
Clealco
Açúcar, Etanol e Energia

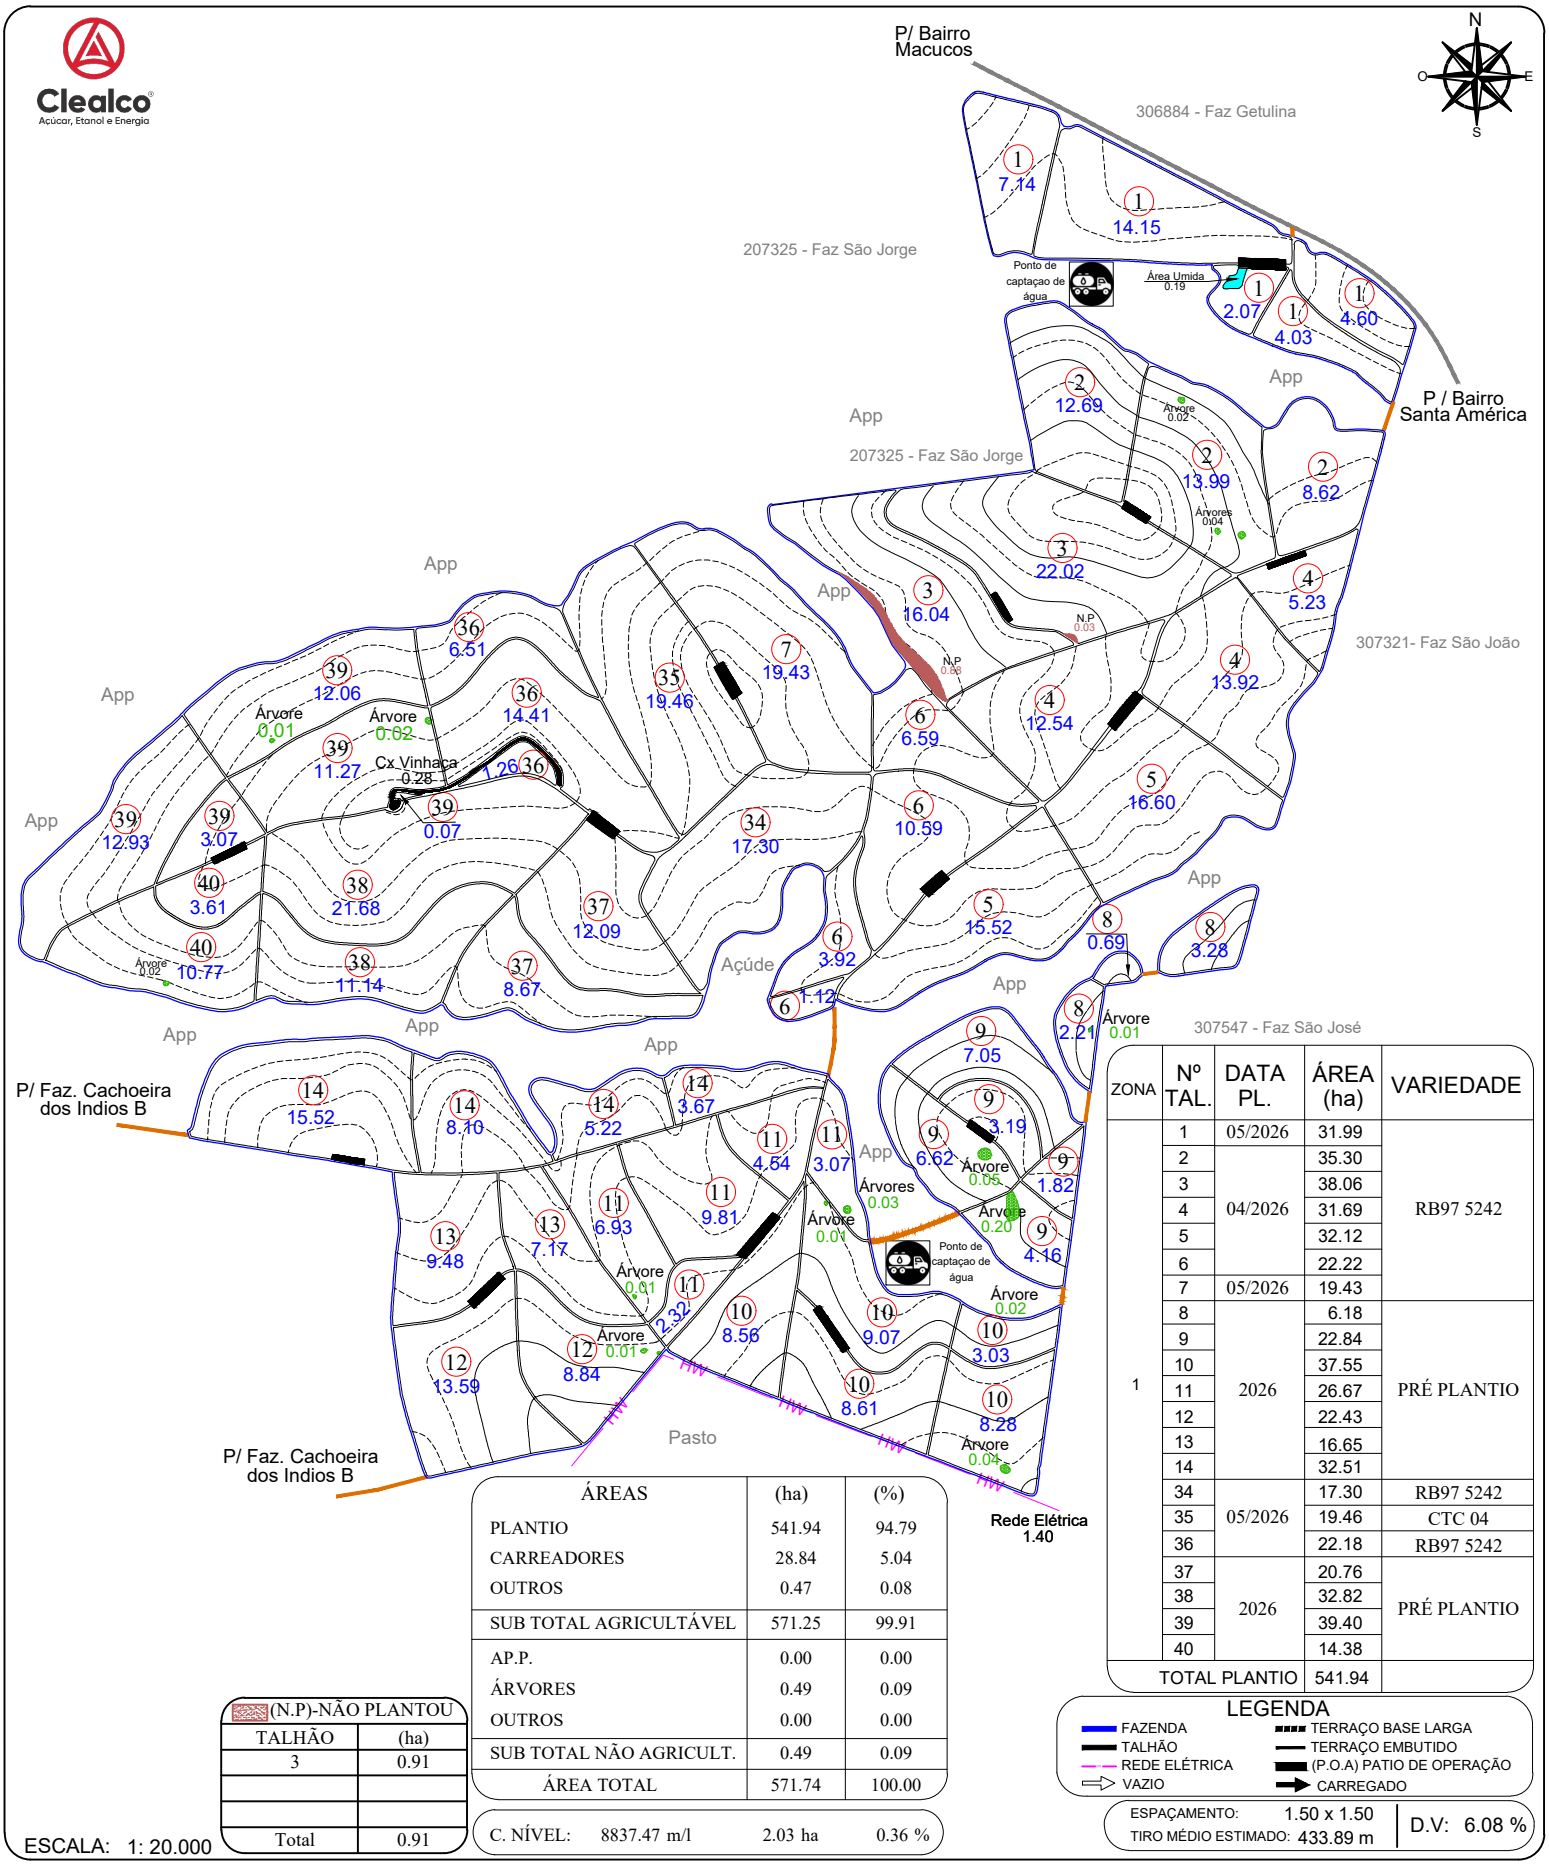

ZONA	Nº TAL.	DATA PL.	ÁREA (ha)	VARIEDADE
1	1	05/2026	31.99	RB97 5242
	2	04/2026	35.30	
	3		38.06	
	4		31.69	
	5		32.12	
	6		22.22	
	7	05/2026	19.43	
	8	2026	6.18	PRÉ PLANTIO
	9		22.84	
	10		37.55	
	11		26.67	
	12		22.43	
	13		16.65	
	14		32.51	
	34	05/2026	17.30	RB97 5242
	35		19.46	CTC 04
	36		22.18	RB97 5242
	37	2026	20.76	PRÉ PLANTIO
	38		32.82	
	39		39.40	
	40		14.38	
TOTAL PLANTIO			541.94	

ÁREAS	(ha)	(%)
PLANTIO	541.94	94.79
CARREADORES	28.84	5.04
OUTROS	0.47	0.08
SUB TOTAL AGRICULTÁVEL	571.25	99.91
AP.P.	0.00	0.00
ÁRVORES	0.49	0.09
OUTROS	0.00	0.00
SUB TOTAL NÃO AGRICULT.	0.49	0.09
ÁREA TOTAL	571.74	100.00

(N.P)-NÃO PLANTOU	
TALHÃO	(ha)
3	0.91
Total	0.91


C. NÍVEL: 8837.47 m/l 2.03 ha 0.36 %

LEGENDA
- FAZENDA
- TALHÃO
- REDE ELÉTRICA
- VAZIO
- TERRAÇO BASE LARGA
- TERRAÇO EMBUTIDO
- (P.O.A) PATIO DE OPERAÇÃO
- CARREGADO

ESPAÇAMENTO: 1.50 x 1.50
TIRO MÉDIO ESTIMADO: 433.89 m
D.V: 6.08 %

ESCALA: 1: 20.000

CROQUI DE ACESSO

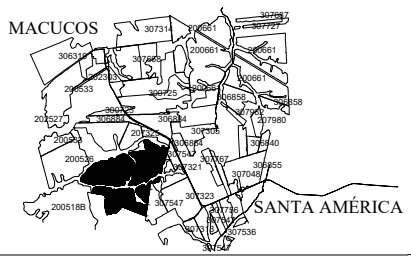

FAZENDA CACHOEIRA DOS ÍNDIOS

PROPRIETÁRIO: PAULO BODINI BARION
COMPRADOR: CLEALCO
MUNICÍPIO: GETULINA - SP

DISTÂNCIAS (km):
UNID. I - Asfalto: 75.30 Terra.: 3.15
UNID.I I - Asfalto: 21.90 Terra.: 3.15

COORDENADAS: E(X): 594159.96 N(Y): 7590897.45
LAT: -21°46'59.3329" LONG: -50°5'21.0761"

LEVANTAMENTO VIA:
- SATÉLITE
- GPS / VANT
- GOOGLE

CLEALCO - AÇÚCAR E ALCOOL S/A - DEPARTAMENTO DE GEOTECNOLOGIA

UNIDADE: II
PARTE: A/B
FUNDO AGRÍCOLA: 200518

M:\01-Mapa de safra\Mapas Atualizados\Clealco\200518 - Fazenda Cachoeira dos Indios (Paulo Bonini Barion)\200518 A - Fazenda Cachoeira dos Indios (Paulo Bonini Barion).dwg

Bruno Gamboa 25/09/26