
Clealco
Açúcar, Etanol e Energia

(N.P)-NÃO PLANTOU 2024	
TALHÃO	(ha)
53	0.02
62	0.57
63	1.09
68	0.74
69	0.22
71	0.12
Total	2.76

(N.P)-NÃO PLANTOU 2022	
TALHÃO	(ha)
40	0.03
72	0.20
73	0.39
74	0.43
75	1.54
76	0.13
Total	2.72

(N.P)-NÃO PLANTOU 2023	
TALHÃO	(ha)
45	0.58
46	0.60
56	0.45
57	0.44
Total	2.07

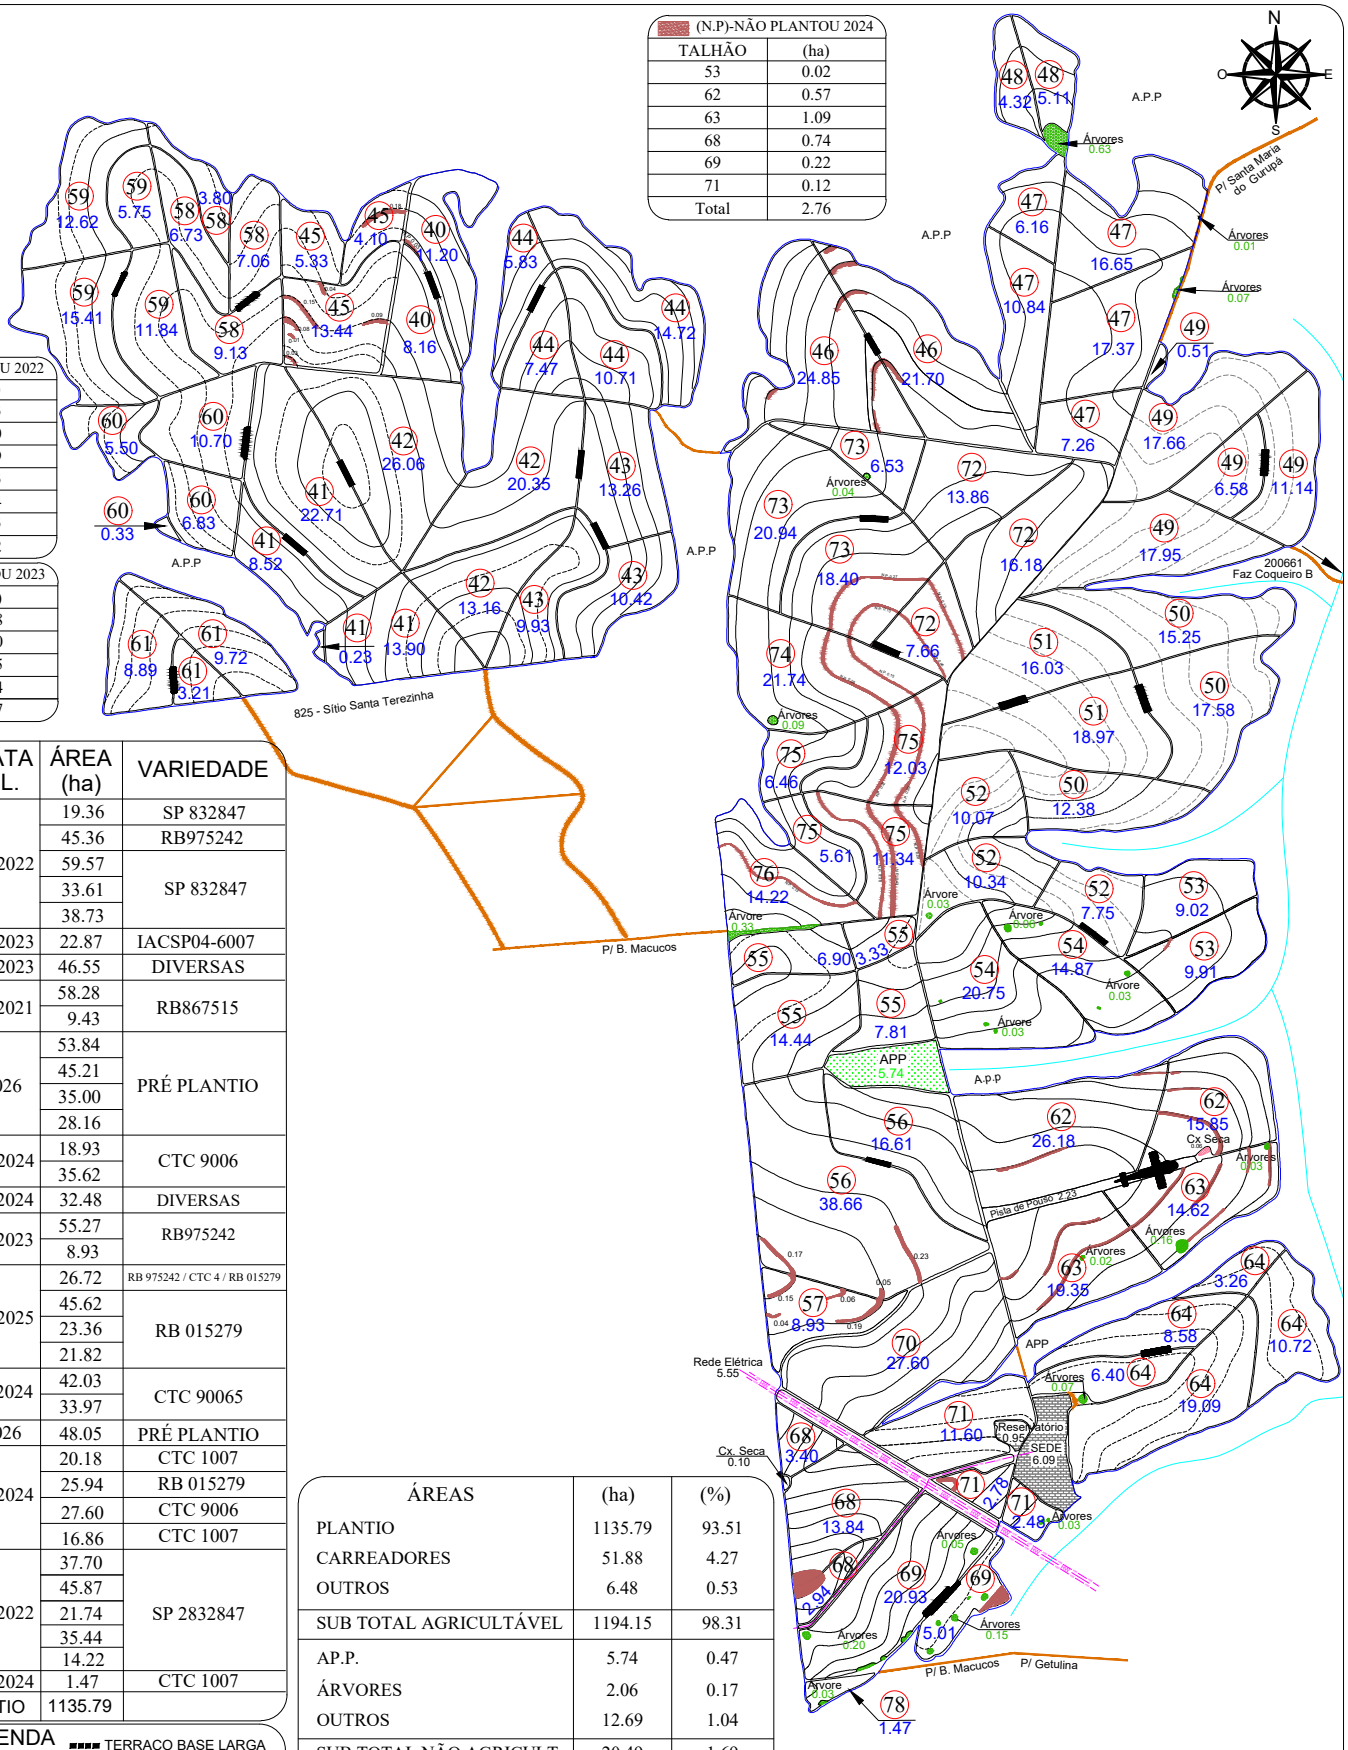

D.V.	Nº TAL.	DATA PL.	ÁREA (ha)	VARIEDADE
5.83%	40	04/2022	19.36	SP 832847
	41		45.36	RB975242
	42		59.57	SP 832847
	43		33.61	
	44		38.73	
	45	02/2023	22.87	IACSP04-6007
	46	03/2023	46.55	DIVERSAS
	47	05/2021	58.28	RB867515
	48		9.43	
	49	2026	53.84	PRÉ PLANTIO
	50		45.21	
	51		35.00	
	52		28.16	
	53	03/2024	18.93	CTC 9006
	54		35.62	
	55	04/2024	32.48	DIVERSAS
5.30%	56	02/2023	55.27	RB975242
	57		8.93	
	58	03/2025	26.72	RB 975242 / CTC 4 / RB 015279
	59		45.62	RB 015279
	60		23.36	
	61		21.82	
	62	04/2024	42.03	CTC 90065
	63		33.97	
	64	2026	48.05	PRÉ PLANTIO
	68	04/2024	20.18	CTC 1007
	69		25.94	RB 015279
	70		27.60	CTC 9006
	71		16.86	CTC 1007
	72	04/2022	37.70	SP 2832847
	73		45.87	
	74		21.74	
	75		35.44	
	76		14.22	
	78	04/2024	1.47	CTC 1007
TOTAL PLANTIO			1135.79	

LEGENDA
- FAZENDA
- TALHÃO
- REDE ELÉTRICA
- TERRAÇO BASE LARGA
- TERRAÇO EMBUTIDO


ESPAÇAMENTO: 1.50 x 1.50
TIRO MÉDIO ESTIMADO: 315.31 m

ÁREAS	(ha)	(%)
PLANTIO	1135.79	93.51
CARREADORES	51.88	4.27
OUTROS	6.48	0.53
SUB TOTAL AGRICULTÁVEL	1194.15	98.31
AP.P.	5.74	0.47
ÁRVORES	2.06	0.17
OUTROS	12.69	1.04
SUB TOTAL NÃO AGRICULT.	20.49	1.69
ÁREA TOTAL	1214.64	100.00

C. NÍVEL: 78751.72 m/l 18.11 ha 1.49 %

ESCALA: 1: 28.000

CROQUI DE ACESSO

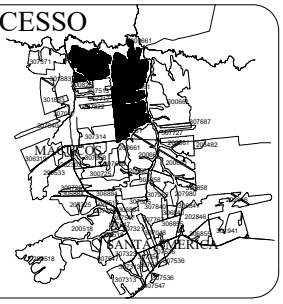

FAZENDA COQUEIRO DO TATU

PROPRIETÁRIO: CLEALCO S/A
COMPRADOR: CLEALCO S/A
MUNICÍPIO: GETULINA - SP

DISTÂNCIAS (km):
UNID. I - Asfalto: 71.00 Terra.: 5.60
UNID.I I - Asfalto: 13.00 Terra.: 5.60
UNID. III -Asfalto: 43.30 Terra.: 9.30

COORDENADAS: E(X): 592878.47 N(Y): 7599354.32
LAT: -21°42'24.5475" LONG: -50°6'7.4068"
CLEALCO - AÇÚCAR E ALCOOL S/A - DEPARTAMENTO DE GEOTECNOLOGIA

LEVANTAMENTO VIA:
- SATÉLITE
- GPS / VANT
- GOOGLE

UNIDADE: II
PARTE: C/C
FUNDO AGRÍCOLA: 200661

M:\01-Mapa de safra\Mapas Atualizados\Clealco\200661 - Fazenda Coqueiro do Tatu (Clealco)\200661 C - Fazenda Coqueiro do Tatu - (Clealco).dwg

Peterson Santos 10/08/2026