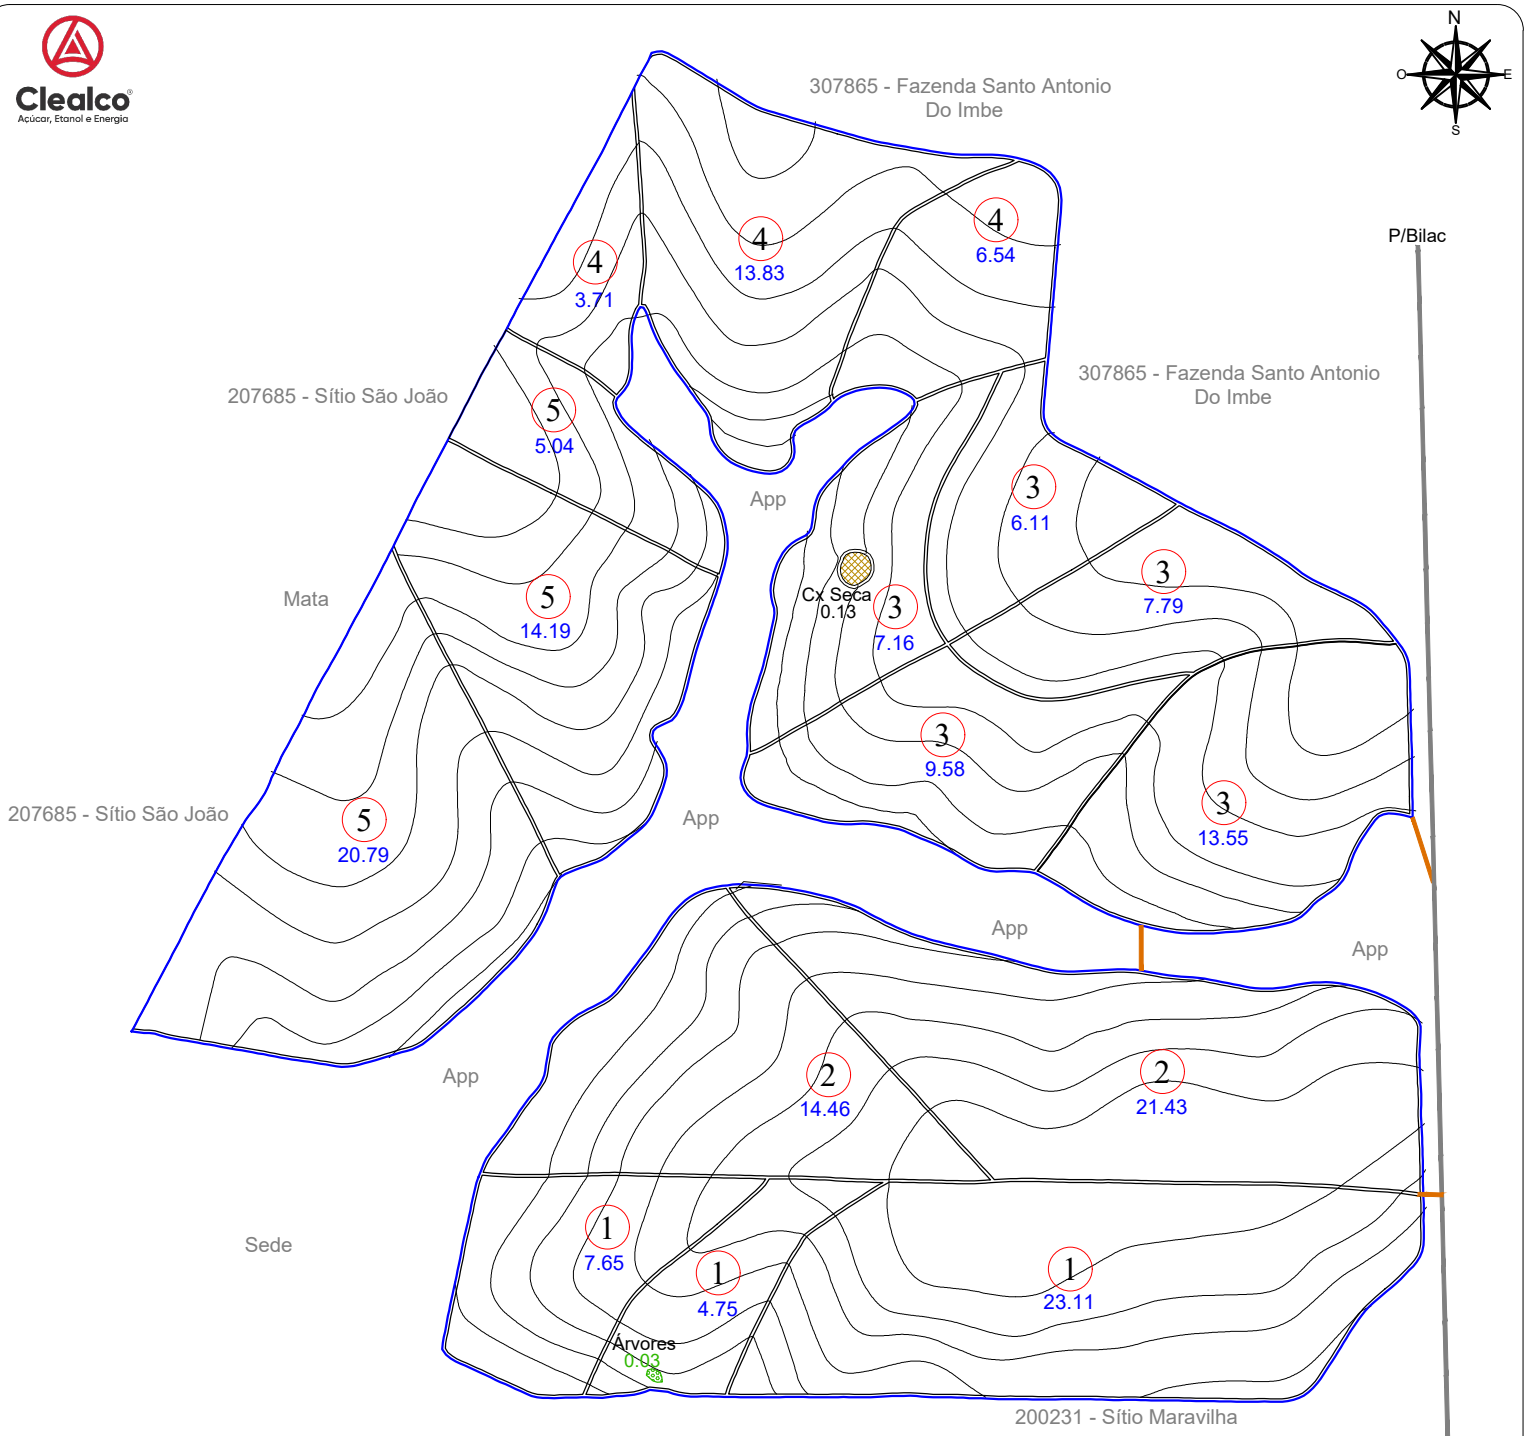


Nº TAL.	DATA PL.	ÁREA (ha)	VARIEDADE
1	05/2020	35.51	RB97 5201
2		35.89	
3		44.19	
4		24.08	
5		40.02	
TOTAL PLANTIO		179.69	

ÁREAS	(ha)	(%)
PLANTIO	179.69	96.43
CARREADORES	6.50	3.49
OUTROS	0.13	0.07
SUB TOTAL AGRICULTÁVEL	186.32	99.98
AP.P.	0.00	0.00
ÁRVORES	0.03	0.02
OUTROS	0.00	0.00
SUB TOTAL NÃO AGRICULT.	0.03	0.02
ÁREA TOTAL	186.35	100.00

LEGENDA


- FAZENDA
- TALHÃO
- REDE ELÉTRICA
- TERRAÇO BASE LARGA
- TERRAÇO EMBUTIDO
- (P.O.A) PATIO DE OPERAÇÃO

ESPAÇAMENTO: 1.50 x 1.50
TIRO MÉDIO ESTIMADO: 000.00 m
D.V: 0.00 %

C. NÍVEL: 30115.35 m/l 6.93 ha 3.72 %

ESCALA: 1: 10.500

CROQUI DE ACESSO

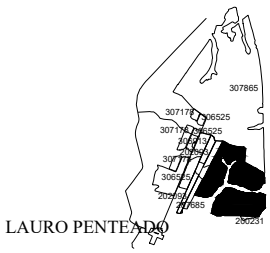

LAURO PENTEADO

FAZENDA OURO PRETO

PROPRIETÁRIO: NELSON YOSUKE MATSUOKA
COMPRADOR: CLEALCO
MUNICÍPIO: CLEMENTINA - SP

DISTÂNCIAS (km):
UNID. I - Asfalto: 8.80 Terra.: 1.50
UNID.I I - Asfalto: 64.00 Terra.: 1.50

COORDENADAS: E(X): 558458.48 N(Y): 7621673.72
LAT: -21°30'23.9093" LONG: -50°26'8.1396"
CLEALCO - AÇÚCAR E ALCOOL S/A - DEPARTAMENTO DE GEOTECNOLOGIA

LEVANTAMENTO VIA:
SATÉLITE
GPS / VANT
GOOGLE

UNIDADE: I
PARTE: A/A
FUNDO AGRÍCOLA: 201027

M:\01-Mapa de safra\Mapas Atualizados\Clealco\201027 - Fazenda Ouro Preto (Nelson Yosuke Matsuoka)\201027 - Fazenda Ouro Preto (Nelson Yosuke Matsuoka).dwg

Bruno Gamboa 11/12/25