

Clealco
Açúcar, Etanol e Energia

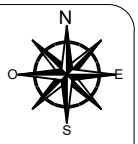

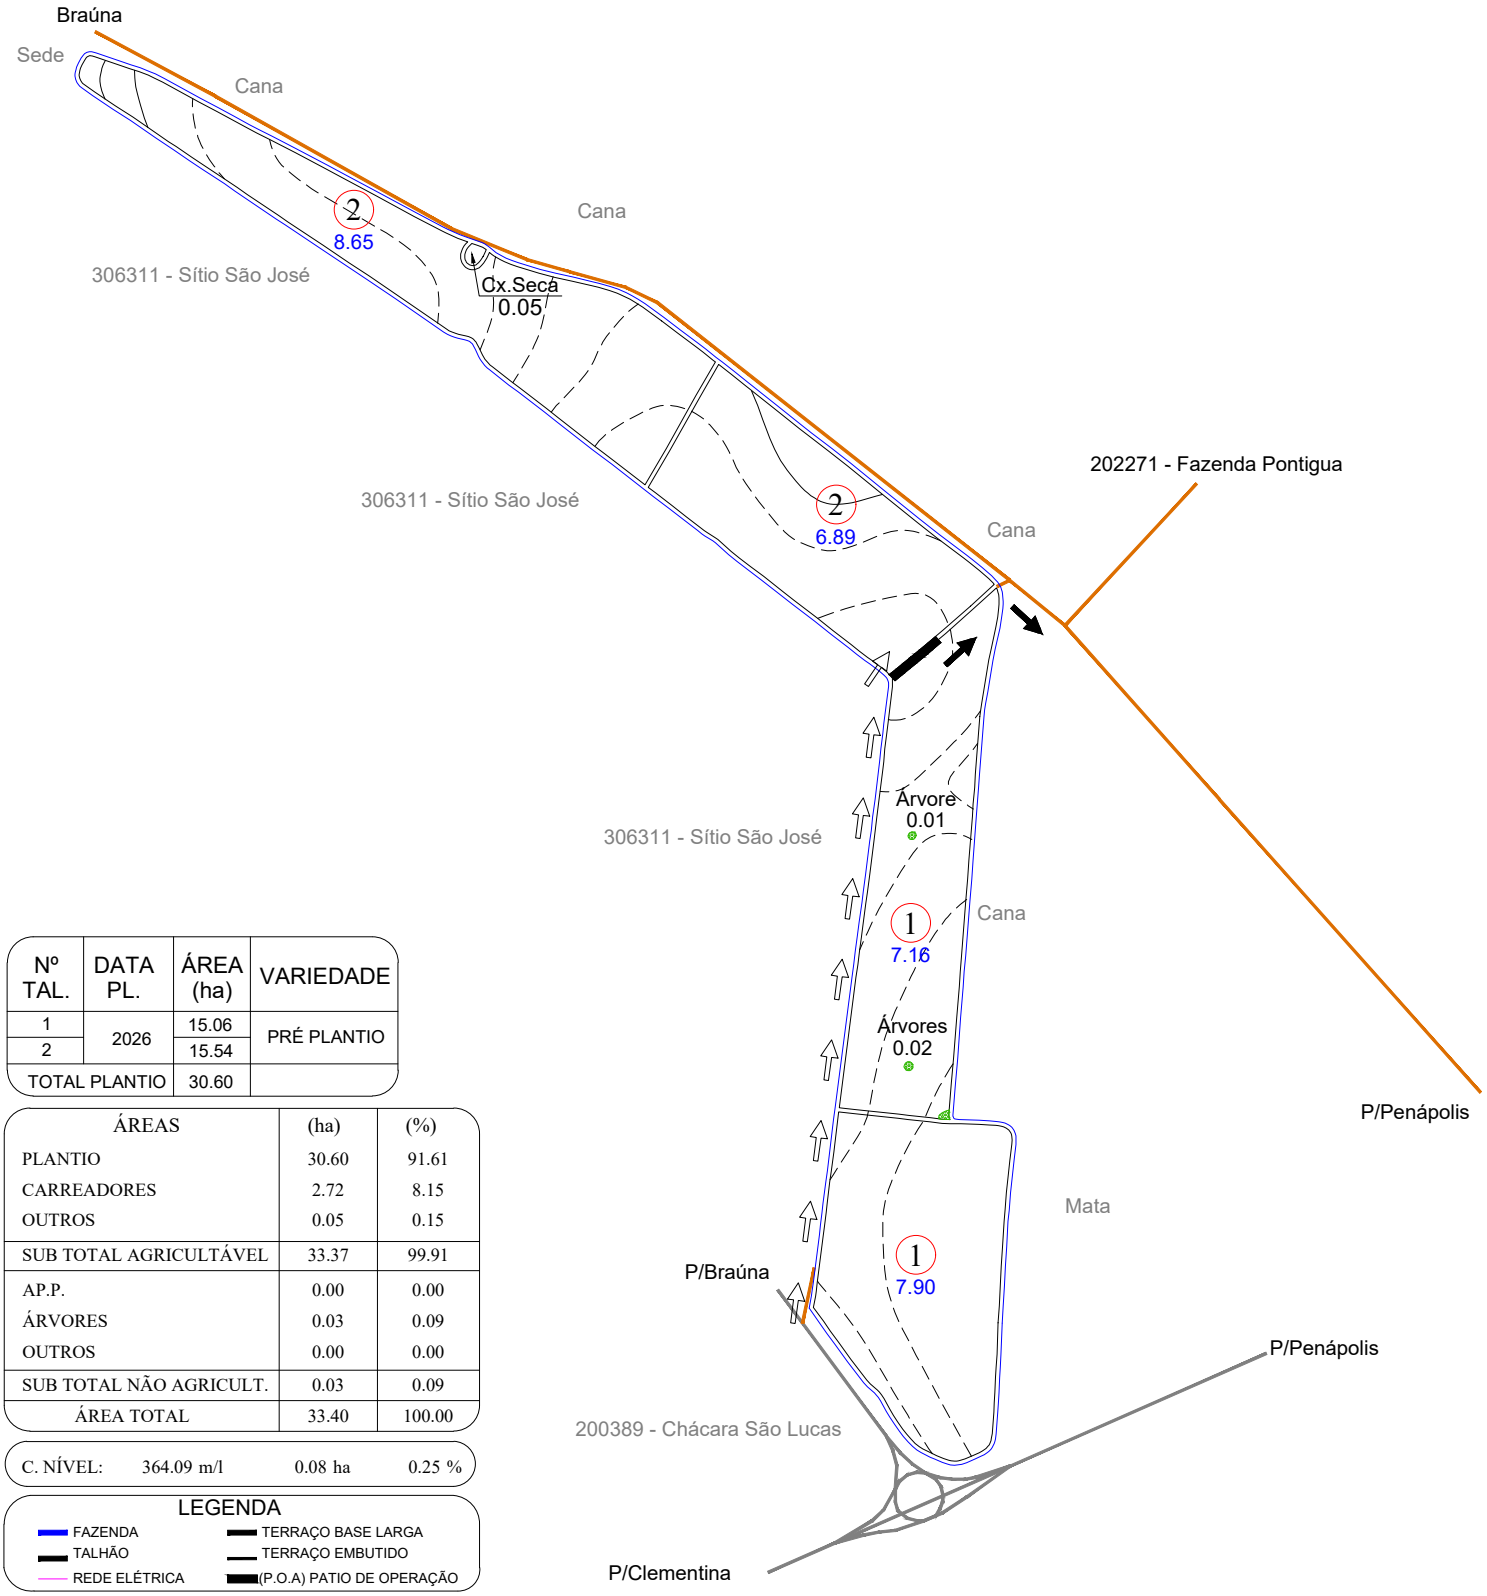

Nº TAL.	DATA PL.	ÁREA (ha)	VARIEDADE
1	2026	15.06	PRÉ PLANTIO
2		15.54	
TOTAL PLANTIO		30.60	

ÁREAS	(ha)	(%)
PLANTIO	30.60	91.61
CARREADORES	2.72	8.15
OUTROS	0.05	0.15
SUB TOTAL AGRICULTÁVEL	33.37	99.91
AP.P.	0.00	0.00
ÁRVORES	0.03	0.09
OUTROS	0.00	0.00
SUB TOTAL NÃO AGRICULT.	0.03	0.09
ÁREA TOTAL	33.40	100.00

C. NÍVEL: 364.09 m/l 0.08 ha 0.25 %


LEGENDA

- FAZENDA
- TALHÃO
- REDE ELÉTRICA
- TERRAÇO BASE LARGA
- TERRAÇO EMBUTIDO
- (P.O.A) PATIO DE OPERAÇÃO

ESPAÇAMENTO: 1.50 x 1.50
TIRO MÉDIO ESTIMADO: 225.13 m
D.V: 0.00 %

ESCALA: 1: 9.500

CROQUI DE ACESSO

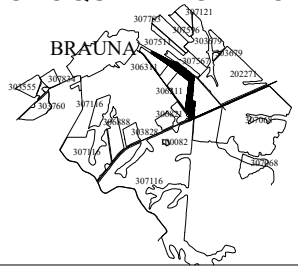

SÍTIO UNIÃO

PROPRIETÁRIO: MARINA DIVANIR PIRANI P
COMPRADOR: CLEALCO
MUNICÍPIO: BRAUNA - SP

DISTÂNCIAS (km):
UNID. I - Asfalto: 18.00 Terra.: 1.00
UNID.I I - Asfalto: 76.00 Terra.: 1.00

COORDENADAS: E(X): 572675.43 N(Y): 7621248.10
LAT: -21°30'35.8792" LONG: -50°17'53.9554"

CLEALCO - AÇÚCAR E ALCOOL S/A - DEPARTAMENTO DE GEOTECNOLOGIA

LEVANTAMENTO VIA:
- SATÉLITE
- GPS / VANT
- GOOGLE

UNIDADE: I
PARTE: A/A
FUNDO AGRÍCOLA: 201150

M:\01-Mapa de safra\Mapas Atualizados\Clealco\201150 - Sítio União (Marina Divanri Pirani Peres)\201150 - Sítio União (Marina Divanri Pirani Peres).dwg

Bruno Gamboa 08/09/26