ZONA D.V.	Nº TAL.	DATA PL.	ÁREA (ha)	VAR.
1 5.81 %	2521	07/2021	17.11	RB 975242
	2621		36.76	
	2721		15.96	
	2821		18.26	
	2921		32.47	
	3021		19.98	
	3121		31.70	
	3222		48.13	
	3322	03/2022	41.46	
	3422		40.02	
TOTAL PLANTIO			301.85	--------


ÁREAS	(ha)	(%)
PLANTIO	301.85	93.97
CARREADORES	18.89	5.88
OUTROS	0.46	0.14
SUB TOTAL AGRICULTÁVEL	321.20	100.00
AP.P.	0.00	0.00
ÁRVORES	0.01	0.00
OUTROS	0.00	0.00
SUB TOTAL NÃO AGRICULT.	0.01	0.00
ÁREA TOTAL	321.21	100.00

C. NÍVEL: 24799.71 m/l 5.70 ha 1.78 %

LEGENDA


- FAZENDA
- TALHÃO
- CURVA DE NÍVEL
- CARREADOR
- CONFRONTANTE
- REDE ELÉTRICA
- TRAJETO VAZIO
- TRAJETO CARREGADO

PLANTIO MANUAL - ESPAÇAMENTO: 1.50 X 1.50
TIRO MÉDIO ESTIMADO: 586.69m

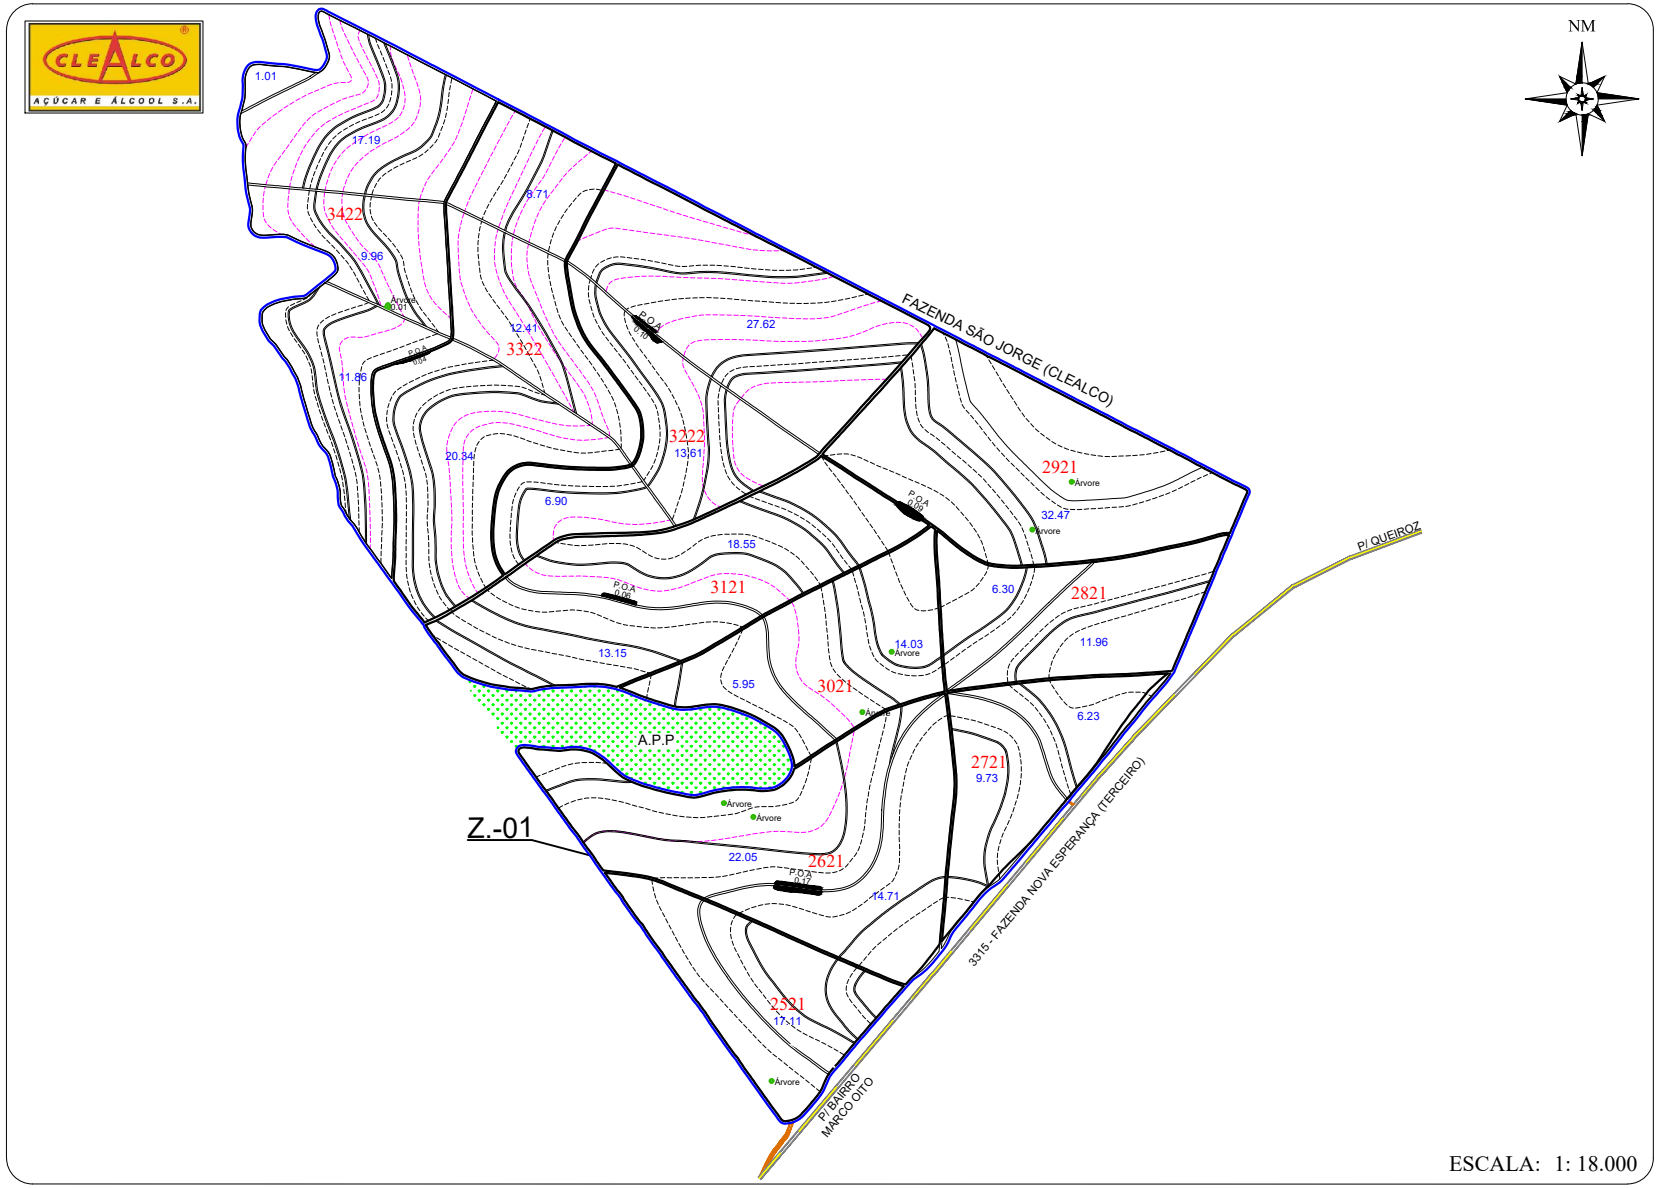

ESCALA: 1: 18.000

CROQUI DE ACESSO

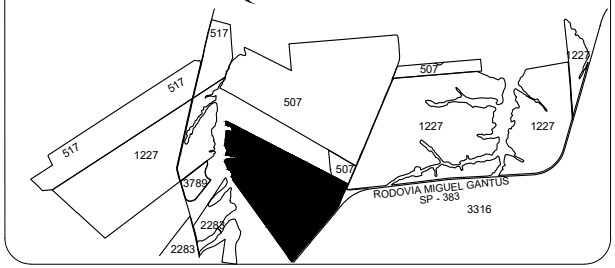

FAZENDA SÃO BENTO

PROPRIETÁRIO: MARGARIDA H. T. YABUTA
COMPRADOR: CLEALCO S/A
MUNICÍPIO: QUEIROZ - SP

DISTÂNCIAS (km):

UNID. I - Asfalto:	35.00	Terra.:	24.40
UNID.I I - Asfalto:	15.50	Terra.:	1.50
UNID. III -Asfalto:	52.00	Terra.:	1.50

COORDENADAS: E(X): 571.198,00 N(Y): 7.584.014,00
LAT: 21°50'46,79923" LONG: 50°18'39,56635"

CLEALCO - AÇÚCAR E ALCOOL S/A - DEPARTAMENTO DE TOPOGRAFIA

UNIDADE: II
PARTE: A/C
FUNDO AGRÍCOLA: 201227