D.V.	Nº TAL.	DATA PL.	ÁREA (ha)	VARIEDADE
4.22%	1	06/2023	38.28	RB 985476
	2		18.54	
	3		21.94	RB 966928
	4		13.31	
TOTAL PLANTIO			92.07	--------

ÁREAS	(ha)	(%)
PLANTIO	92.07	93.46
CARREADORES	5.55	5.63
OUTROS	0.27	0.27
SUB TOTAL AGRICULTÁVEL	97.89	99.38
AP.P.	0.00	0.00
ÁRVORES	0.07	0.07
OUTROS	0.54	0.55
SUB TOTAL NÃO AGRICULT.	0.61	0.62
ÁREA TOTAL	98.50	100.00


C. NÍVEL: 15318.61 m/l 3.52 ha 3.58 %

LEGENDA

- FAZENDA
- TALHÃO
- CURVA DE NÍVEL
- CARREADOR
- CONFRONTANTE
- REDE ELÉTRICA
- TRAJETO VAZIO
- TRAJETO CARREGADO


PLANTIO MANUAL - ESPAÇAMENTO: 1.50 X 1.50
TIRO MÉDIO ESTIMADO: 204.63

Clealco
Açúcar, Etanol e Energia

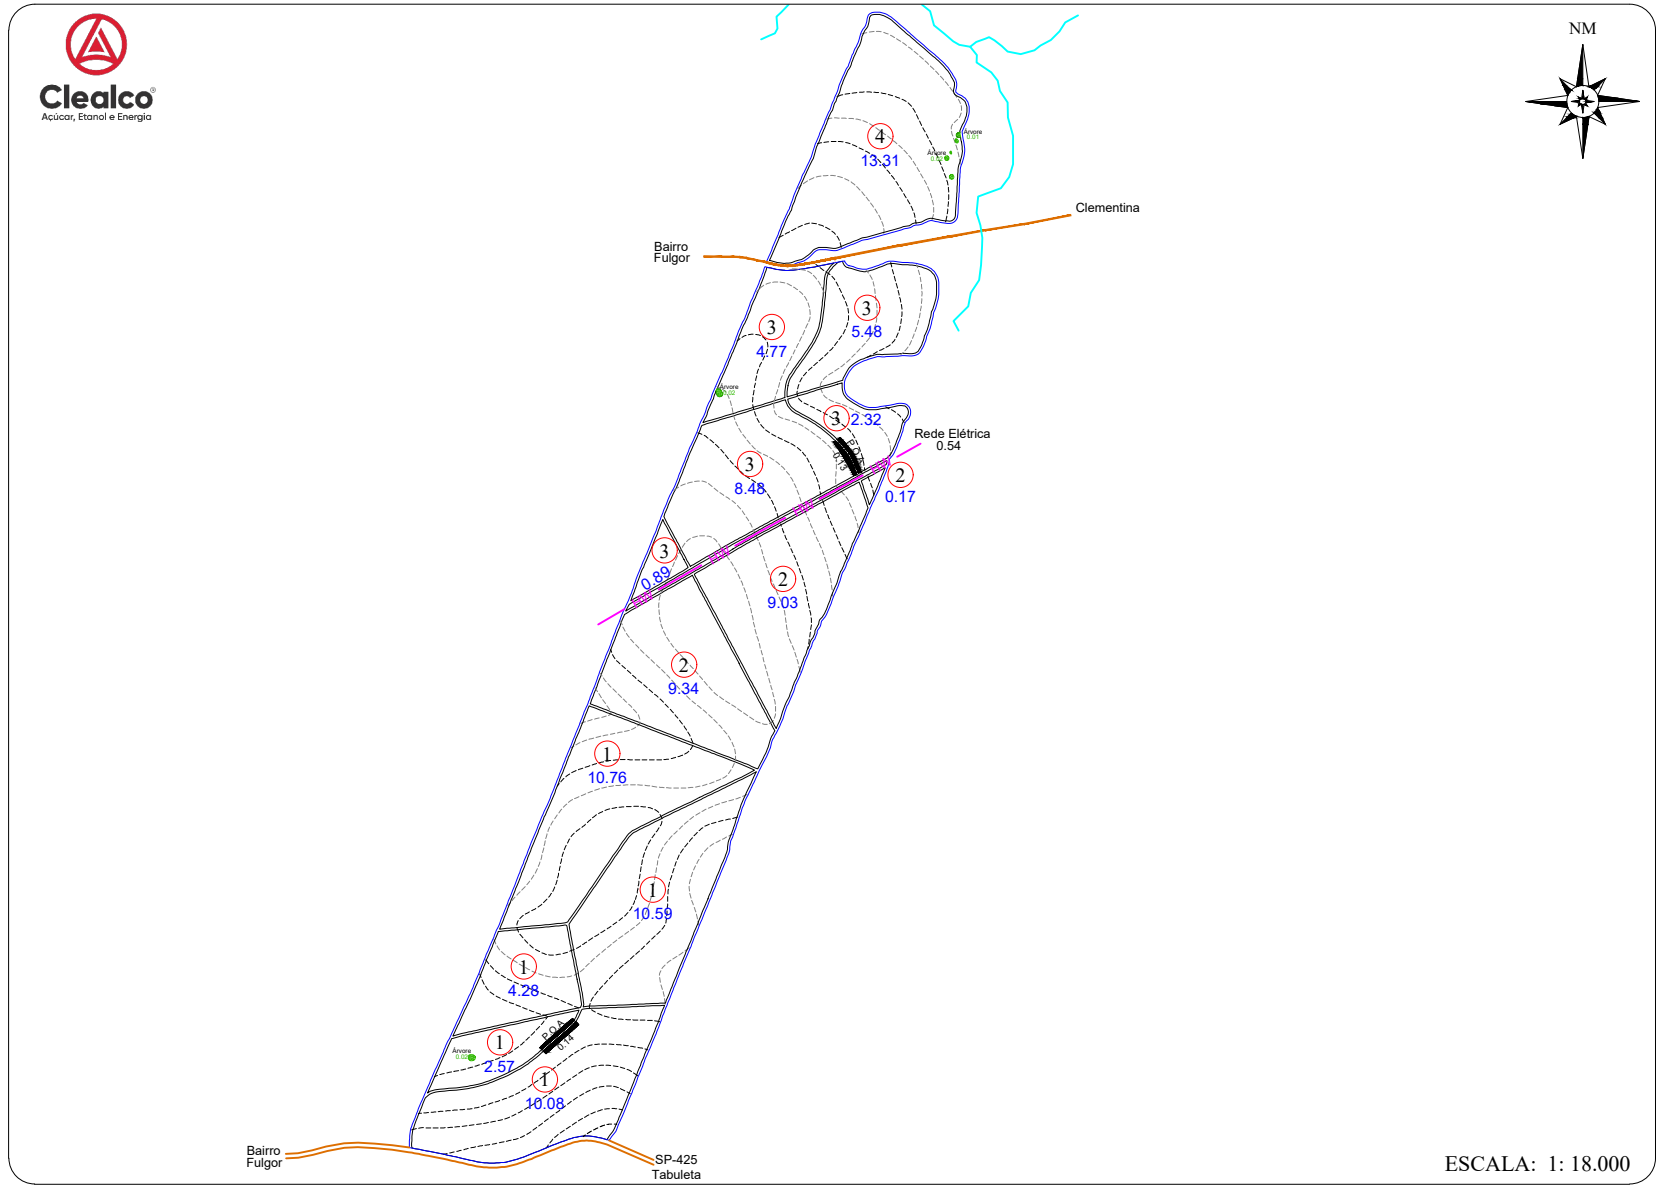

ESCALA: 1: 18.000

CROQUI DE ACESSO

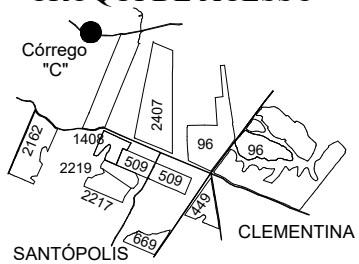

SÍTIO SÃO LUIZ

PROPRIETÁRIO: SUMIE YDA
COMPRADOR: CLEALCO S/A
MUNICÍPIO: CLEMENTINA - SP

DISTÂNCIAS (km):
UNID. I - Asfalto: 6.50 Terra.: 3.50
UNID.I I - Asfalto: 54.00 Terra.: 3.50
UNID. III -Asfalto: 0.00 Terra.: 0.00

COORDENADAS: E(X): 553562.51 N(Y): 7614509.87
LAT: -21°34'17.4640" LONG: -50°28'57.4794"

CLEALCO - AÇÚCAR E ALCOOL S/A - DEPARTAMENTO DE TOPOGRAFIA

UNIDADE: I
PARTE: A/A
FUNDO AGRÍCOLA: 201244