ZONA D.V.	Nº TAL.	DATA PL.	ÁREA (ha)	VAR.
1 4.38 %	1	04/2023	8.99	IACSP01-5503
	2		24.36	
	3		34.53	
	4		40.84	VIVEIRO
TOTAL PLANTIO			108.72	--------

ÁREAS	(ha)	(%)
PLANTIO	108.72	93.08
CARREADORES	6.20	5.31
OUTROS	0.26	0.22
SUB TOTAL AGRICULTÁVEL	115.18	98.61
AP.P.	0.37	0.32
ÁRVORES	0.91	0.78
OUTROS	0.34	0.29
SUB TOTAL NÃO AGRICULT.	1.62	1.39
ÁREA TOTAL	116.80	100.00


C. NÍVEL: 1202.39 m/l 0.28 ha 0.24 %

LEGENDA

- FAZENDA
- TALHÃO
- CURVA DE NÍVEL
- CARREADOR
- CONFRONTANTE
- REDE ELÉTRICA
- TRAJETO VAZIO
- TRAJETO CARREGADO


PLANTIO MANUAL - ESPAÇAMENTO: 1.50 X 1.50
TIRO MÉDIO ESTIMADO: 286.26 m

Clealco
Açúcar, Etanol e Energia

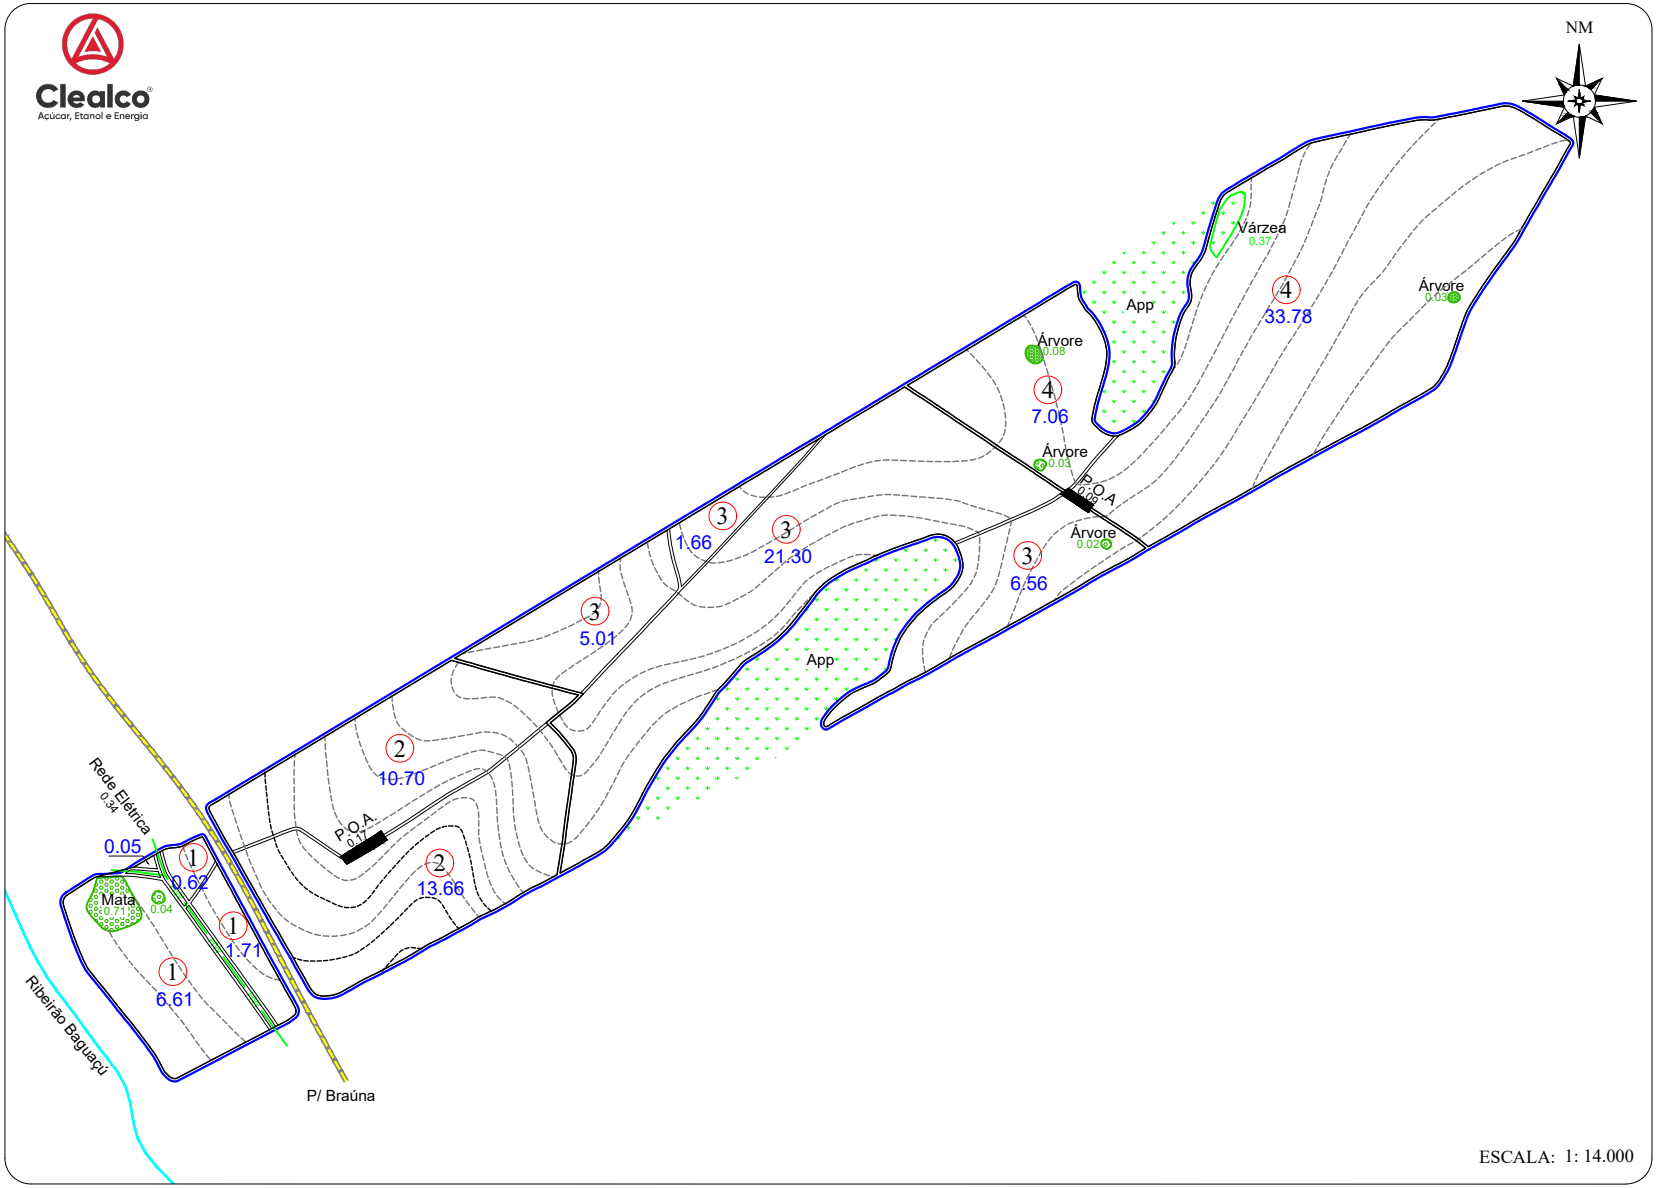

ESCALA: 1: 14.000

CROQUI DE ACESSO

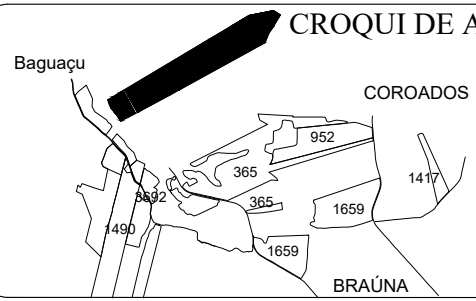

FAZENDA SÃO GABRIEL II

PROPRIETÁRIO: JOSÉ ZANCANER NETO
ARRENDATÁRIO: CLEALCO S/A
MUNICÍPIO: COROADOS

DISTÂNCIAS (km):
UNID. I - Asfalto: 18.70 Terra.: 01.50
UNID.I I - Asfalto: 72.00 Terra.: 01.50
UNID. III -Asfalto: 28.00 Terra.: 01.50

COORDENADAS: E(X): 567343.20 N(Y): 7627416.79
LAT: -21°27'15.9967" LONG: -50°21'0.1737"

CLEALCO - AÇÚCAR E ALCOOL S/A - DEPARTAMENTO DE TOPOGRAFIA

UNIDADE: I
PARTE: A/A
FUNDO AGRÍCOLA: 201491

M:\01-Mapa de safra\Mapas Atualizados\Clealco\201491 - Fazenda São Gabriel II (José Zancaner Neto)\201491 - Fazenda São Gabriel II (José Zancaner Neto).dwg

Bruno Gamboa 16/05/23