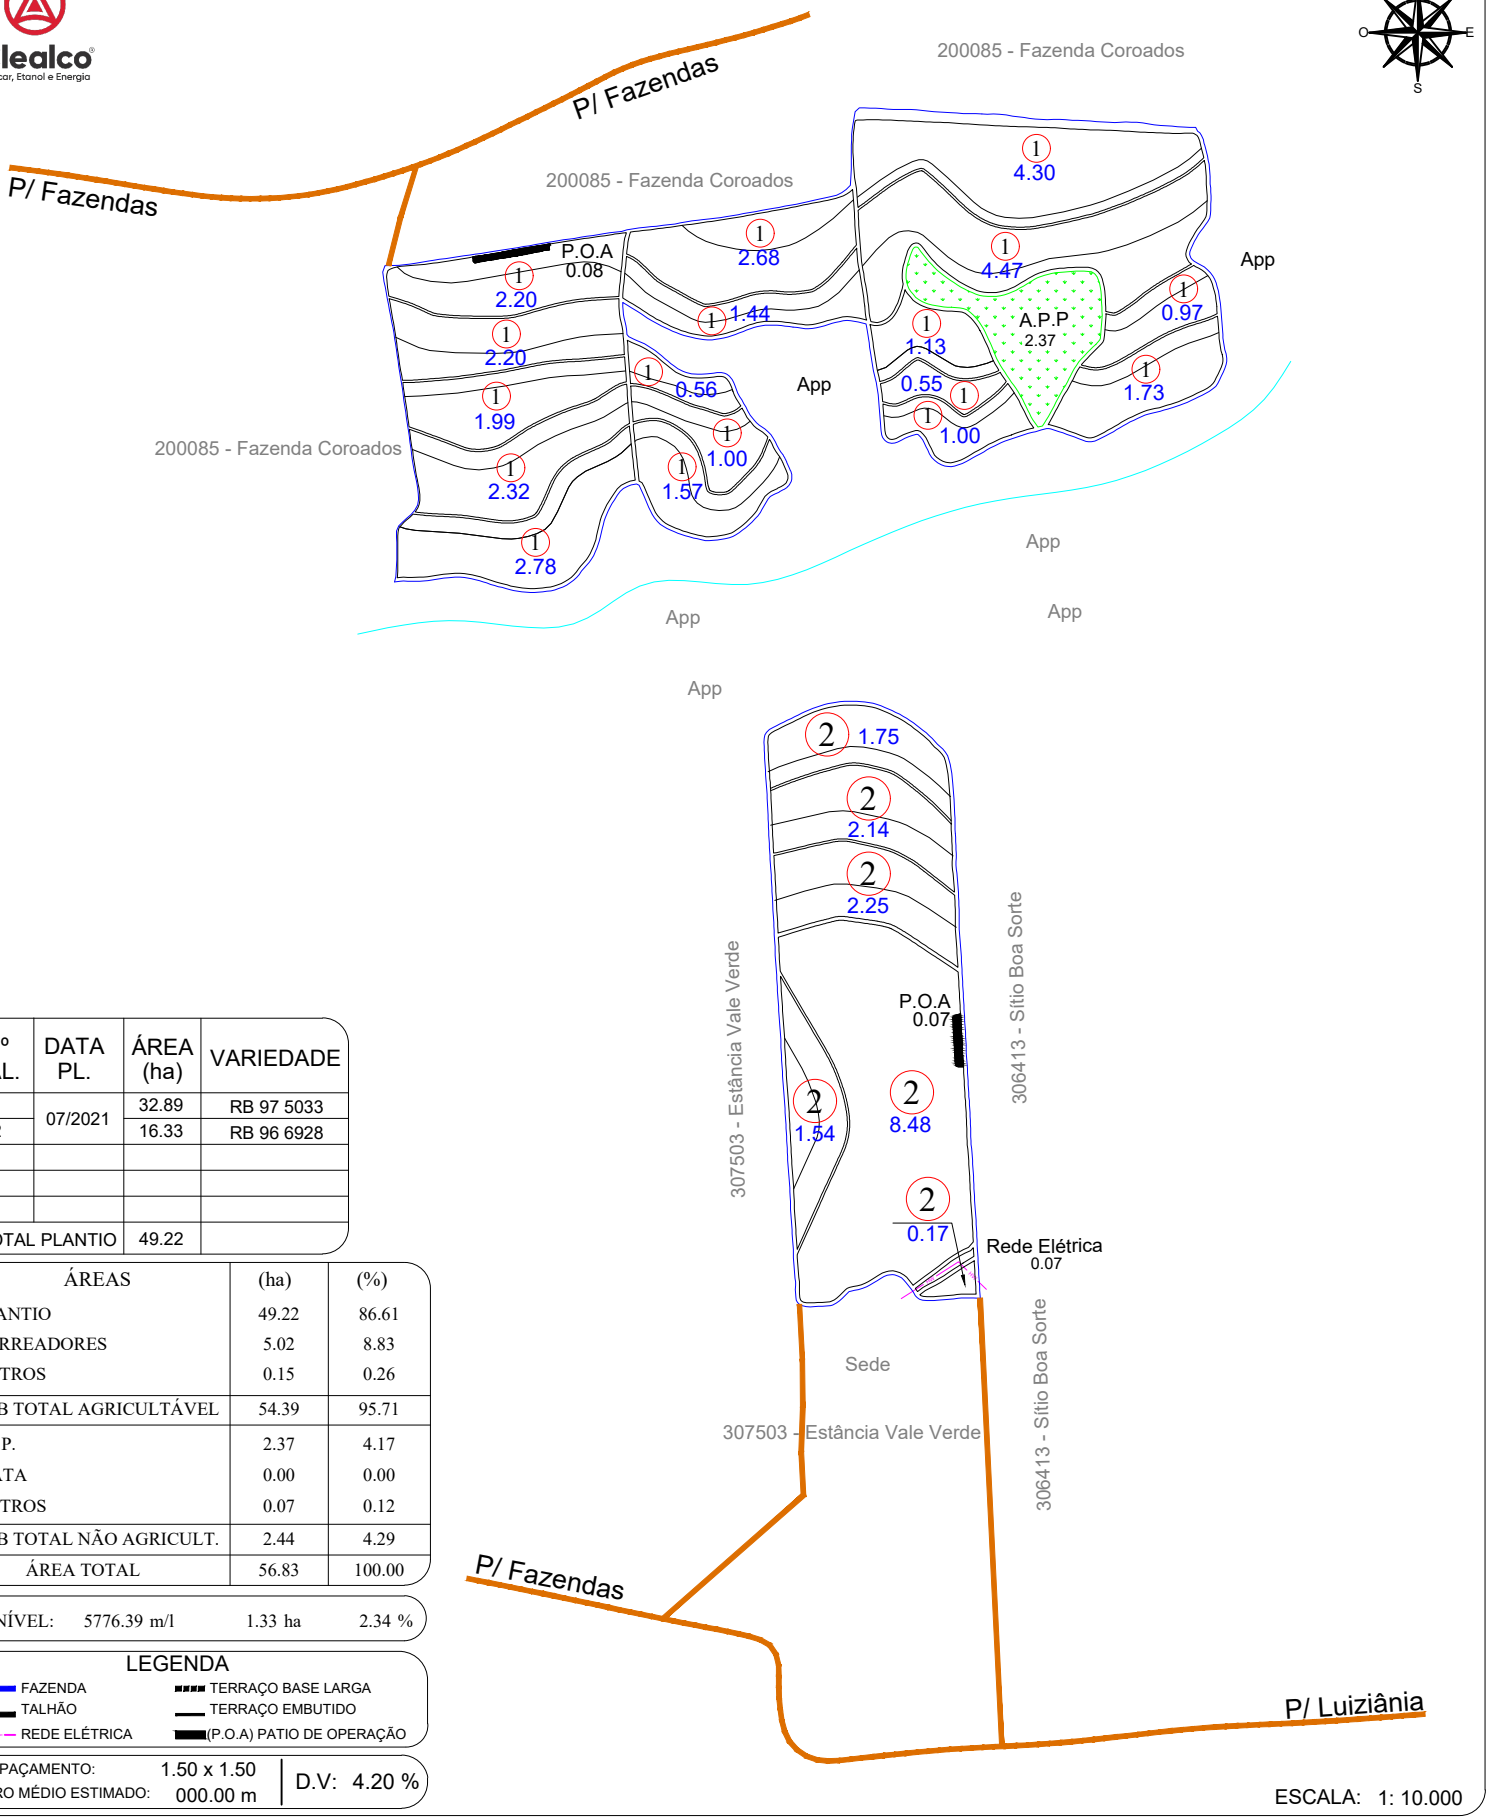


Nº TAL.	DATA PL.	ÁREA (ha)	VARIEDADE
1	07/2021	32.89	RB 97 5033
2		16.33	RB 96 6928
TOTAL PLANTIO		49.22	

ÁREAS	(ha)	(%)
PLANTIO	49.22	86.61
CARREADORES	5.02	8.83
OUTROS	0.15	0.26
SUB TOTAL AGRICULTÁVEL	54.39	95.71
AP.P.	2.37	4.17
MATA	0.00	0.00
OUTROS	0.07	0.12
SUB TOTAL NÃO AGRICULT.	2.44	4.29
ÁREA TOTAL	56.83	100.00

C. NÍVEL: 5776.39 m/l 1.33 ha 2.34 %


LEGENDA

- FAZENDA
- TALHÃO
- REDE ELÉTRICA
- TERRAÇO BASE LARGA
- TERRAÇO EMBUTIDO
- (P.O.A) PATIO DE OPERAÇÃO

ESPAÇAMENTO: 1.50 x 1.50
TIRO MÉDIO ESTIMADO: 000.00 m
D.V: 4.20 %

ESCALA: 1: 10.000

CROQUI DE ACESSO

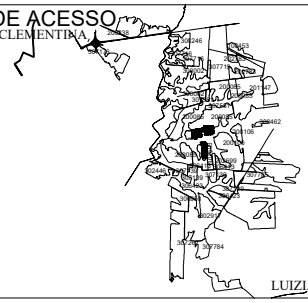

ESTÂNCIA BELA VISTA

PROPRIETÁRIO: JOSÉ ANTONIO C. DE LIMA
COMPRADOR: CLEALCO
MUNICÍPIO: BRAÚNA - SP

DISTÂNCIAS (km):
UNID. I - Asfalto: 0.00 Terra.: 9.00
UNID.I I - Asfalto: 31.00 Terra.: 11.00

COORDENADAS: E(X): 563410.06 N(Y): 7609605.85
LAT: -21°36'55.8023" LONG: -50°23'14.3949"

CLEALCO - AÇÚCAR E ALCOOL S/A - DEPARTAMENTO DE GEOTECNOLOGIA

LEVANTAMENTO VIA:
SATÉLITE
GPS / VANT
GOOGLE

UNIDADE: I
PARTE: A/A
FUNDO AGRÍCOLA: 202076

M:\01-Mapa de safra\Mapas Atualizados\Clealco\202076 - Estância Bela Vista (José Antonio de Lima)\202076 - Estância Bela Vista (José Antonio de Lima).dwg

Bruno Gamboa 24/09/25