ZONA D.V.	Nº TAL.	DATA PL.	ÁREA (ha)	VAR.
1 4.13 %	2	06/2022	20.75	CTC9001
	3		25.40	
	4		21.85	
	5		8.46	
	6		4.31	
TOTAL PLANTIO			80.77	--------


ÁREAS	(ha)	(%)
PLANTIO	80.77	92.74
CARREADORES	6.11	7.02
ADUTORA	0.21	0.24
SUB TOTAL AGRICULTÁVEL	87.09	100.00
AP.P.	0.00	0.00
MATA	0.00	0.00
OUTROS	0.00	0.00
SUB TOTAL NÃO AGRICULT.	0.00	0.00
ÁREA TOTAL	87.09	100.00

C. NÍVEL: 8266.43 m/l 1.90 ha 2.18 %


LEGENDA

- FAZENDA
- TALHÃO
- CURVA DE NÍVEL
- CARREADOR
- CONFRONTANTE
- REDE ELÉTRICA
- TRAJETO VAZIO
- TRAJETO CARREGADO

PLANTIO MANUAL - ESPAÇAMENTO: 1.50 X 1.50
TIRO MÉDIO ESTIMADO: 644.21m

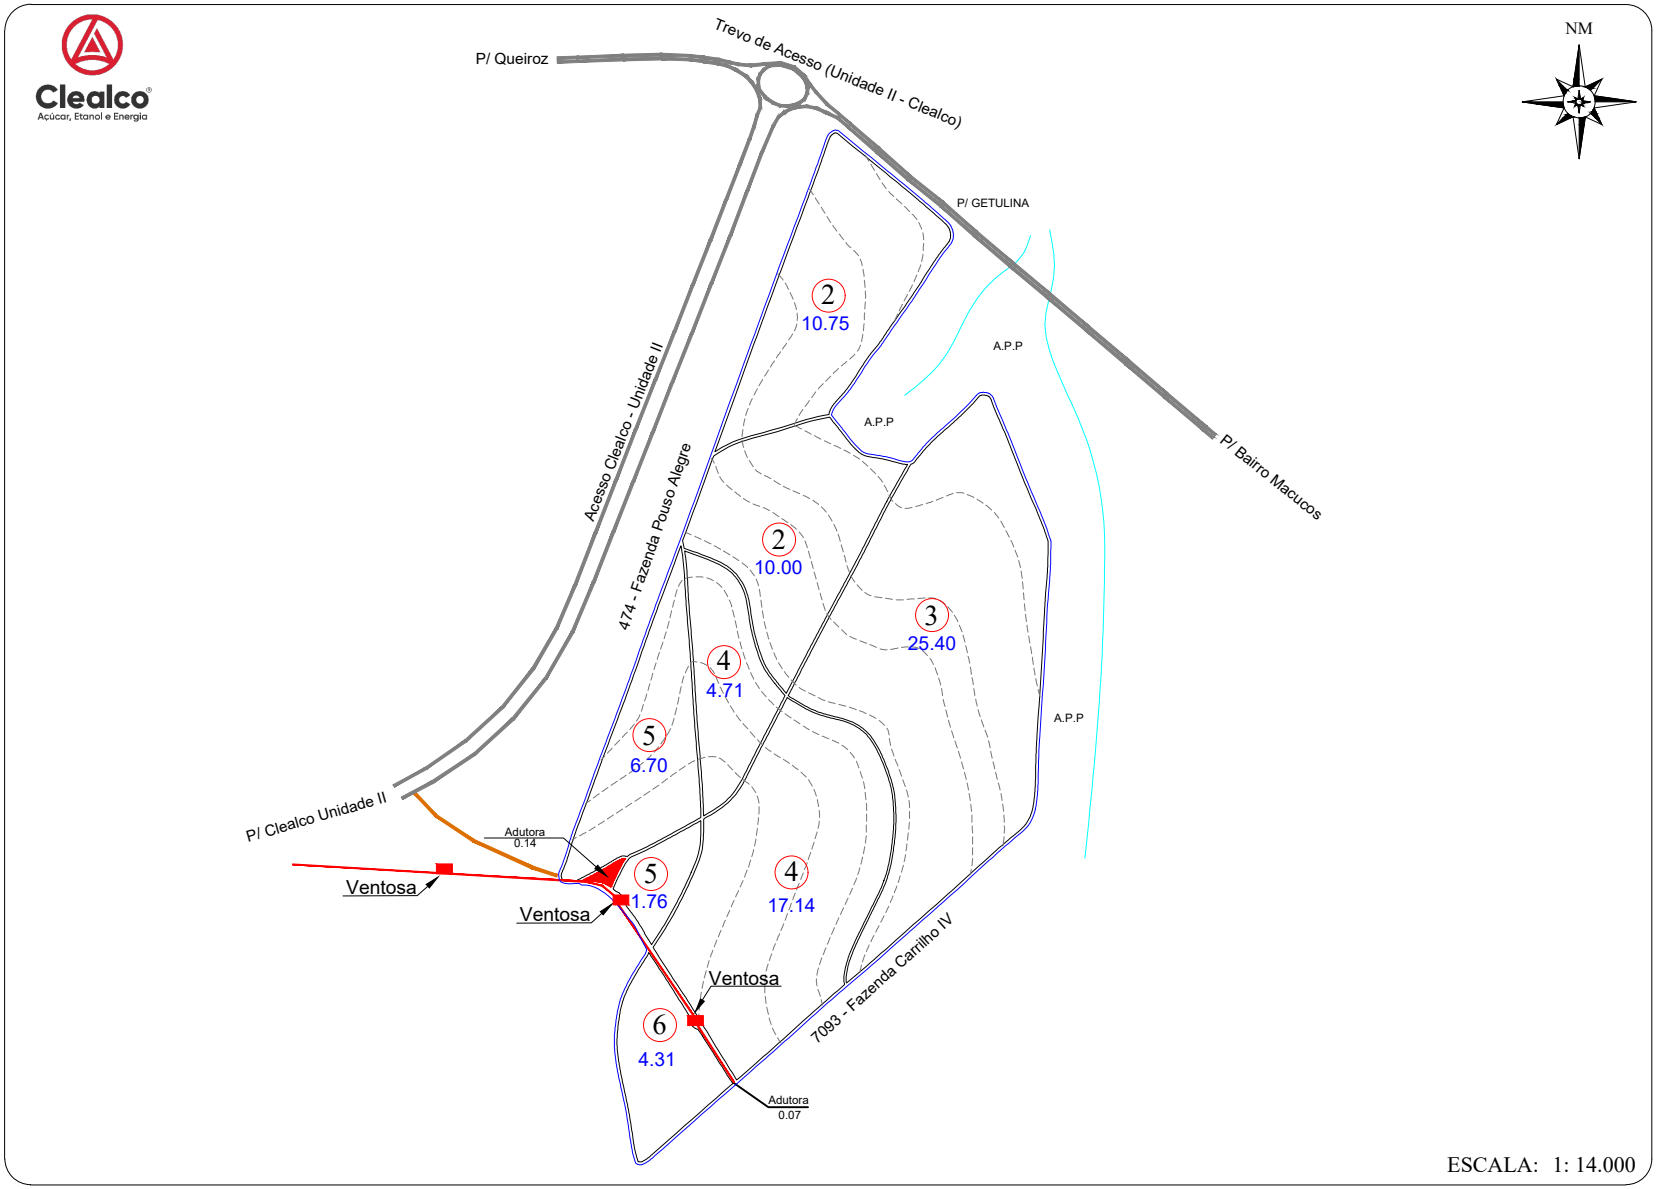

CROQUI DE ACESSO

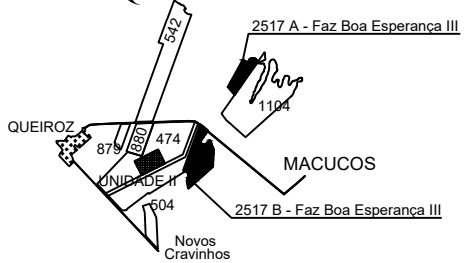

FAZENDA BOA ESPERANÇA III

PROPRIETÁRIO: AMÉLIA ACERBI JORGE
COMPRADOR: CLEALCO S/A
MUNICÍPIO: QUEIROZ - SP

DISTÂNCIAS (km):
UNID. I - Asfalto: 57.20 Terra.: 1.20
UNID.I I - Asfalto: 3.40 Terra.: 1.20
UNID. III -Asfalto: 55.40 Terra.: 1.20

COORDENADAS: E(X): 582.454,46 N(Y): 7.588.746,75
LAT: 21°48'11.3842" LONG: 50°12'8.2762"

CLEALCO - AÇÚCAR E ALCOOL S/A - DEPARTAMENTO DE TOPOGRAFIA

UNIDADE: II
PARTE: B/B
FUNDO AGRÍCOLA: 202517

M:\01-Mapa de safra\Mapas Atualizados\Clealco\202517 - Fazenda Boa Esperança III (Amélia Acerbi Jorge)\202517 B - Fazenda Boa Esperança III (Amélia Acerbi Jorge).dwg

Peterson Santos 07/11/2022