
Clealco
Açúcar, Etanol e Energia

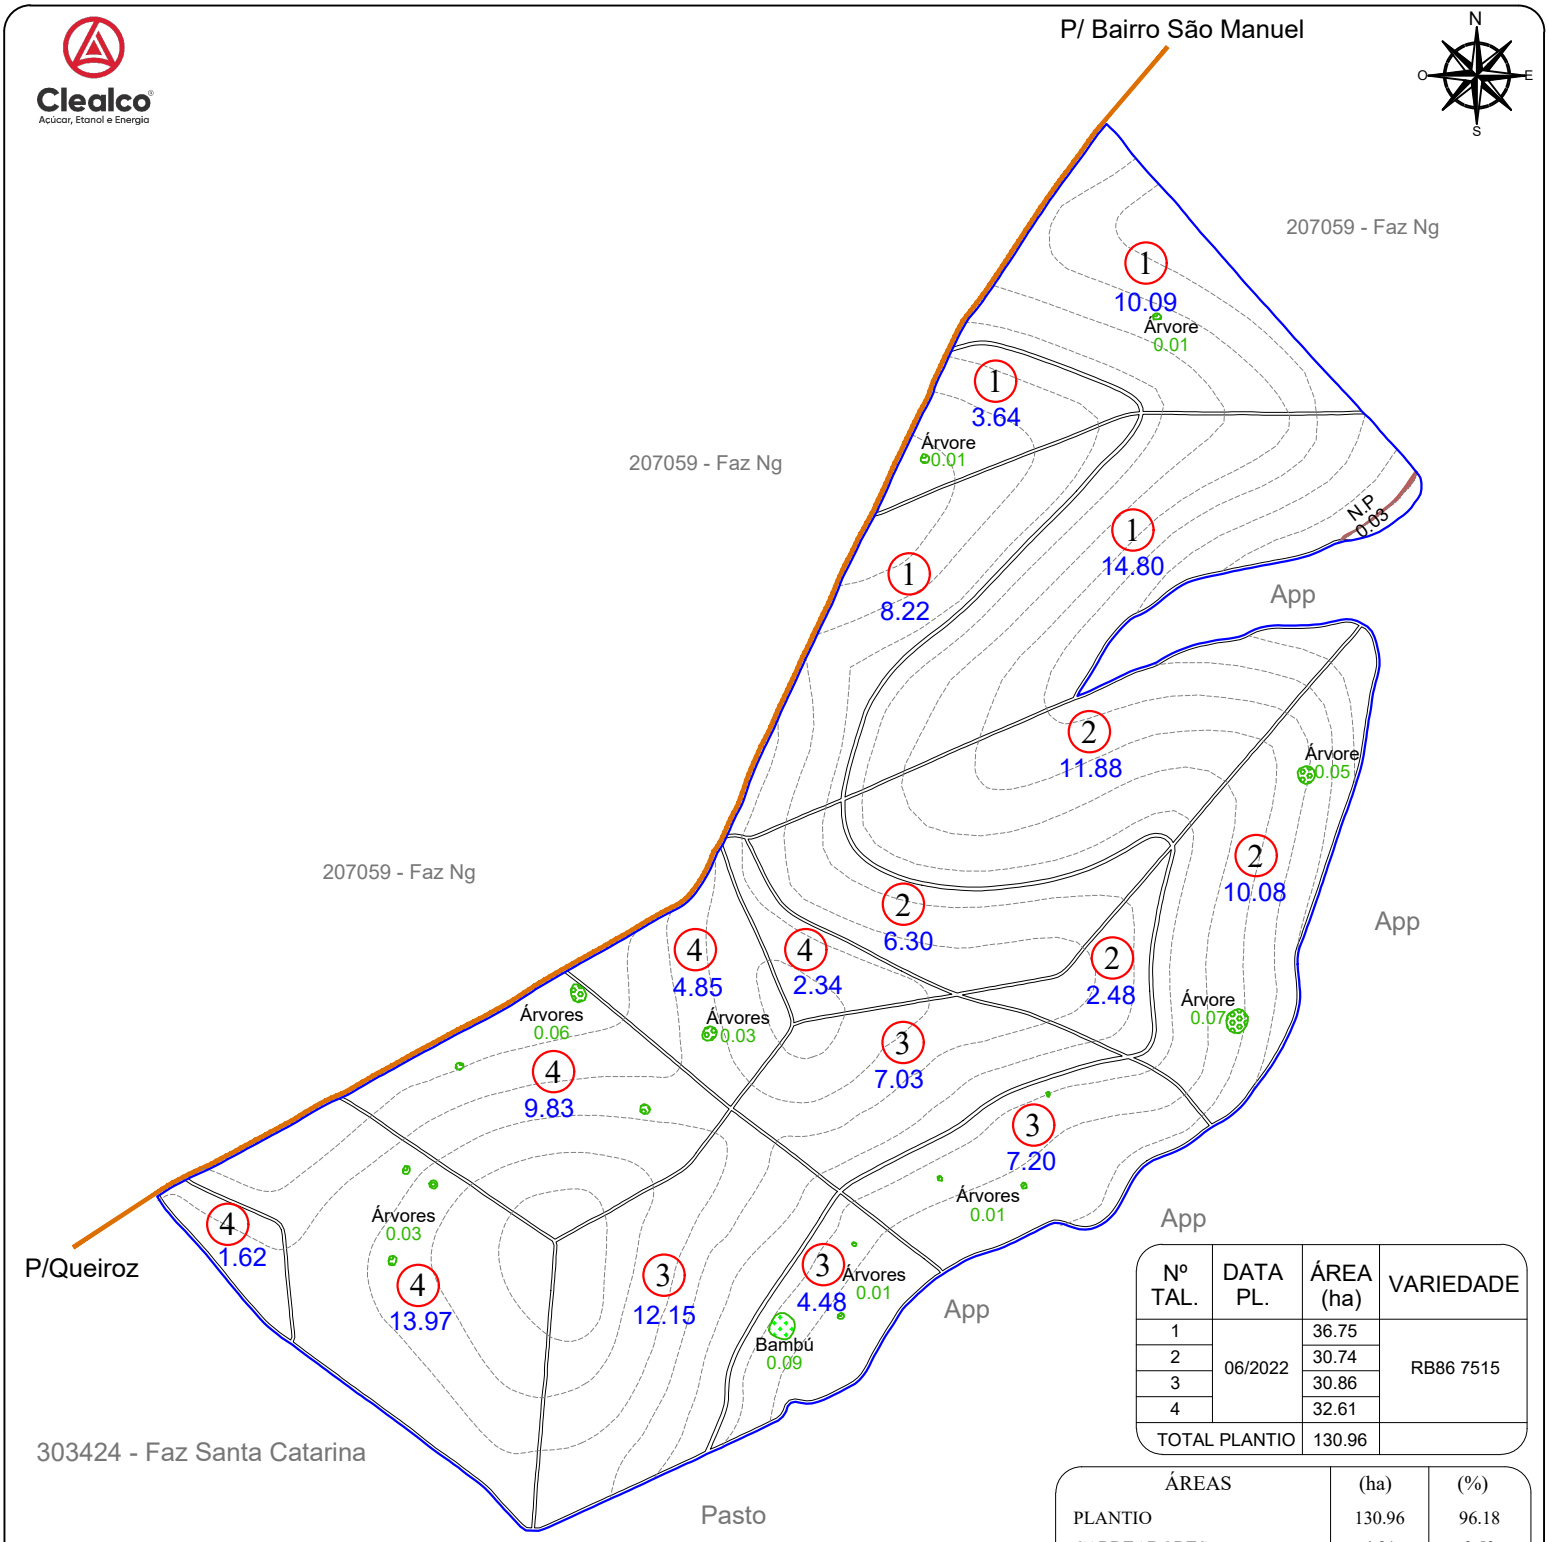

Nº TAL.	DATA PL.	ÁREA (ha)	VARIEDADE
1	06/2022	36.75	RB86 7515
2		30.74	
3		30.86	
4		32.61	
TOTAL PLANTIO		130.96	

ÁREAS	(ha)	(%)
PLANTIO	130.96	96.18
CARREADORES	4.81	3.53
OUTROS	0.03	0.02
SUB TOTAL AGRICULTÁVEL	135.80	99.73
AP.P.	0.00	0.00
ÁRVORES	0.37	0.27
OUTROS	0.00	0.00
SUB TOTAL NÃO AGRICULT.	0.37	0.27
ÁREA TOTAL	136.17	100.00

C. NÍVEL: 23307.33 m/l 5.36 ha 3.94 %


LEGENDA

- FAZENDA
- TALHÃO
- REDE ELÉTRICA
- VAZIO
- TERRAÇO BASE LARGA
- TERRAÇO EMBUTIDO
- (P.O.A) PATIO DE OPERAÇÃO
- CARREGADO

ESPAÇAMENTO: 1.50 x 1.50
TIRO MÉDIO ESTIMADO: 633.45 m
D.V: 5.39 %

ESCALA: 1: 10.500

CROQUI DE ACESSO

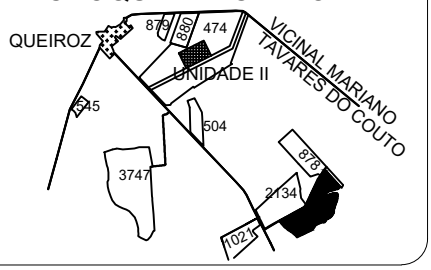

FAZENDA N.G.

PROPRIETÁRIO: JUCILEI MAGALHÃES RODRIGUES
COMPRADOR: CLEALCO
MUNICÍPIO: QUEIROZ - SP

DISTÂNCIAS (km):
UNID. I - Asfalto: 60.00 Terra.: 6.70
UNID.I I - Asfalto: 6.40 Terra.: 6.70

COORDENADAS: E(X): 584426.39 N(Y): 7584436.57
LAT: -21°50'31.2239" LONG: -50°10'58.8074"

CLEALCO - AÇÚCAR E ALCOOL S/A - DEPARTAMENTO DE GEOTECNOLOGIA

LEVANTAMENTO VIA:
- SATÉLITE
- GPS / VANT
- GOOGLE

UNIDADE: I
PARTE: A/A
FUNDO AGRÍCOLA: 202545

M:\01-Mapa de safra\Mapas Atualizados\Clealco\202545 - Fazenda Ng (Jucilei Magalhães Rodrigues)\202545 - Fazenda Ng Jucilei Magalhães Rodrigues).dwg

Peterson Santos 16/07/2026