
Clealco
Açúcar, Etanol e Energia

Nº TAL.	DATA PL.	ÁREA (ha)	VARIEDADE
1	2026	42.23	PLANTIO 2026
TOTAL PLANTIO		42.23	

ÁREAS	(ha)	(%)
PLANTIO	42.23	92.59
CARREADORES	2.24	4.91
OUTROS	0.00	0.00
SUB TOTAL AGRICULTÁVEL	44.47	97.50
AP.P.	0.00	0.00
MATA	0.04	0.09
OUTROS	1.10	2.41
SUB TOTAL NÃO AGRICULT.	1.14	2.50
ÁREA TOTAL	45.61	100.00

C. NÍVEL:	0.00 m/l	0.00 ha	0.00 %

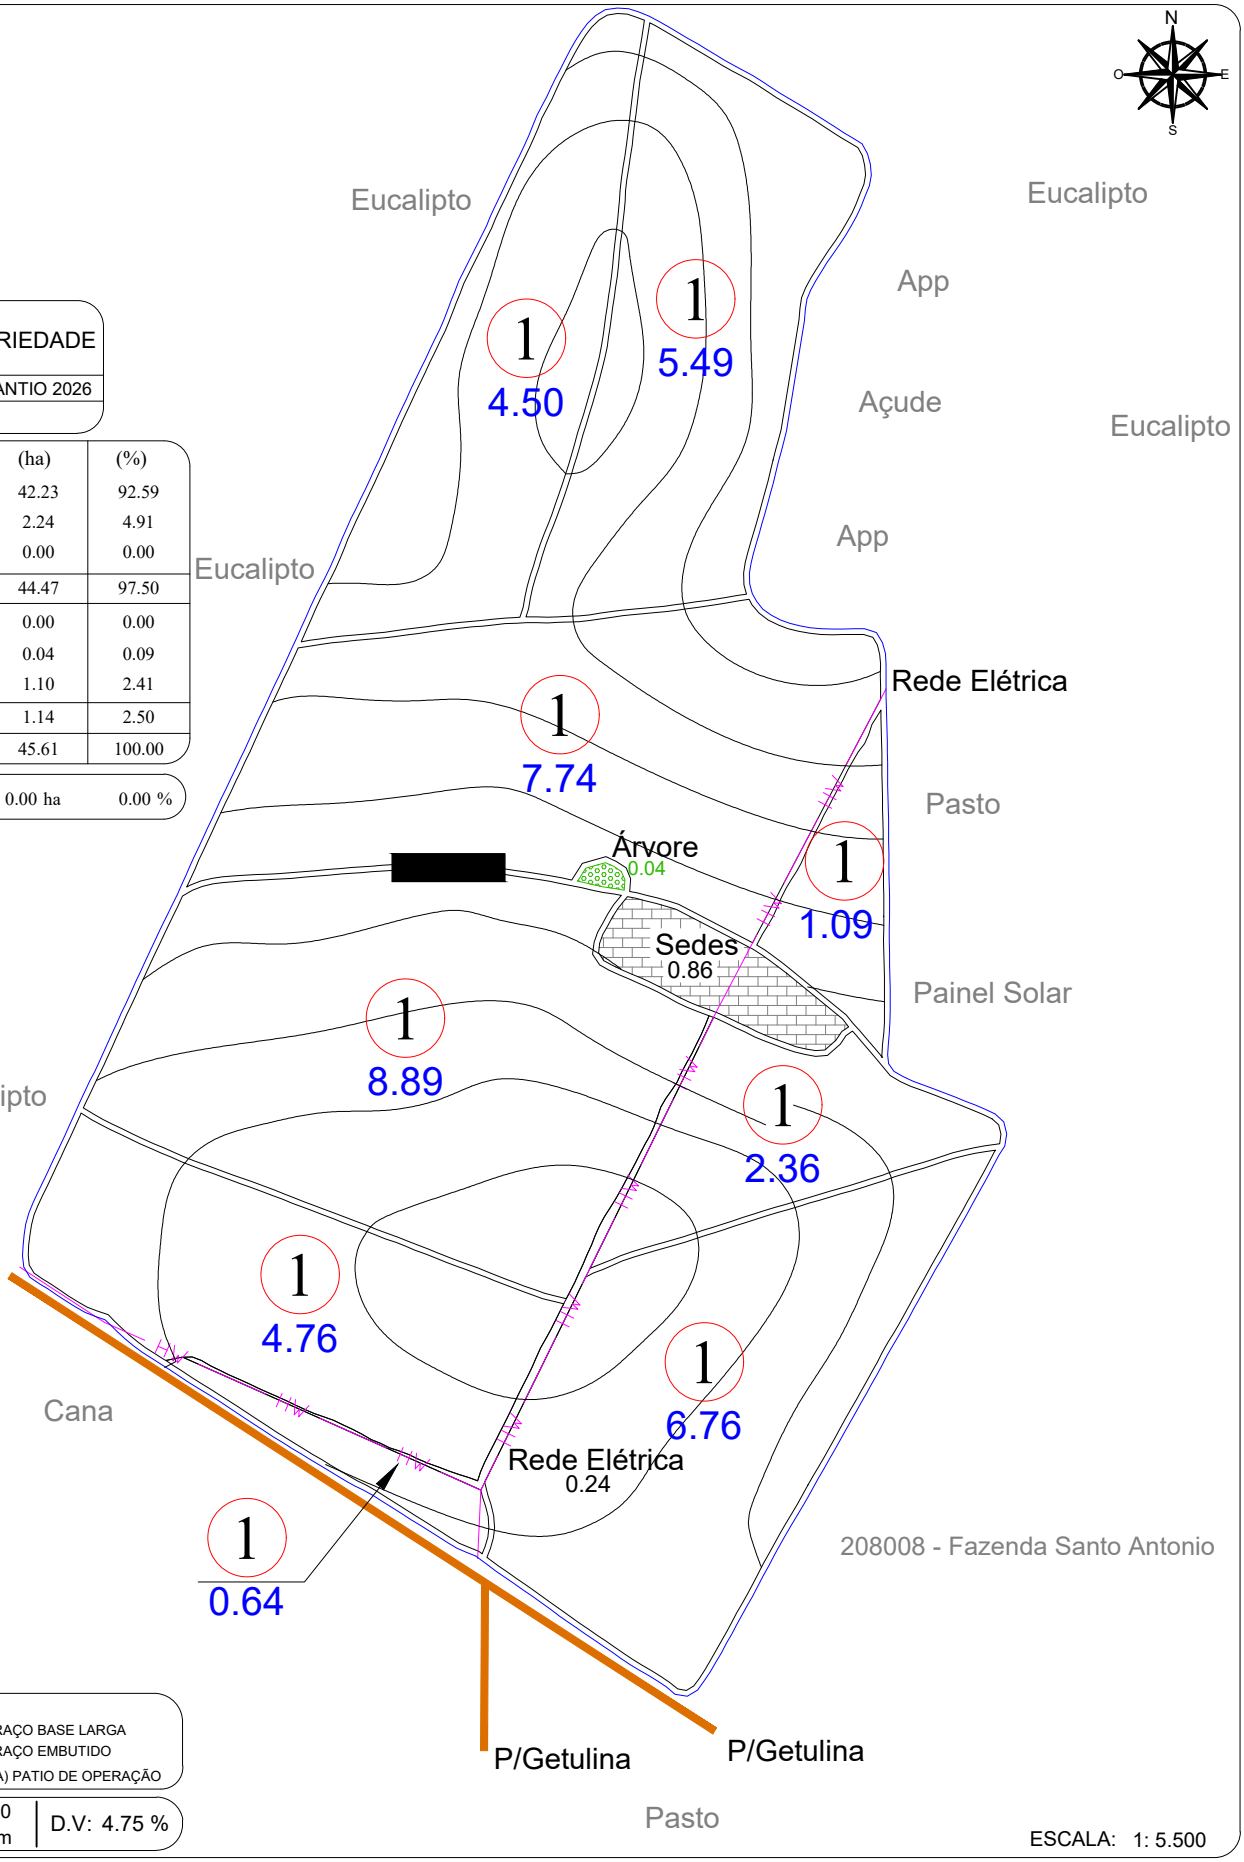


LEGENDA

- FAZENDA
- TALHÃO
- REDE ELÉTRICA
- TERRAÇO BASE LARGA
- TERRAÇO EMBUTIDO
- (P.O.A) PATIO DE OPERAÇÃO

ESPAÇAMENTO:	1.50 x 1.50	D.V: 4.75 %
TIRO MÉDIO ESTIMADO:	245.13 m	

ESCALA: 1: 5.500

CROQUI DE ACESSO

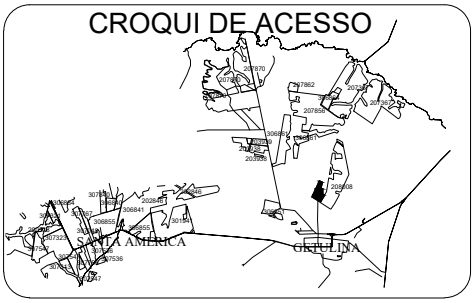

ESTÂNCIA SÃO FRANCISCO DE ASSIS

PROPRIETÁRIO: CLAUDEMIR SZAUTER E OUTRA
COMPRADOR: CLEALCO
MUNICÍPIO: GETULINA - SP

DISTÂNCIAS (km):
UNID. I - Asfalto: 91.10 Terra.: 5.00
UNID.I I - Asfalto: 38.50 Terra.: 5.00

COORDENADAS: E(X): 609847.62 N(Y): 7592052.69
LAT: -21°46'18.5044" LONG: -49°56'15.1295"

CLEALCO - AÇÚCAR E ALCOOL S/A - DEPARTAMENTO DE GEOTECNOLOGIA

LEVANTAMENTO VIA:
- SATÉLITE
- GPS / VANT
- GOOGLE

UNIDADE: II
PARTE: A/A
FUNDO AGRÍCOLA: 202582

M:\01-Mapa de safra\Mapas Atualizados\Clealco\202582 - Estância São Francisco de Assis (Claudemir Szauter e Outra)\202582 - Estância São Francisco de Assis (Claudemir Szauter e Outra).dwg

Bruno Gamboa 13/1025