DV	Nº TAL.	DATA PL.	ÁREA (ha)	VARIEDADE
4.65%	1	03/2022	30.85	RB 975242
	2		17.08	
TOTAL PLANTIO			47.93	--------

ÁREAS	(ha)	(%)
PLANTIO	47.93	92.63
CARREADORES	3.63	7.03
OUTROS	0.09	0.17
SUB TOTAL AGRICULTÁVEL	51.65	99.83
AP.P.	0.00	0.00
ÁRVORES	0.09	0.17
OUTROS	0.00	0.00
SUB TOTAL NÃO AGRICULT.	0.09	0.17
ÁREA TOTAL	51.74	100.00

C. NÍVEL:	5410.43 m/l	1.24 ha	2.40 %

LEGENDA

FAZENDA	CONFRONTANTE
TALHÃO	REDE ELÉTRICA
CURVA DE NÍVEL	TRAJETO VAZIO
CARREADOR	TRAJETO CARREGADO

PLANTIO MANUAL - ESPAÇAMENTO: 1.50 X 1.50
TIRO MÉDIO ESTIMADO: 243.96m

Clealco
Açúcar, Etanol e Energia

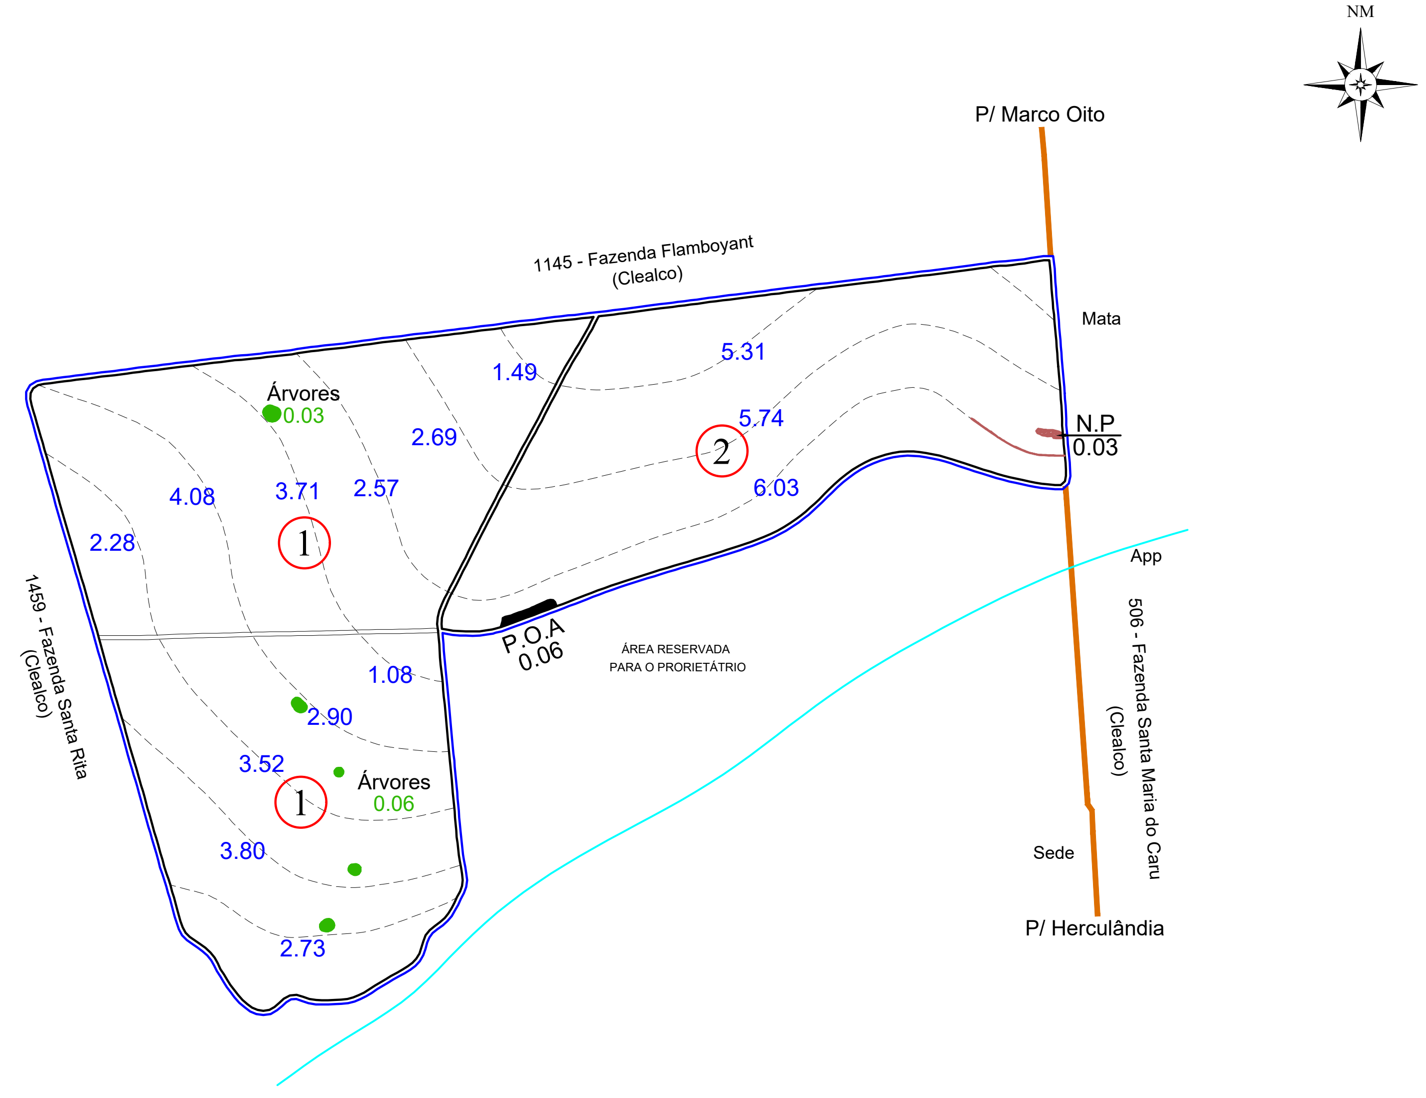
NM
P/ Marco Oito
1145 - Fazenda Flamboyant (Clealco)
Mata
N.P
0.03
1.49
5.31
5.74
2.69
2
6.03
Árvores
0.03
4.08
3.71
2.57
1
2.28
1459 - Fazenda Santa Rita (Clealco)
P.O.A
0.06
ÁREA RESERVADA PARA O PROIERTÁTRIO
App
506 - Fazenda Santa Maria do Caru (Clealco)
1.08
2.90
3.52
1
Árvores
0.06
3.80
2.73
Sede
P/ Herculândia

ESCALA: 1: 10.000

CROQUI DE ACESSO

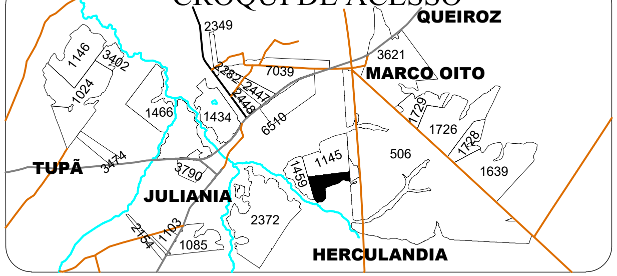

ESTÂNCIA SALVADOR

PROPRIETÁRIO:	EUNICE TAVARES SOLER
COMPRADOR:	CLEALCO S/A
MUNICÍPIO:	HERCULÂNDIA - SP

DISTÂNCIAS (km):

UNID. I -	Asfalto:	32.50	Terra.:	27.50
UNID.I I -	Asfalto:	17.00	Terra.:	4.30
UNID. III -	Asfalto:	70.00	Terra.:	4.30

COORDENADAS: E(X): 568502.30 N(Y): 7577454.25
LAT: -21°54'20.7966" LONG: -50°20'12.4801"

CLEALCO - AÇÚCAR E ALCOOL S/A - DEPARTAMENTO DE TOPOGRAFIA

UNIDADE:
II

PARTE:
A/A

FUNDO AGRÍCOLA:
202598

M:\01-Mapa de safra\Mapas Atualizados\Clealco\202598 - Estância Salvador (Eunice Tavares Soler)\202598 - Estância Salvador (Eunice Tavares Soler).dwg

Fernanda Bezerra 25/07/22