ZONA DV	Nº TAL.	DATA PL.	ÁREA (ha)	VARIEDADE
1 3.84 %	7	04/2021	40.05	RB 97 5242
	8		32.98	
	9		48.25	
	10		30.40	
	11		39.43	
	12		32.09	
	13		35.37	
TOTAL PLANTIO			258.57	--------

ÁREAS	(ha)	(%)
PLANTIO	258.57	92.89
CARREADORES	17.88	6.42
PÁTIO OPERAÇÕES AGRÍCOLAS	0.49	0.18
SUB TOTAL AGRICULTÁVEL	276.94	99.49
CURRAL	1.42	0.51
MATA	-	-
OUTROS	-	-
SUB TOTAL NÃO AGRICULT.	1.42	0.51
ÁREA TOTAL	278.36	100.00

C. NÍVE 34261.85 m/l 7.88 ha 2.83 %


LEGENDA

- FAZENDA
- TALHÃO
- CURVA DE NÍVEL
- CARREADOR
- CONFRONTANTE
- REDE ELÉTRICA
- TRAJETO VAZIO
- TRAJETO CARREGADO

PLANTIO MANUAL - ESPAÇAMENTO: 1.50 X 1.50

Clealco
Açúcar, Etanol e Energia


PÓS PLANTIO

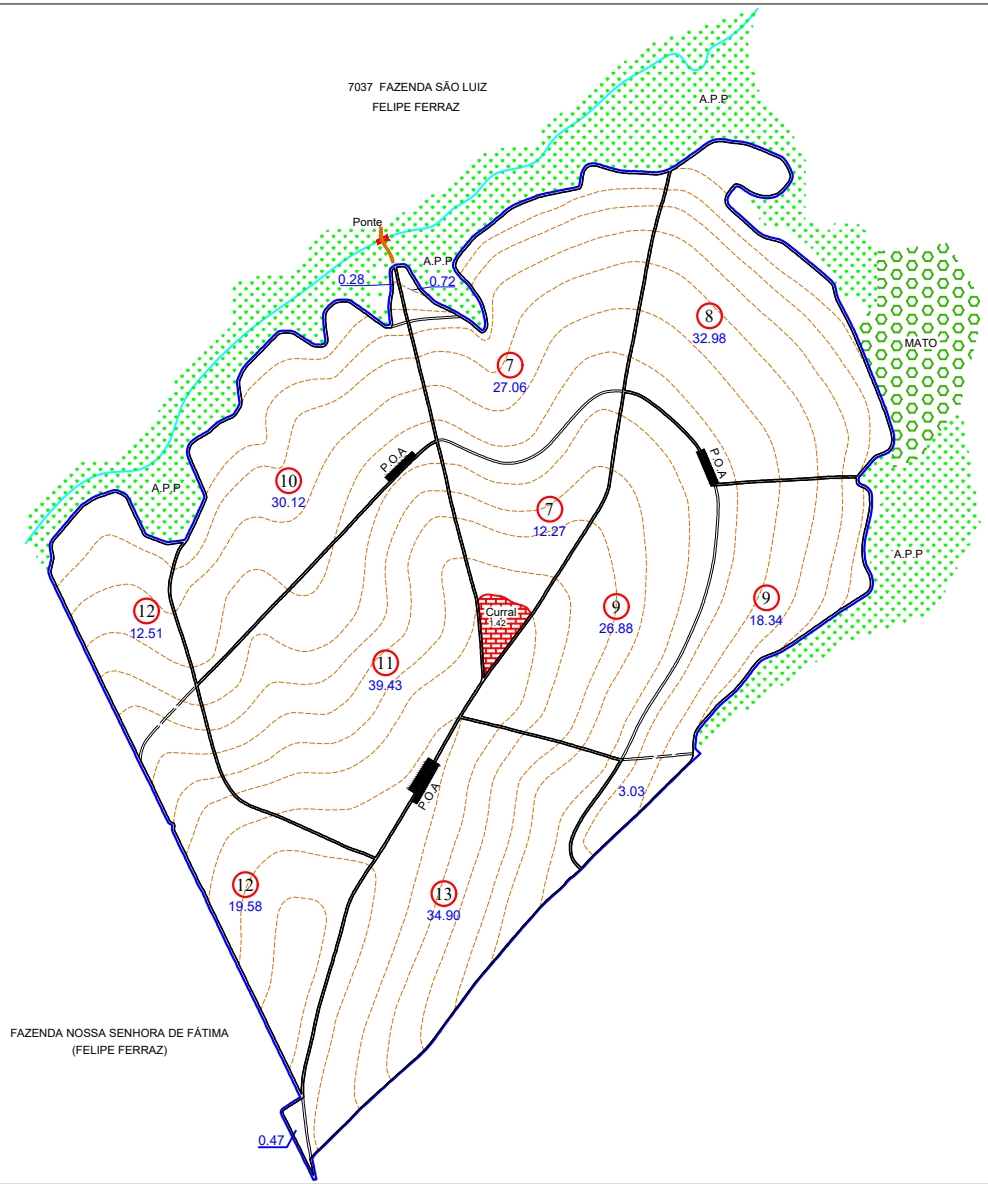

NM

ESCALA: 1: 18.000

CROQUI DE ACESSO

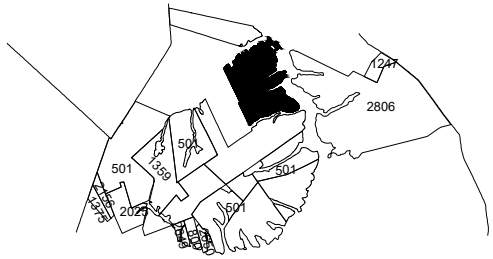

FAZENDA SÃO LUIZ

PROPRIETÁRIO: FERNANDO FERNANDES
ARRENDATÁRIO: CLEALCO S/A
MUNICÍPIO: QUEIROZ

DISTÂNCIAS (km):
UNID. I - Asfalto: 65.70 Terra.: 5.00
UNID.I I - Asfalto: 6.70 Terra.: 5.00
UNID. III -Asfalto: 62.70 Terra.: 5.00

COORDENADAS: E(X): 7577556 N(Y): 580892
LAT: 21º54'16" LONG: 50º13'10"

CLEALCO - AÇÚCAR E ALCOOL S/A - DEPARTAMENTO DE TOPOGRAFIA

UNIDADE: II

PARTE: A/B

FUNDO AGRÍCOLA: 202617

M:\01-Mapa de safra\Mapas Safra 2023 - PIMS\Clealco\202617 A -Fazenda São Luiz (Alice Cisneros Fernandes) - 2023.dwg