ZONA DV	Nº TAL.	DATA PL.	ÁREA (ha)	VARIEDADE
1 7.42 %	1	05/2021	7.51	SP 83 2847
	2		29.50	RB 86 7515
	3		23.26	
	4		29.27	
TOTAL PLANTIO			89.54	--------


ÁREAS	(ha)	(%)
PLANTIO	89.54	89.01
CARREADORES	8.87	8.82
NÃO PLANTOU	0.21	0.21
PÁTIO OPERAÇÕES AGRÍCOLAS	0.08	0.07
SUB TOTAL AGRICULTÁVEL	98.70	98.11
ÁRVORES	0.07	0.07
REDE ELÉTRICA	0.30	0.30
A.P.P	1.53	1.52
SUB TOTAL NÃO AGRICULT.	1.90	1.89
ÁREA TOTAL	100.60	100.00

C. NÍVE 8418.08 m/l 1.94 ha 1.92 %

LEGENDA

- FAZENDA
- TALHÃO
- CURVA DE NÍVEL
- CARREADOR
- CONFRONTANTE
- REDE ELÉTRICA
- TRAJETO VAZIO
- TRAJETO CARREGADO


PLANTIO MANUAL - ESPAÇAMENTO: 1.50 X 1.50

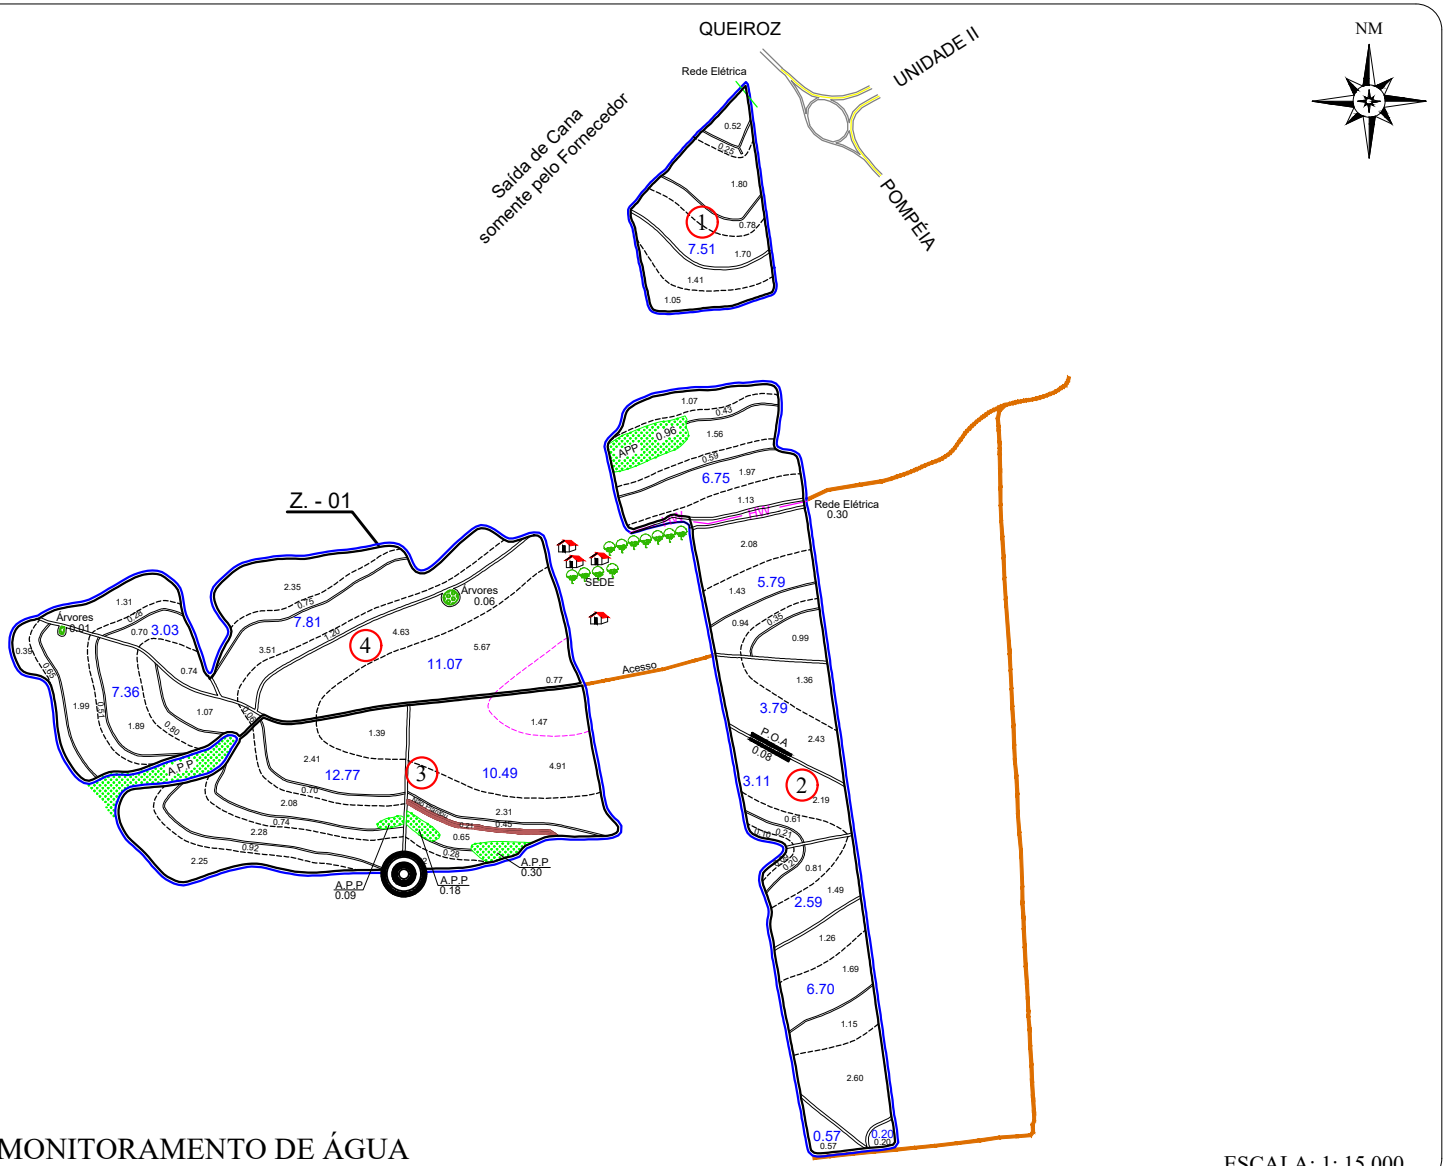

POÇO DE MONITORAMENTO DE ÁGUA

ESCALA: 1: 15.000

CROQUI DE ACESSO

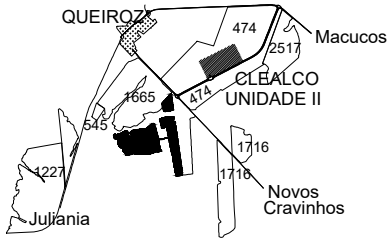

FAZENDA YPÊ

PROPRIETÁRIO: ALICE CISNEROS FERNANDES
ARRENDATÁRIO: CLEALCO S/A
MUNICÍPIO: QUEIROZ

DISTÂNCIAS (km):
UNID. I - Asfalto: 61.00 Terra.: 1.00
UNID.I I - Asfalto: 2.00 Terra.: 1.00
UNID. III -Asfalto: 58.50 Terra.: 1.00

COORDENADAS: E(X): 579038.619 N(Y): 7586514.562
LAT: 21º 49' 25" LONG: 50º 14' 07"

CLEALCO - AÇÚCAR E ALCOOL S/A - DEPARTAMENTO DE TOPOGRAFIA

UNIDADE: II

PARTE: A/A

FUNDO AGRÍCOLA: 202618

M:\01-Mapa de safra\Mapas Atualizados\Clealco\202618 - Fazenda Ypê (Alice Cisneros Fernandes)\202618 - Fazenda Ypê (Alice Cisneros Fernandes).dwg

Pedro Becker 12/07/21