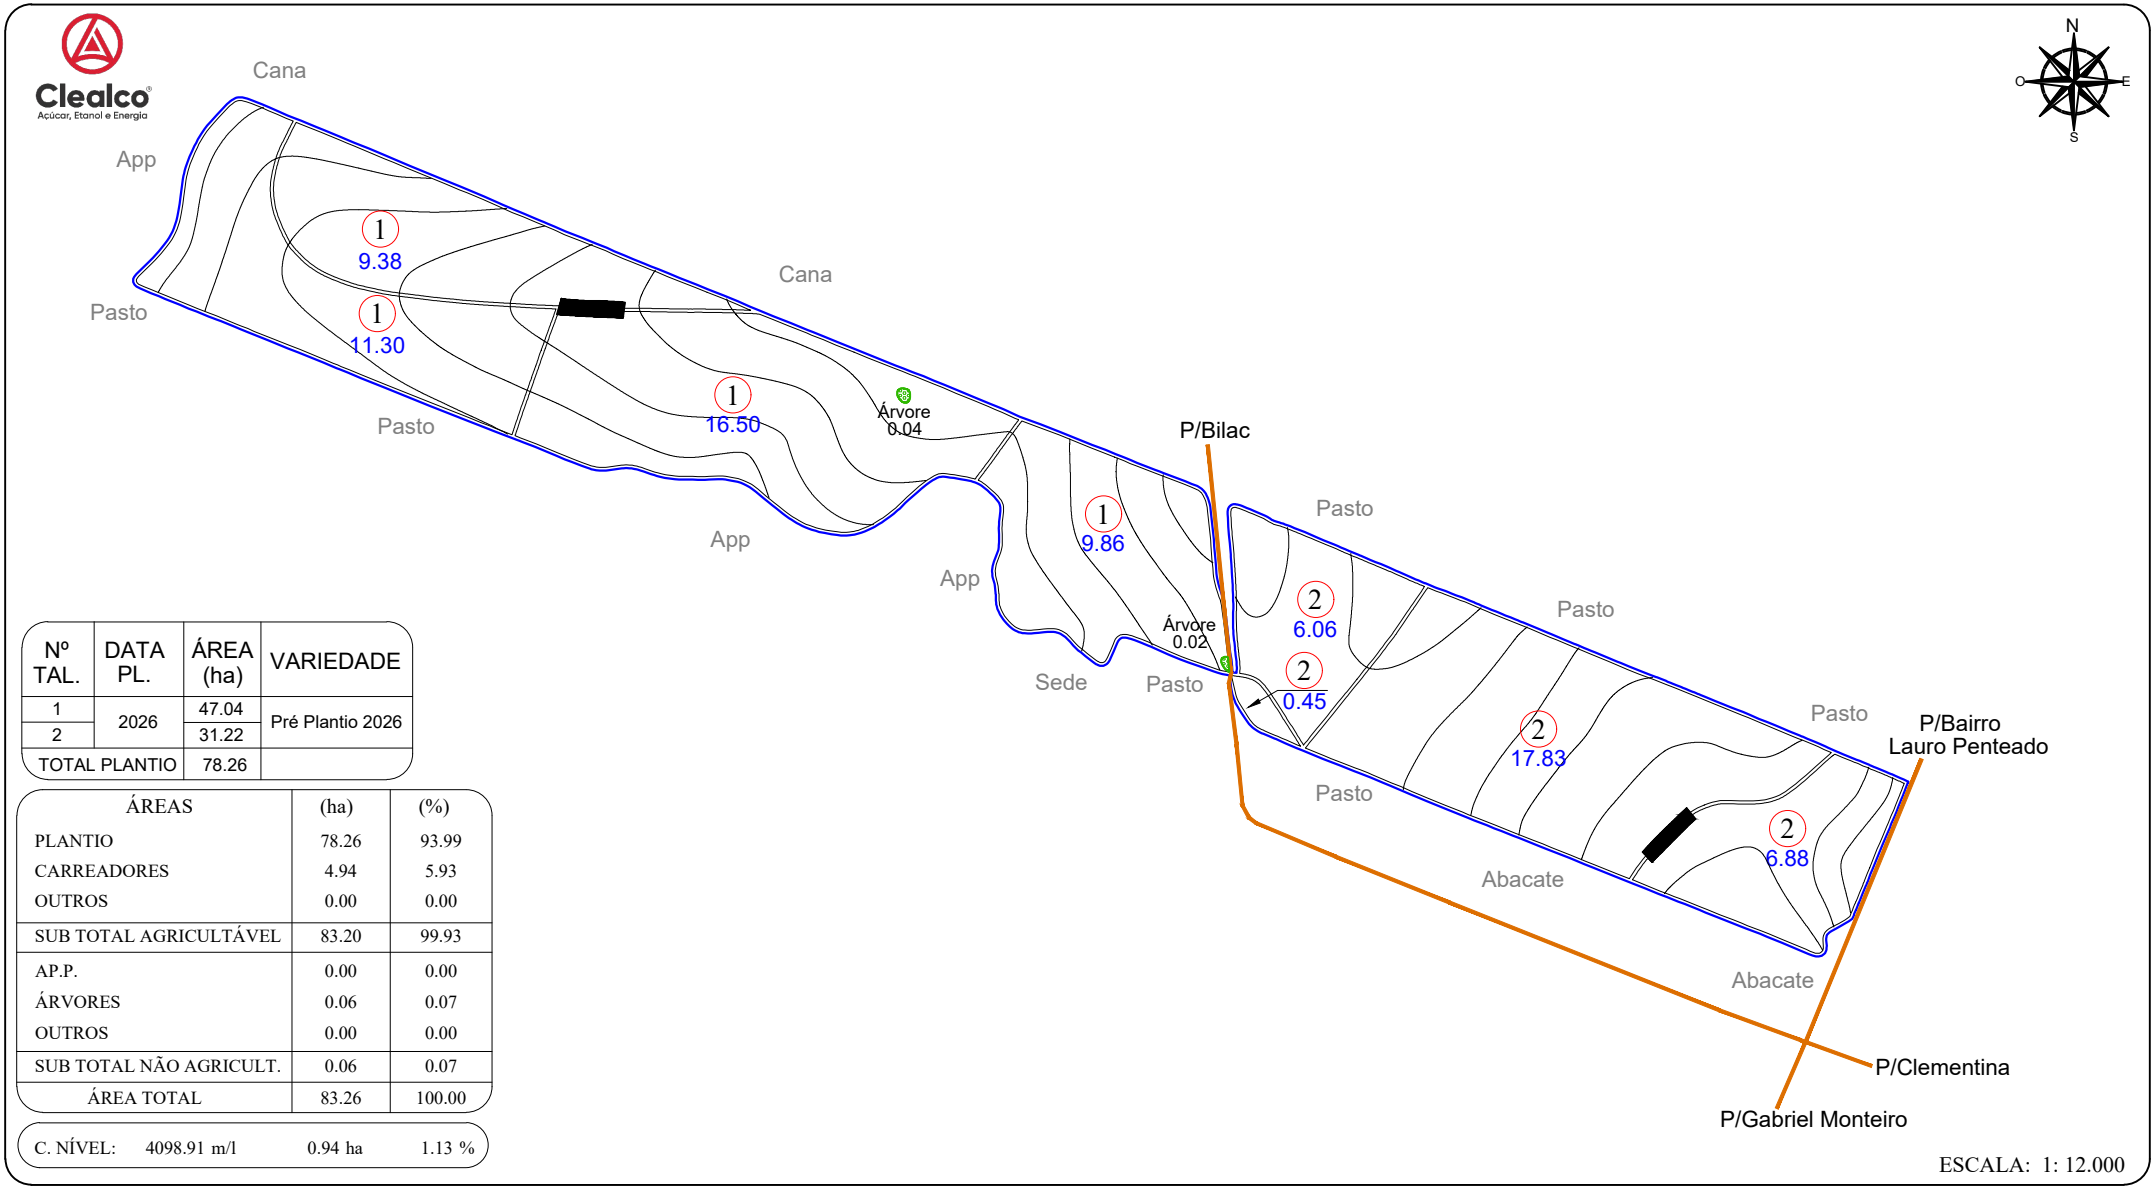


Nº TAL.	DATA PL.	ÁREA (ha)	VARIEDADE
1	2026	47.04	Pré Plantio 2026
2		31.22	
TOTAL PLANTIO		78.26	

ÁREAS	(ha)	(%)
PLANTIO	78.26	93.99
CARREADORES	4.94	5.93
OUTROS	0.00	0.00
SUB TOTAL AGRICULTÁVEL	83.20	99.93
AP.P.	0.00	0.00
ÁRVORES	0.06	0.07
OUTROS	0.00	0.00
SUB TOTAL NÃO AGRICULT.	0.06	0.07
ÁREA TOTAL	83.26	100.00

C. NÍVEL: 4098.91 m/l 0.94 ha 1.13 %


ESCALA: 1: 12.000

LEGENDA

- FAZENDA
- TALHÃO
- REDE ELÉTRICA
- TERRAÇO BASE LARGA
- TERRAÇO EMBUTIDO
- VAZIO
- CARREGADO

ESPAÇAMENTO: 1.50 x 1.50
TIRO MÉDIO ESTIMADO: 257.64 m
D.V: 4.84 %

CROQUI DE ACESSO

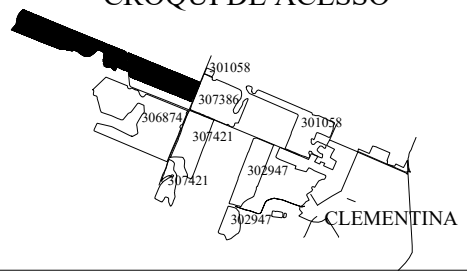

SÍTIO SÃO LUIZ III

PROPRIETÁRIO: SUMIE YDA
COMPRADOR: CLEALCO
MUNICÍPIO: CLEMENTINA - SP

DISTÂNCIAS (km):
UNID. I - Asfalto: 4.00 Terra.: 3.00
UNID.I I - Asfalto: 51.00 Terra.: 4.70

COORDENADAS: E(X): 553122.26 N(Y): 7618072.82
LAT: -21°32'21.6269" LONG: -50°29'13.1953"

CLEALCO - AÇÚCAR E ALCOOL S/A - DEPARTAMENTO DE GEOTECNOLOGIA

LEVANTAMENTO VIA:
SATÉLITE
GPS / VANT
GOOGLE

UNIDADE: I
PARTE: A/A
FUNDO AGRÍCOLA: 202714

M:\01-Mapa de safra\Mapas Atualizados\Clealco\202714 - Sítio São Luiz III (Sumie Yda)\202714 - Sítio São Luiz III (Sumie Yda).dwg

Peterson Santos 05/05/2026