
Clealco
Açúcar, Etanol e Energia

ÁREAS	(ha)	(%)
PLANTIO	531.61	87.44
CARREADORES	47.10	7.75
OUTROS	0.00	0.00
SUB TOTAL AGRICULTÁVEL	578.71	95.19
AP.P.	26.47	4.35
ÁRVORES	1.33	0.22
OUTROS	1.46	0.24
SUB TOTAL NÃO AGRICULT.	29.26	4.81
ÁREA TOTAL	607.97	100.00

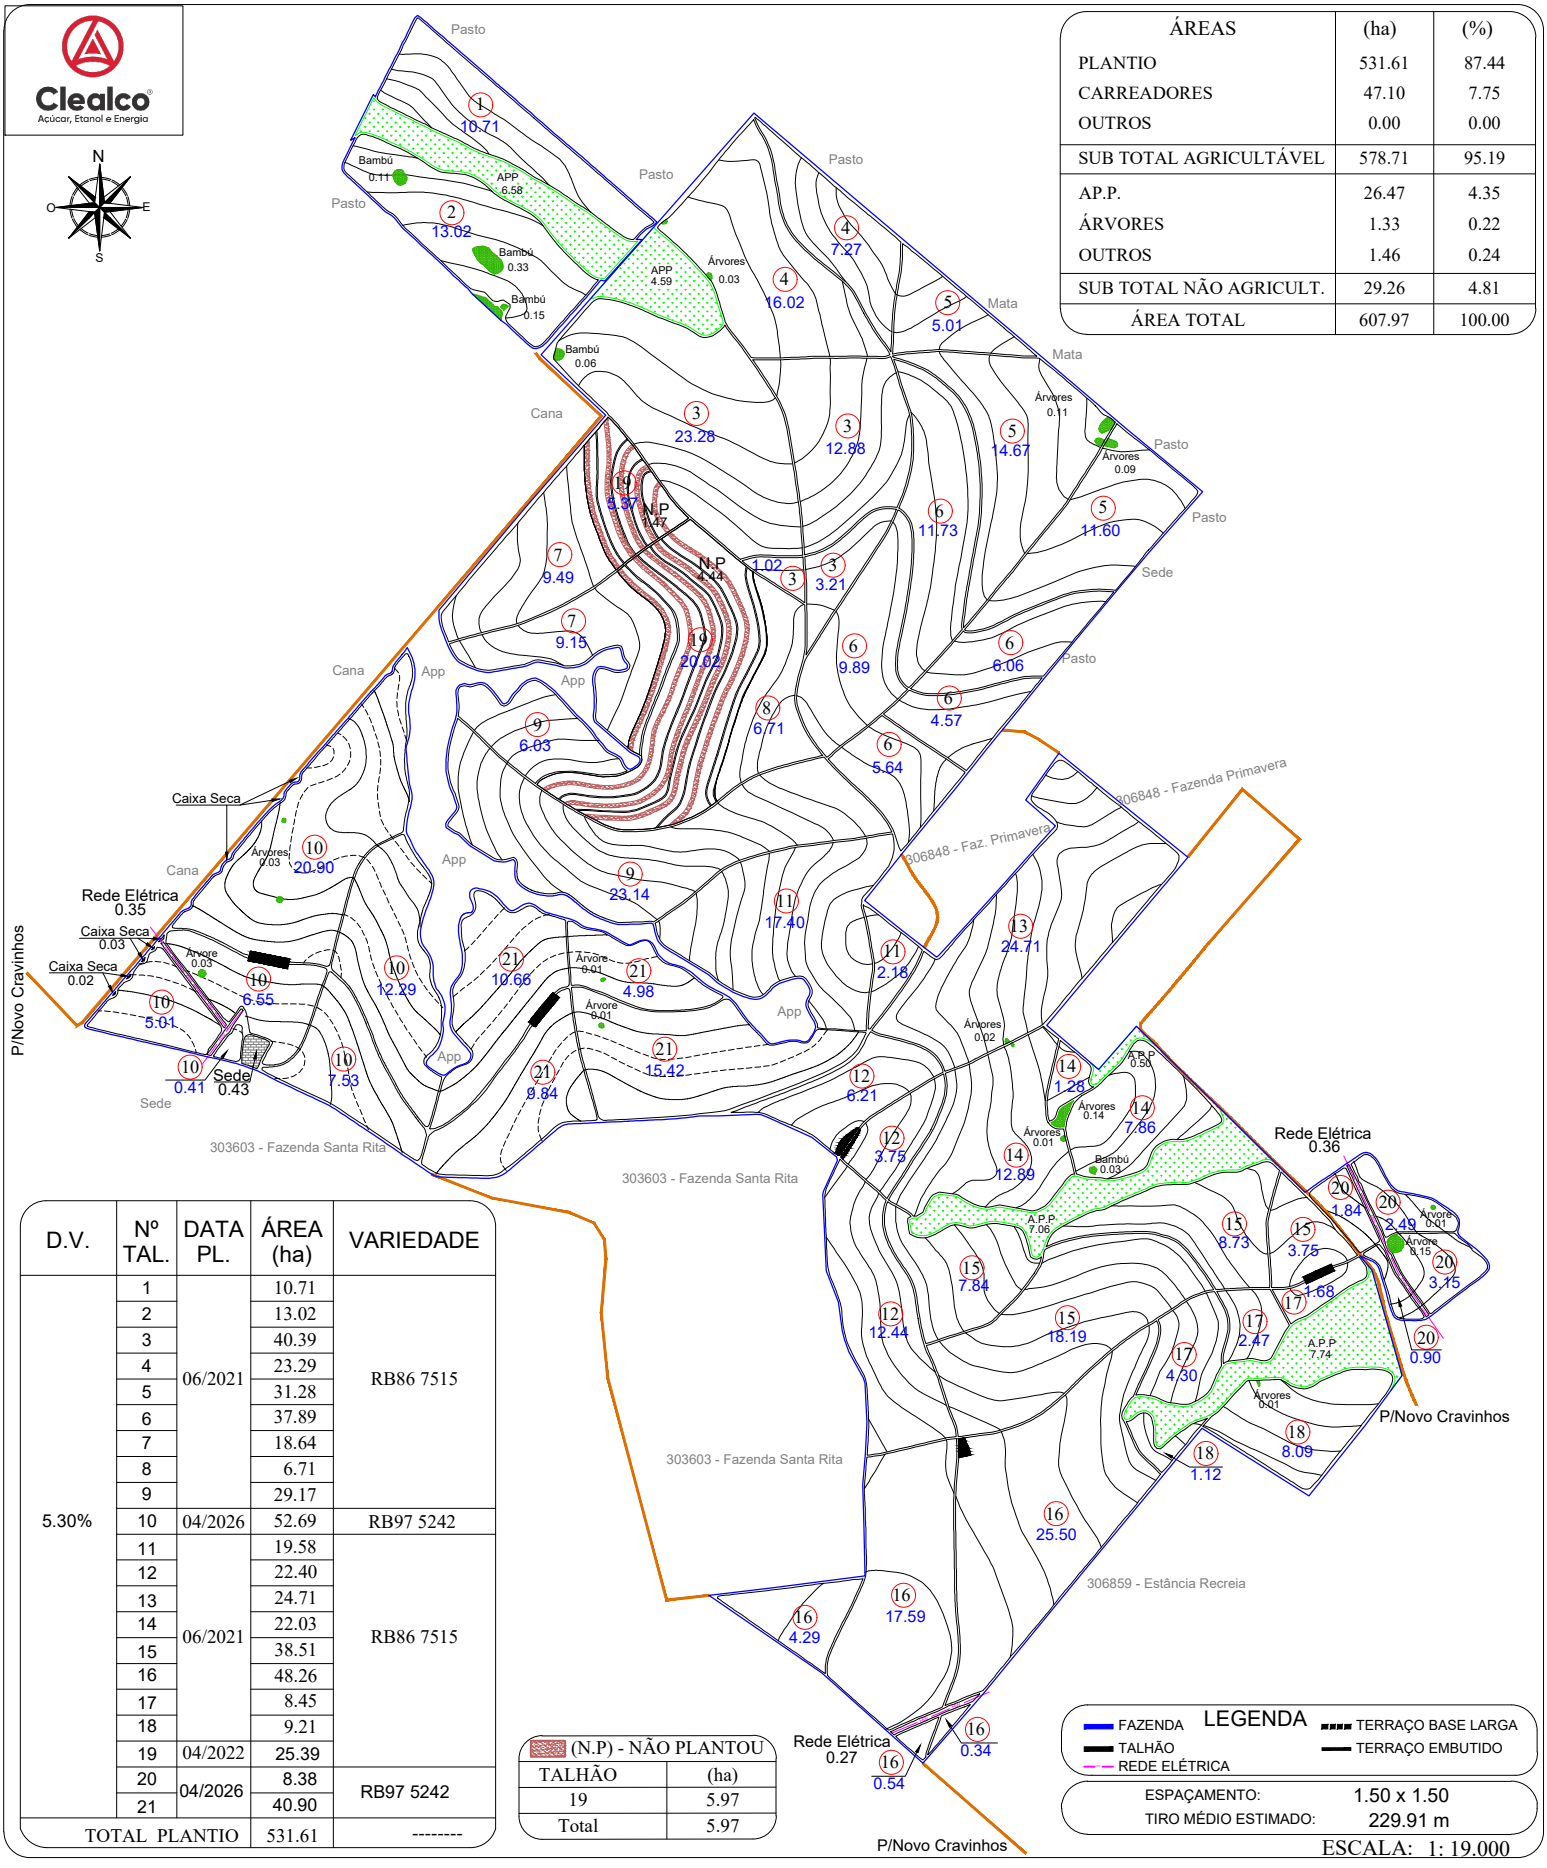

D.V.	Nº TAL.	DATA PL.	ÁREA (ha)	VARIEDADE
5.30%	1	06/2021	10.71	RB86 7515
	2		13.02	
	3		40.39	
	4		23.29	
	5		31.28	
	6		37.89	
	7		18.64	
	8		6.71	
	9		29.17	
	10	04/2026	52.69	RB97 5242
	11	06/2021	19.58	RB86 7515
	12		22.40	
	13		24.71	
	14		22.03	
	15		38.51	
	16		48.26	
	17		8.45	
	18		9.21	
	19	04/2022	25.39	
	20	04/2026	8.38	RB97 5242
	21		40.90	
TOTAL PLANTIO			531.61	--------


(N.P) - NÃO PLANTOU	
TALHÃO	(ha)
19	5.97
Total	5.97

LEGENDA
FAZENDA
TALHÃO
REDE ELÉTRICA
TERRAÇO BASE LARGA
TERRAÇO EMBUTIDO

ESPAÇAMENTO: 1.50 x 1.50
TIRO MÉDIO ESTIMADO: 229.91 m

ESCALA: 1: 19.000

CROQUI DE ACESSO

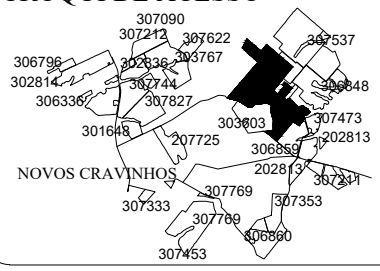

FAZENDA SÃO JOSÉ

PROPRIETÁRIO: COLPAR PARTICIPAÇÕES S/A
COMPRADOR: CLEALCO S/A
MUNICÍPIO: MARÍLIA

DISTÂNCIAS (km):
UNID. I - Asfalto: 77.30 Terra.: 8.80
UNID.I I - Asfalto: 22.60 Terra.: 8.80
UNID. III -Asfalto: 78.60 Terra.: 8.80

COORDENADAS: E(X): 595460.07 N(Y): 7574336.08
LAT: -21°55'57.6699" LONG: -50°4'32.3430"
CLEALCO - AÇÚCAR E ALCOOL S/A - DEPARTAMENTO DE GEOTECNOLOGIA

LEVANTAMENTO VIA:
SATÉLITE
GPS / VANT
GOOGLE

UNIDADE: II
PARTE: A/A
FUNDO AGRÍCOLA: 202807

M:\01-Mapa de safra\Mapas Atualizados\Clealco\202807 - Fazenda São José (Colpar Participações)\202807 Fazenda São José (Colpar Participações).dwg

Bruno Gamboa 11/09/26