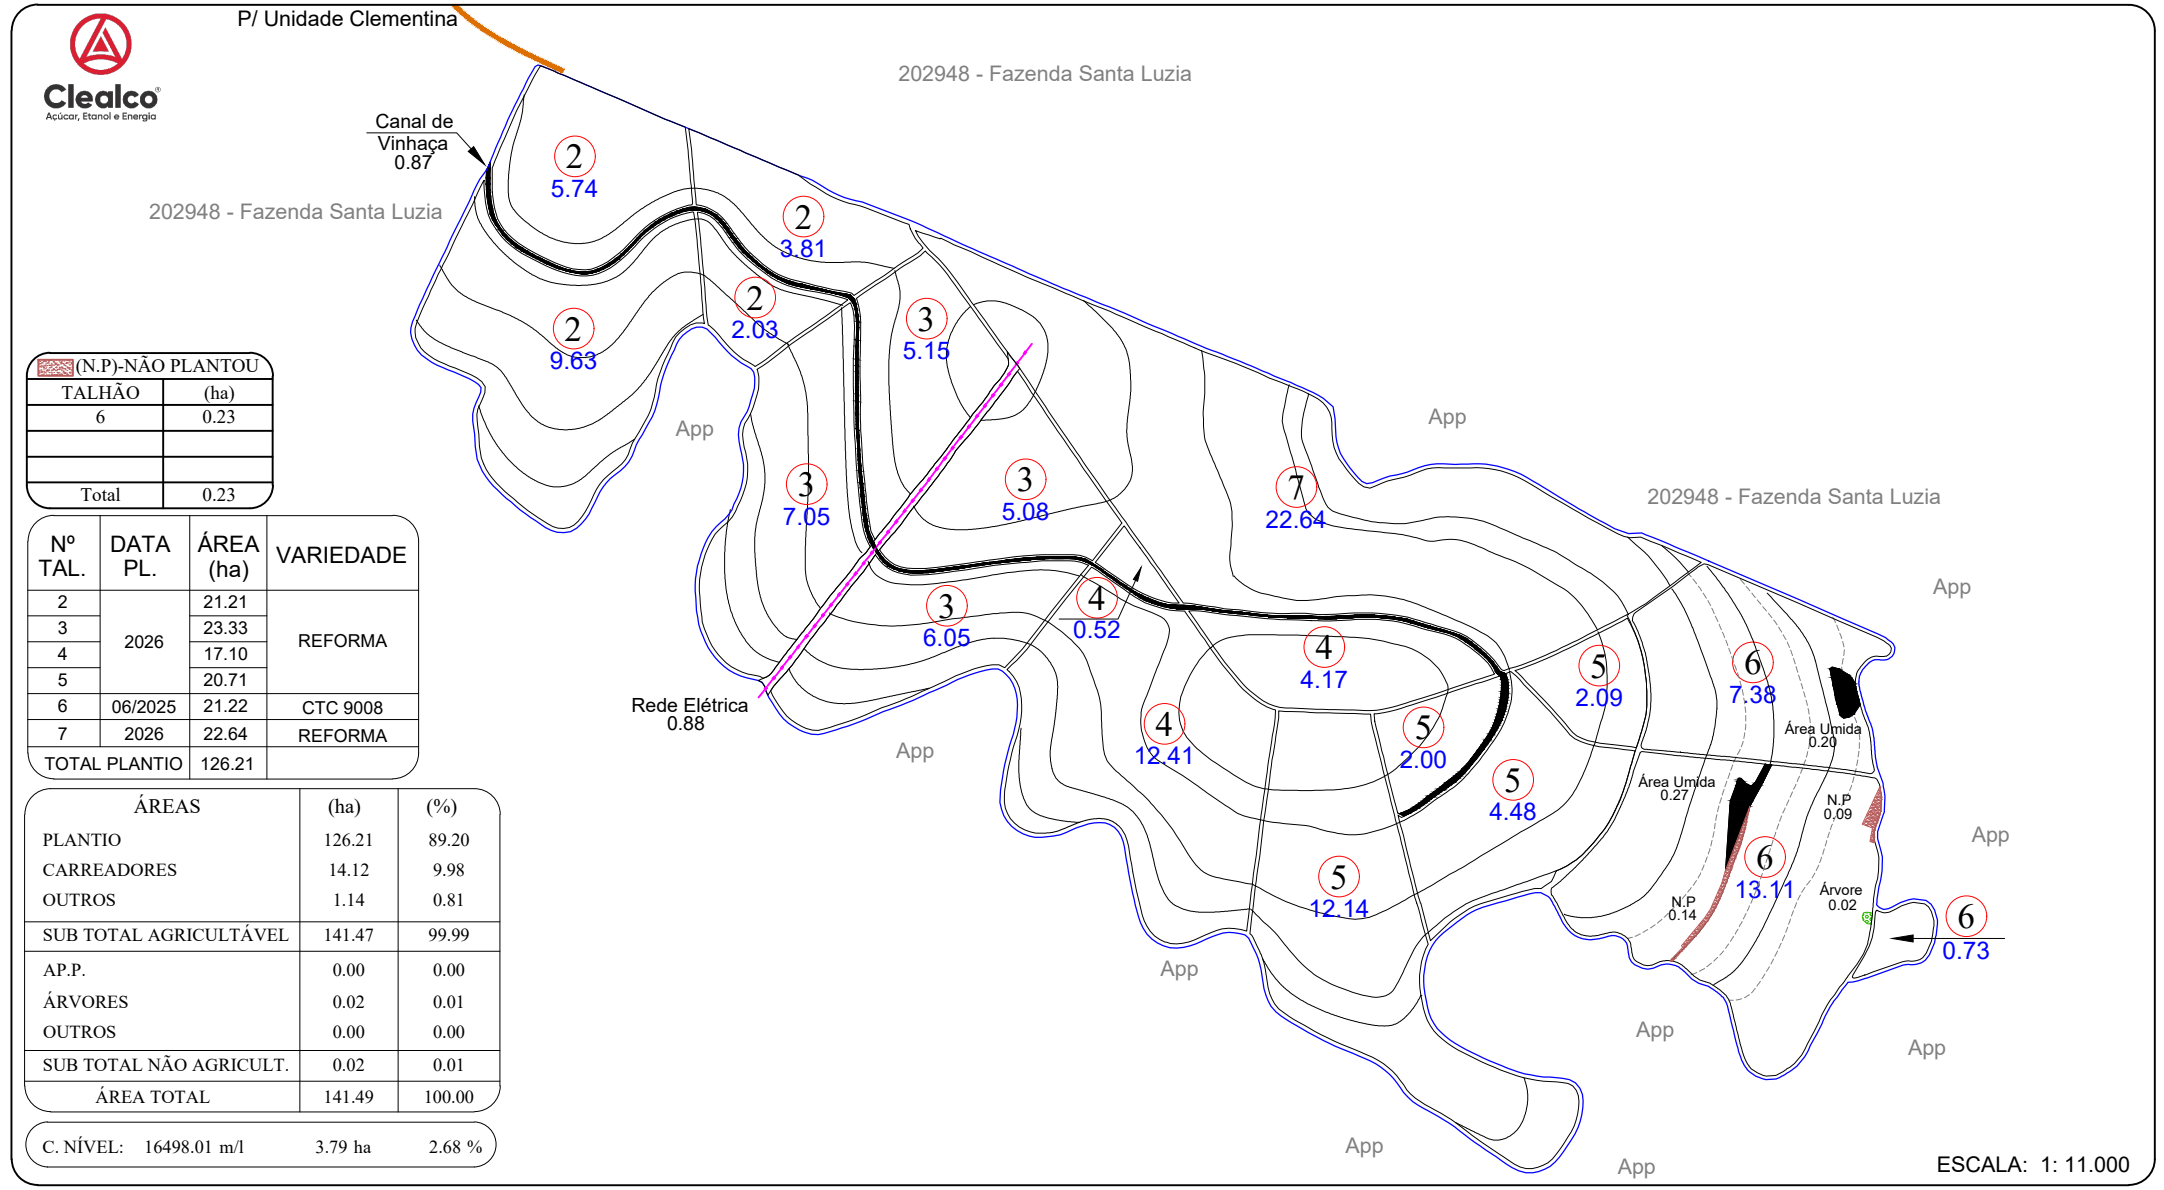


(N.P)-NÃO PLANTOU	
TALHÃO	(ha)
6	0.23
Total	0.23

Nº TAL.	DATA PL.	ÁREA (ha)	VARIEDADE
2	2026	21.21	REFORMA
3		23.33	
4		17.10	
5		20.71	
6	06/2025	21.22	CTC 9008
7	2026	22.64	REFORMA
TOTAL PLANTIO		126.21	

ÁREAS	(ha)	(%)
PLANTIO	126.21	89.20
CARREADORES	14.12	9.98
OUTROS	1.14	0.81
SUB TOTAL AGRICULTÁVEL	141.47	99.99
AP.P.	0.00	0.00
ÁRVORES	0.02	0.01
OUTROS	0.00	0.00
SUB TOTAL NÃO AGRICULT.	0.02	0.01
ÁREA TOTAL	141.49	100.00


C. NÍVEL:	16498.01 m/l	3.79 ha	2.68 %

LEGENDA

- FAZENDA
- TALHÃO
- REDE ELÉTRICA
- TERRAÇO BASE LARGA
- TERRAÇO EMBUTIDO

ESPAÇAMENTO: 1.50 x 1.50
TIRO MÉDIO ESTIMADO: 000.00 m
D.V: 5.76 %

CROQUI DE ACESSO

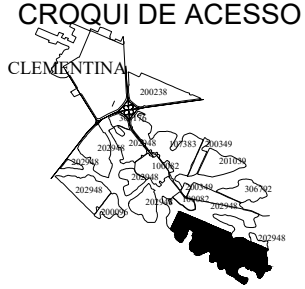

FAZENDA CALIFORNIA

PROPRIETÁRIO: ILHA AZUL EMPREENDIMENTOS
COMPRADOR: CLEALCO
MUNICÍPIO: CLEMENTINA - SP

DISTÂNCIAS (km):
UNID. I - Asfalto: 00.00 Terra.: 03.55
UNID.I I - Asfalto: 30.00 Terra.: 17.80

COORDENADAS: E(X): 560360.93 N(Y): 7611691.46
LAT: -21°35'48.3505" LONG: -50°25'0.7210"
CLEALCO - AÇÚCAR E ALCOOL S/A - DEPARTAMENTO DE GEOTECNOLOGIA

LEVANTAMENTO VIA:
- SATÉLITE
- GPS / VANT
- GOOGLE

UNIDADE: I
PARTE: B/B
FUNDO AGRÍCOLA: 202957

M:\01-Mapa de safra\Mapas Atualizados\Clealco\202957 - Fazenda California VII (Ilha Azul Empreendimentos e Participações)\202957 B - Fazenda California VII (Ilha Azul Empreendimentos e Participações).dwg

Bruno Gamboa 09/12/25