
Clealco
Açúcar, Etanol e Energia

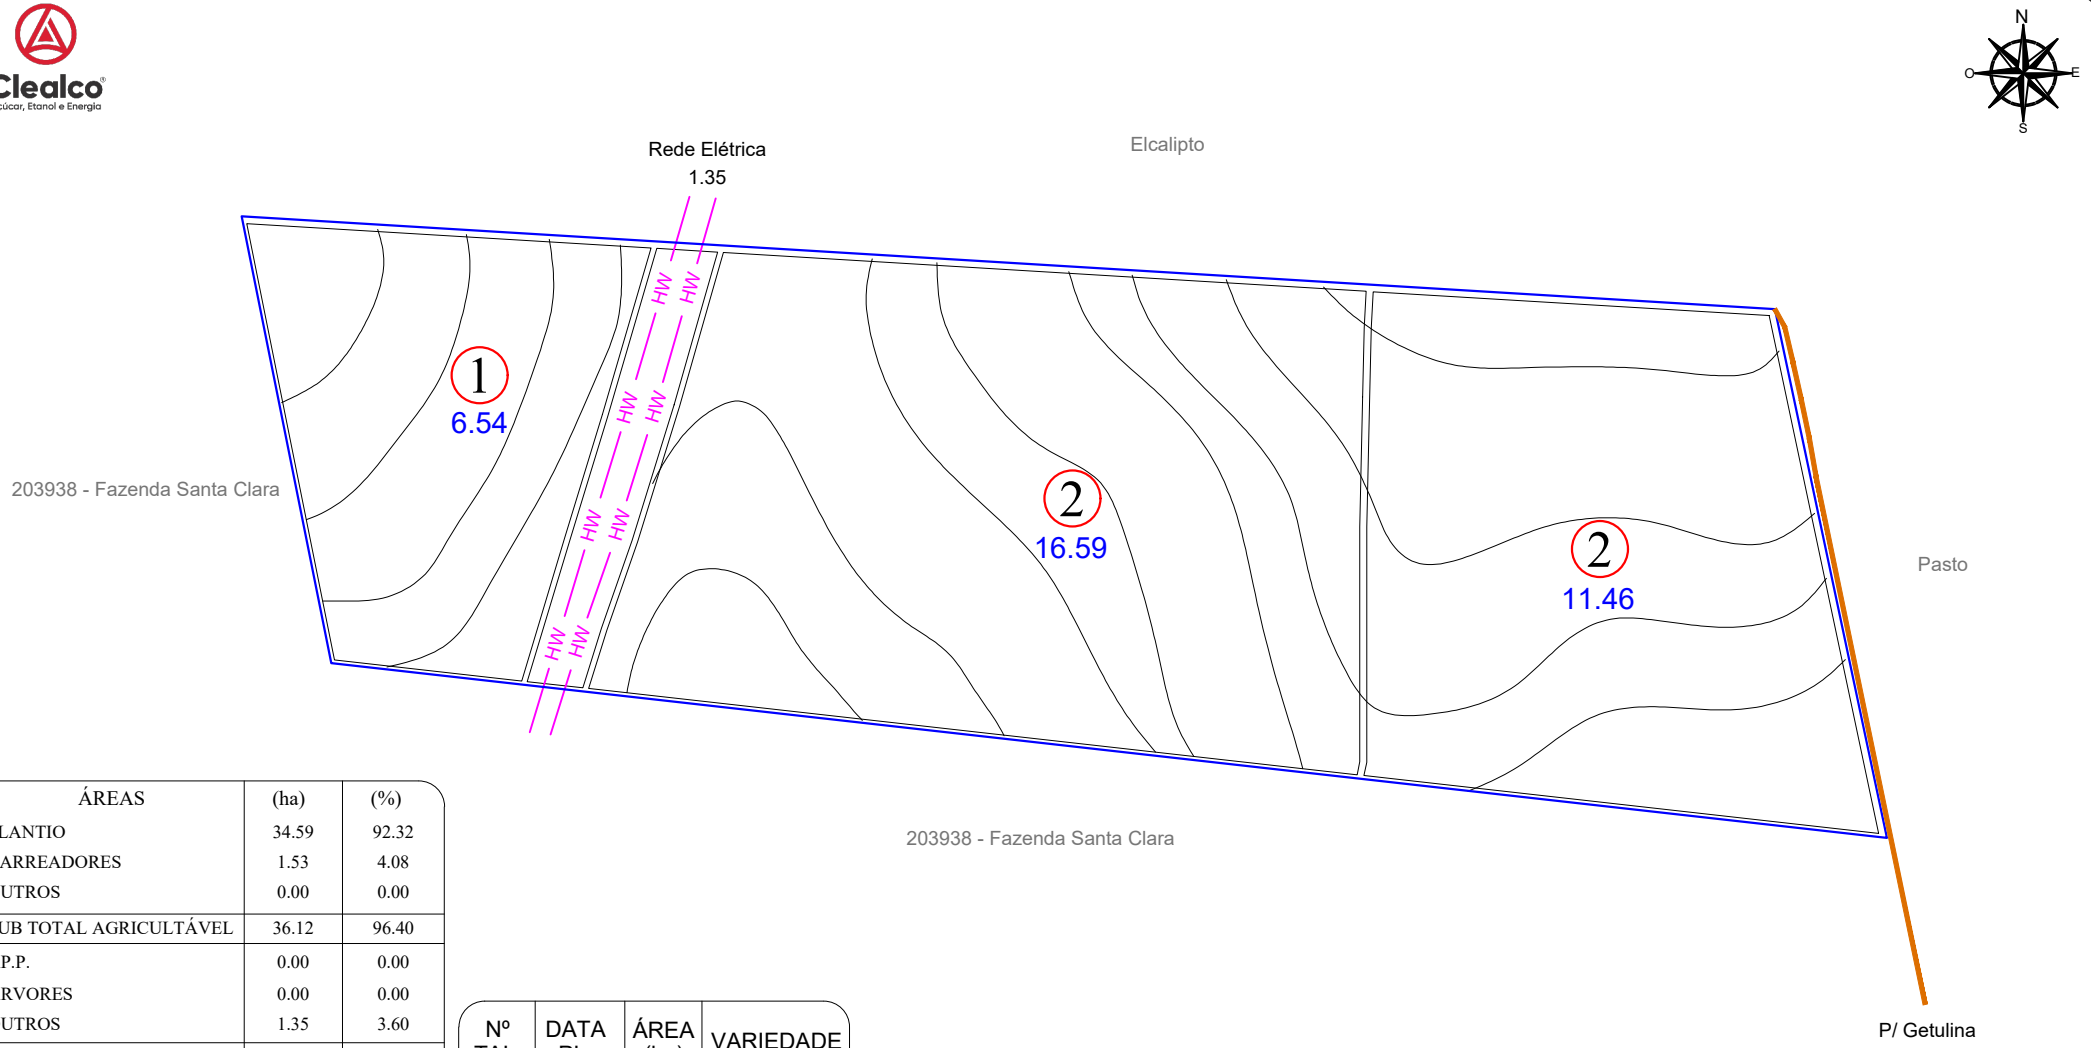

ÁREAS	(ha)	(%)
PLANTIO	34.59	92.32
CARREADORES	1.53	4.08
OUTROS	0.00	0.00
SUB TOTAL AGRICULTÁVEL	36.12	96.40
AP.P.	0.00	0.00
ÁRVORES	0.00	0.00
OUTROS	1.35	3.60
SUB TOTAL NÃO AGRICULT.	1.35	3.60
ÁREA TOTAL	37.47	100.00

C. NÍVEL:	4912.88 m/l	1.13 ha	3.02 %


Nº TAL.	DATA PL.	ÁREA (ha)	VARIEDADE
1	04/2024	6.54	RB86 7515
2		28.05	
TOTAL PLANTIO		34.59	

ESCALA: 1: 5.500

LEGENDA
- FAZENDA
- TALHÃO
- REDE ELÉTRICA
- TERRAÇO BASE LARGA
- TERRAÇO EMBUTIDO
- VAZIO
- CARREGADO

ESPAÇAMENTO: 1.50 x 1.50
TIRO MÉDIO ESTIMADO: 207.97 m
D.V: 6.18%

CROQUI DE ACESSO

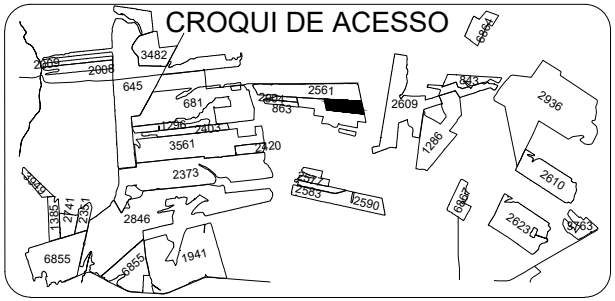

SÍTIO SÃO DOMINGOS

PROPRIETÁRIO: DANIEL VILELA
COMPRADOR: CLEALCO
MUNICÍPIO: GETULINA- SP

DISTÂNCIAS (km):
UNID. I - Asfalto: 66.50 Terra.:15.00
UNID.I I - Asfalto: 38.00 Terra.: 9.00

COORDENADAS: E(X): 606467.41 N(Y): 7594783.61
LAT: -21°44'50.4392" LONG: -49°58'13.4463"
CLEALCO - AÇÚCAR E ALCOOL S/A - DEPARTAMENTO DE GEOTECNOLOGIA

LEVANTAMENTO VIA:
- SATÉLITE
- GPS / VANT
- GOOGLE

UNIDADE: II
PARTE: A/A
FUNDO AGRÍCOLA: 203939

M:\01-Mapa de safra\Mapas Atualizados\Clealco\203939 - Sítio São Domingos (Daniel Vilela)\203939 - Sítio São Domingos (Daniel Vilela).dwg

Peterson Santos 06/10/2026