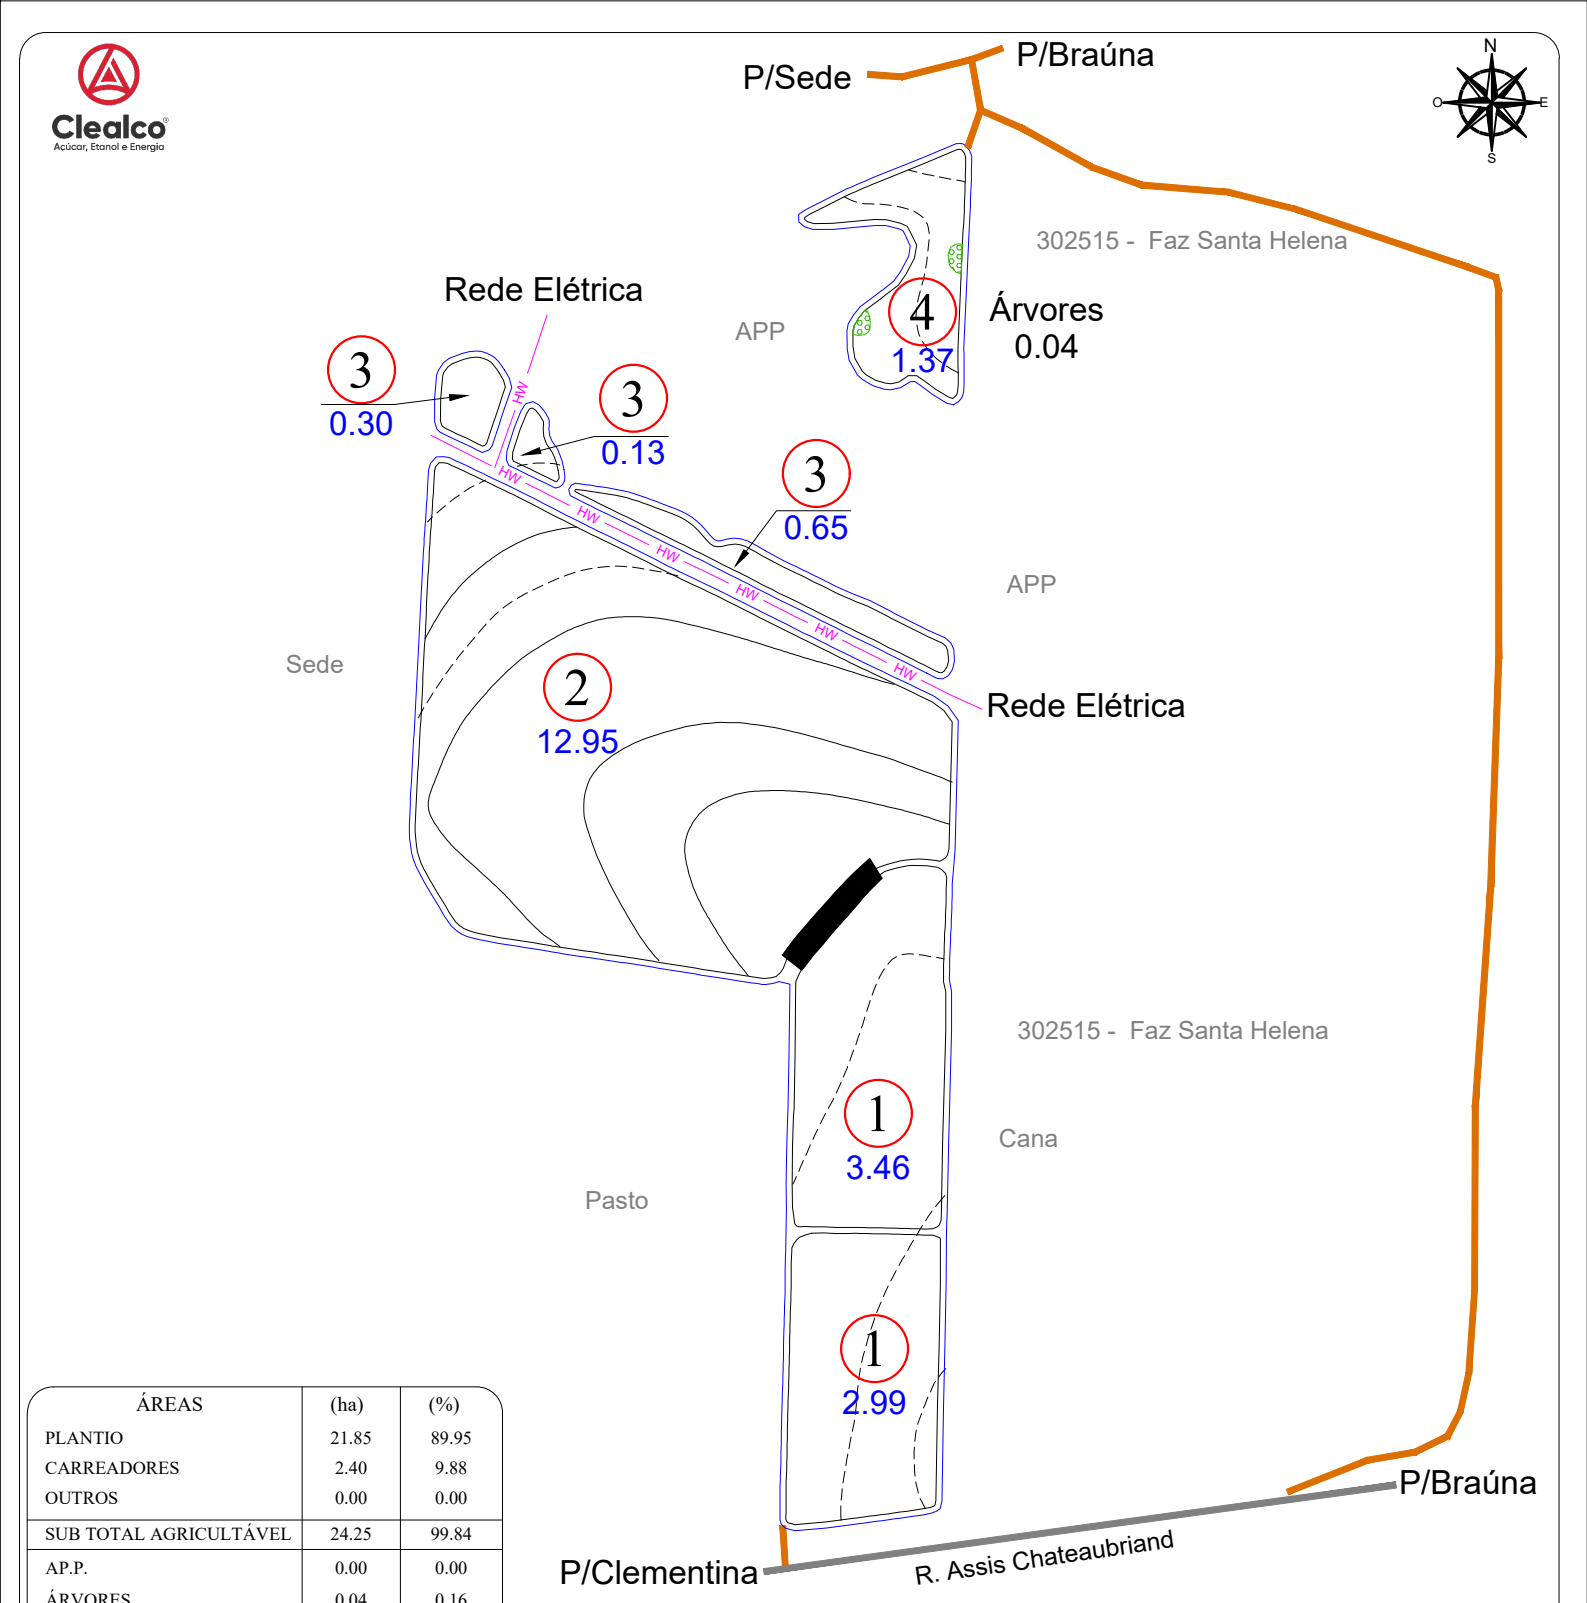


ÁREAS	(ha)	(%)
PLANTIO	21.85	89.95
CARREADORES	2.40	9.88
OUTROS	0.00	0.00
SUB TOTAL AGRICULTÁVEL	24.25	99.84
AP.P.	0.00	0.00
ÁRVORES	0.04	0.16
OUTROS	0.00	0.00
SUB TOTAL NÃO AGRICULT.	0.04	0.16
ÁREA TOTAL	24.29	100.00

LEGENDA


- FAZENDA
- TALHÃO
- REDE ELÉTRICA
- TERRAÇO BASE LARGA
- TERRAÇO EMBUTIDO
- (P.O.A) PATIO DE OPERAÇÃO

ESPAÇAMENTO: 1.50 x 1.50
TIRO MÉDIO ESTIMADO: 000.00 m
D.V: 5.35%

Nº TAL.	DATA PL.	ÁREA (ha)	VARIEDADE
1	05/2025	6.45	CTC 04
2		12.95	
3		1.08	
4		1.37	
TOTAL PLANTIO		21.85	

ESCALA: 1: 6.500

CROQUI DE ACESSO

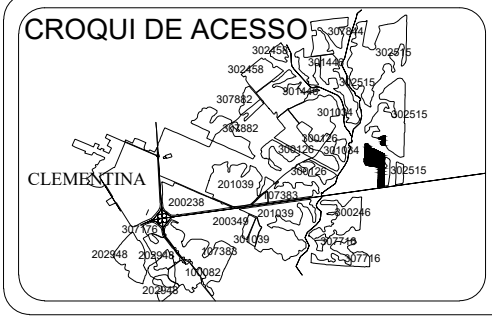

SÍTIO NOSSA SENHORA DE FÁTIMA

PROPRIETÁRIO: ANTONIO CESAR
COMPRADOR: CLEALCO
MUNICÍPIO: BRAÚNA - SP

DISTÂNCIAS (km):
UNID. I - Asfalto: 7.00 Terra.: 1.50
UNID.I I - Asfalto: 61.90 Terra.: 1.50

COORDENADAS: E(X): 563223.64 N(Y): 7616479.02
LAT: -21°33'12.2814" LONG: -50°23'21.8162"

CLEALCO - AÇÚCAR E ALCOOL S/A - DEPARTAMENTO DE GEOTECNOLOGIA

LEVANTAMENTO VIA:
SATÉLITE
GPS / VANT
GOOGLE

UNIDADE: I
PARTE: A/A
FUNDO AGRÍCOLA: 203976

M:\01-Mapa de safra\Mapas Atualizados\Clealco\203976 - Sítio Nossa Senhora de Fatima (Antonio Alves Pereira)\203976 - Sítio Nossa Senhora de Fatima (Antonio Alves Pereira).dwg

Peterson Santos 26/05/2026