
Clealco
Açúcar, Etanol e Energia

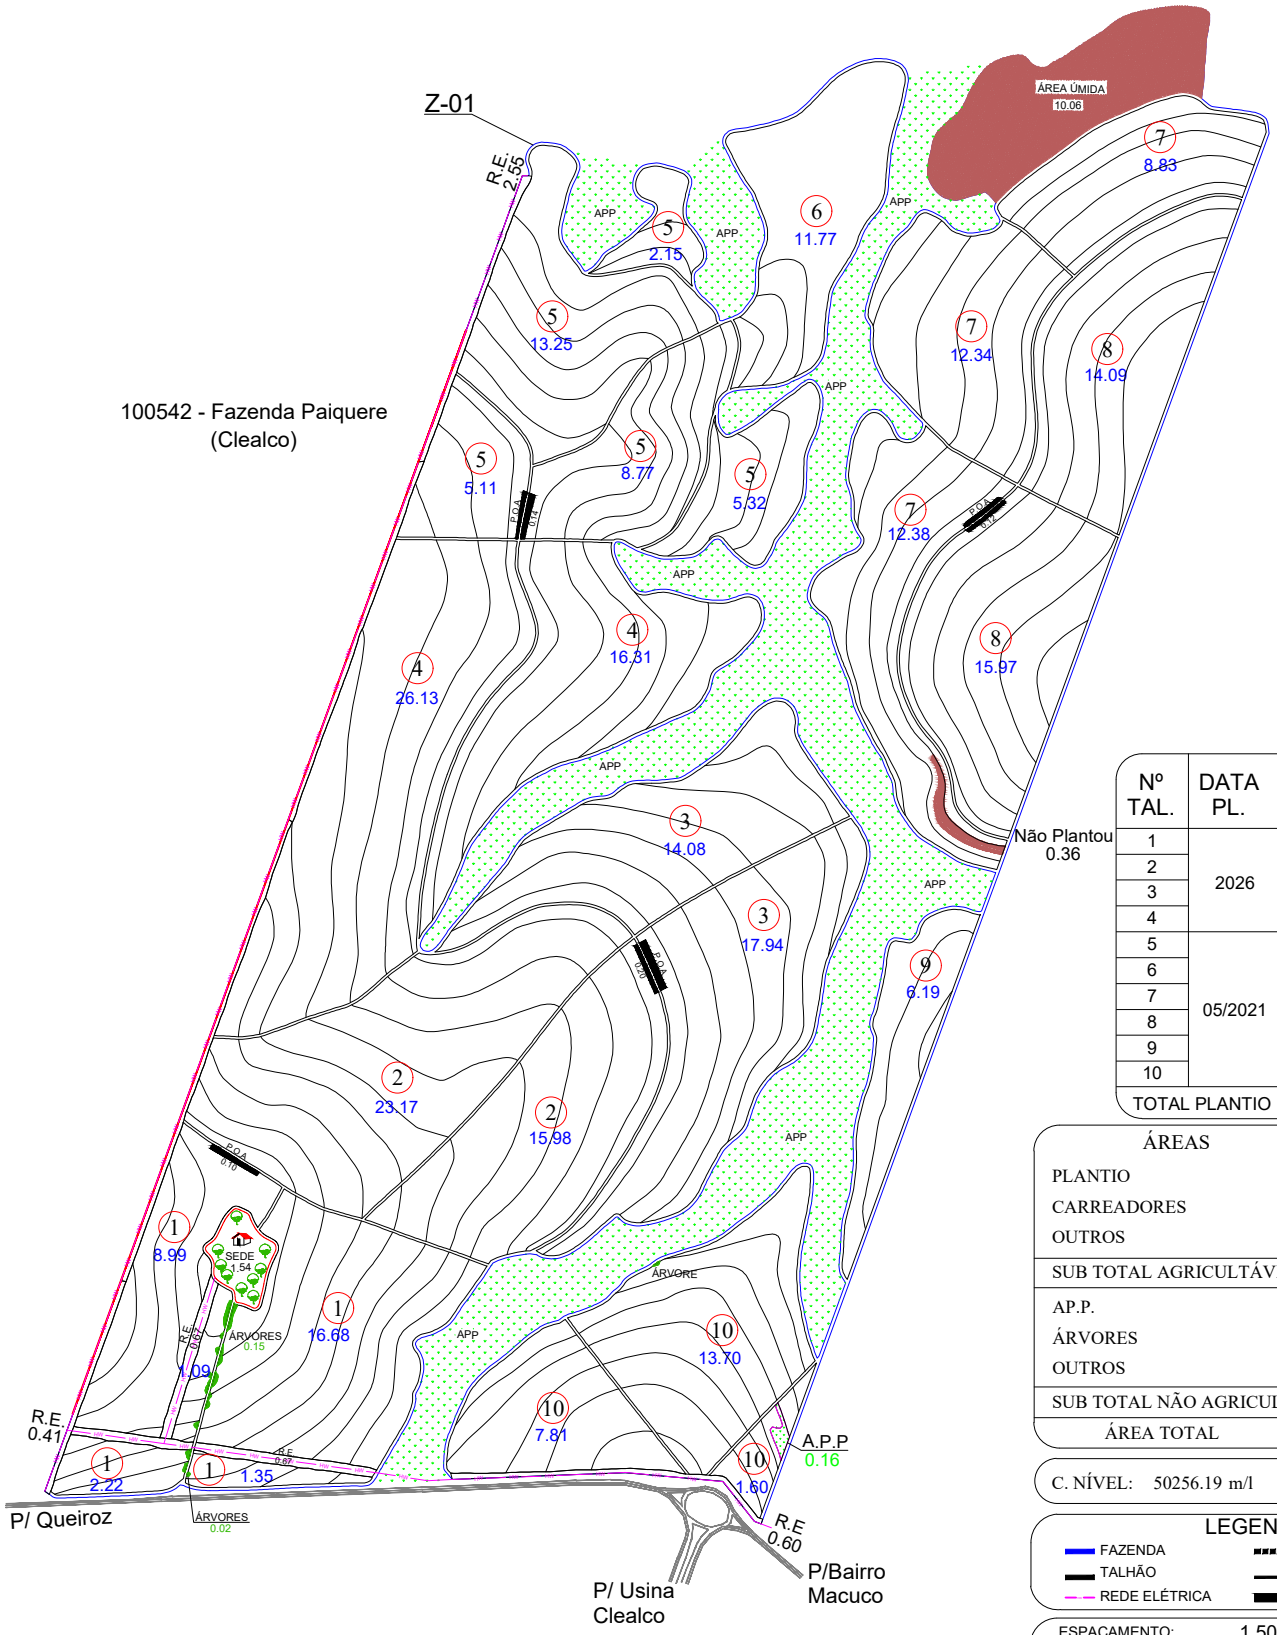

Nº TAL.	DATA PL.	ÁREA (ha)	VARIEDADE
1	2026	30.33	REFORMA
2		39.15	
3		32.02	
4		42.44	
5	05/2021	34.60	CTC 9001
6		11.77	
7		33.55	
8		30.06	
9		6.19	
10		23.11	
TOTAL PLANTIO		283.22	

ÁREAS	(ha)	(%)
PLANTIO	283.22	86.32
CARREADORES	27.20	8.29
OUTROS	10.62	3.24
SUB TOTAL AGRICULTÁVEL	321.04	97.85
AP.P.	0.16	0.05
ÁRVORES	0.17	0.05
OUTROS	6.74	2.05
SUB TOTAL NÃO AGRICULT.	7.07	2.15
ÁREA TOTAL	328.11	100.00


C. NÍVEL: 50256.19 m/l 11.56 ha 3.52 %

LEGENDA
- FAZENDA
- TALHÃO
- REDE ELÉTRICA
- TERRAÇO BASE LARGA
- TERRAÇO EMBUTIDO
- (P.O.A) PATIO DE OPERAÇÃO

ESPAÇAMENTO: 1.50 x 1.50
TIRO MÉDIO ESTIMADO: 000.00 m
D.V: 6.32 %

ESCALA: 1: 15.000

CROQUI DE ACESSO

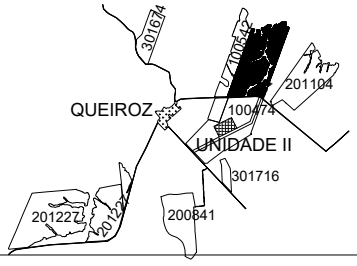

FAZENDA REALEZA

PROPRIETÁRIO: ALEXANDRE COGO
COMPRADOR: CLEALCO
MUNICÍPIO: QUEIROZ - SP

DISTÂNCIAS (km):
UNID. I - Asfalto: 53.00 Terra.: 1.50
UNID.I I - Asfalto: 4.50 Terra.: 1.50

COORDENADAS: E(X): 581715.37 N(Y): 7591258.17
LAT: -21°46'49.8315" LONG: -50°12'34.4635"

CLEALCO - AÇÚCAR E ALCOOL S/A - DEPARTAMENTO DE GEOTECNOLOGIA

LEVANTAMENTO VIA:
- SATÉLITE
- GPS / VANT
- GOOGLE

UNIDADE: I
PARTE: A/A
FUNDO AGRÍCOLA: 206823

M:\01-Mapa de safra\Mapas Atualizados\Clealco\206823 - Fazenda Realeza (Alexandre Cogo)\206823 - Fazenda Realeza (Alexandre Cogo).dwg

Benati 20/02/2026