

Clealco
Açúcar, Etanol e Energia

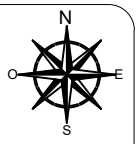

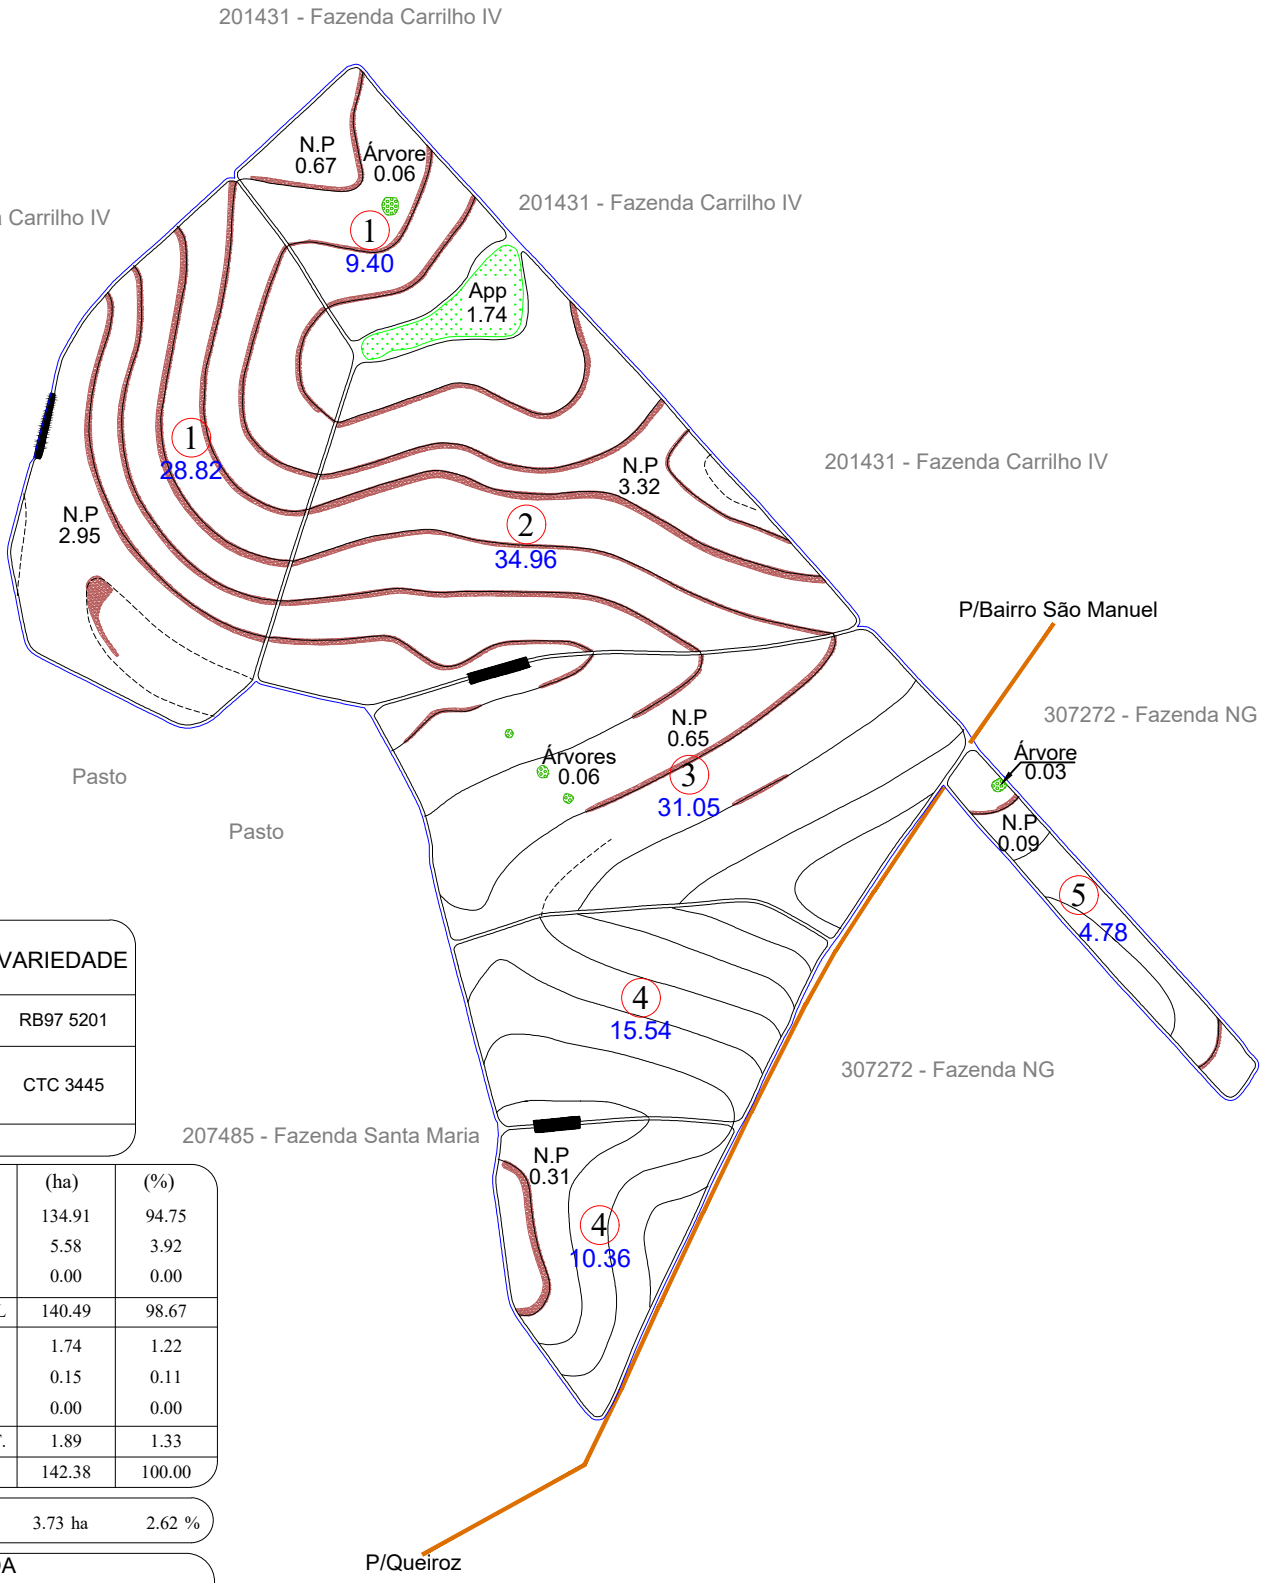

(N.P)-NÃO PLANTOU	
TALHÃO	(ha)
1	3.62
2	3.32
3	0.65
4	0.31
5	0.09
Total	7.99

Nº TAL.	DATA PL.	ÁREA (ha)	VARIEDADE
1	04/2025	38.22	RB97 5201
2		34.96	
3		31.05	CTC 3445
4		25.90	
5		4.78	
TOTAL PLANTIO		134.91	

ÁREAS	(ha)	(%)
PLANTIO	134.91	94.75
CARREADORES	5.58	3.92
OUTROS	0.00	0.00
SUB TOTAL AGRICULTÁVEL	140.49	98.67
AP.P.	1.74	1.22
ÁRVORES	0.15	0.11
OUTROS	0.00	0.00
SUB TOTAL NÃO AGRICULT.	1.89	1.33
ÁREA TOTAL	142.38	100.00

C. NÍVEL:	16233.77 m/l	3.73 ha	2.62 %


LEGENDA

- FAZENDA
- TALHÃO
- REDE ELÉTRICA
- TERRAÇO BASE LARGA
- TERRAÇO EMBUTIDO
- (P.O.A) PATIO DE OPERAÇÃO

ESPAÇAMENTO: 1.50 x 1.50
TIRO MÉDIO ESTIMADO: 313.14 m
D.V: 4.85 %

ESCALA: 1: 12.000

CROQUI DE ACESSO

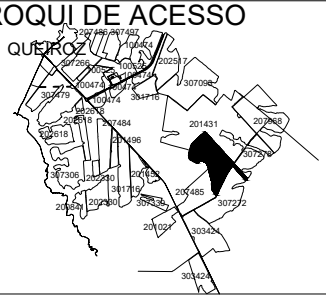

FAZENDA N.G.

PROPRIETÁRIO: JUCILEI MAGALHAES RODRIGUES
COMPRADOR: CLEALCO
MUNICÍPIO: QUEIROZ - SP

DISTÂNCIAS (km):
UNID. I - Asfalto: 68.00 Terra.: 2.50
UNID.I I - Asfalto: 7.00 Terra.: 2.50

COORDENADAS: E(X): 584111.07 N(Y): 7585461.87
LAT: -21°49'57.9334" LONG: -50°11'9.9805"

CLEALCO - AÇÚCAR E ALCOOL S/A - DEPARTAMENTO DE GEOTECNOLOGIA

LEVANTAMENTO VIA:
- SATÉLITE
- GPS / VANT
- GOOGLE

UNIDADE: II
PARTE: A/A
FUNDO AGRÍCOLA: 207059

M:\01-Mapa de safra\Mapas Atualizados\Clealco\207059 - Fazenda Ng (Jucilei Magalhaes Rodrigues)\207059 - Fazenda Ng (Jucilei Magalhaes Rodrigues).dwg

Bruno Gamboa 21/11/25