
Clealco
Açúcar, Etanol e Energia

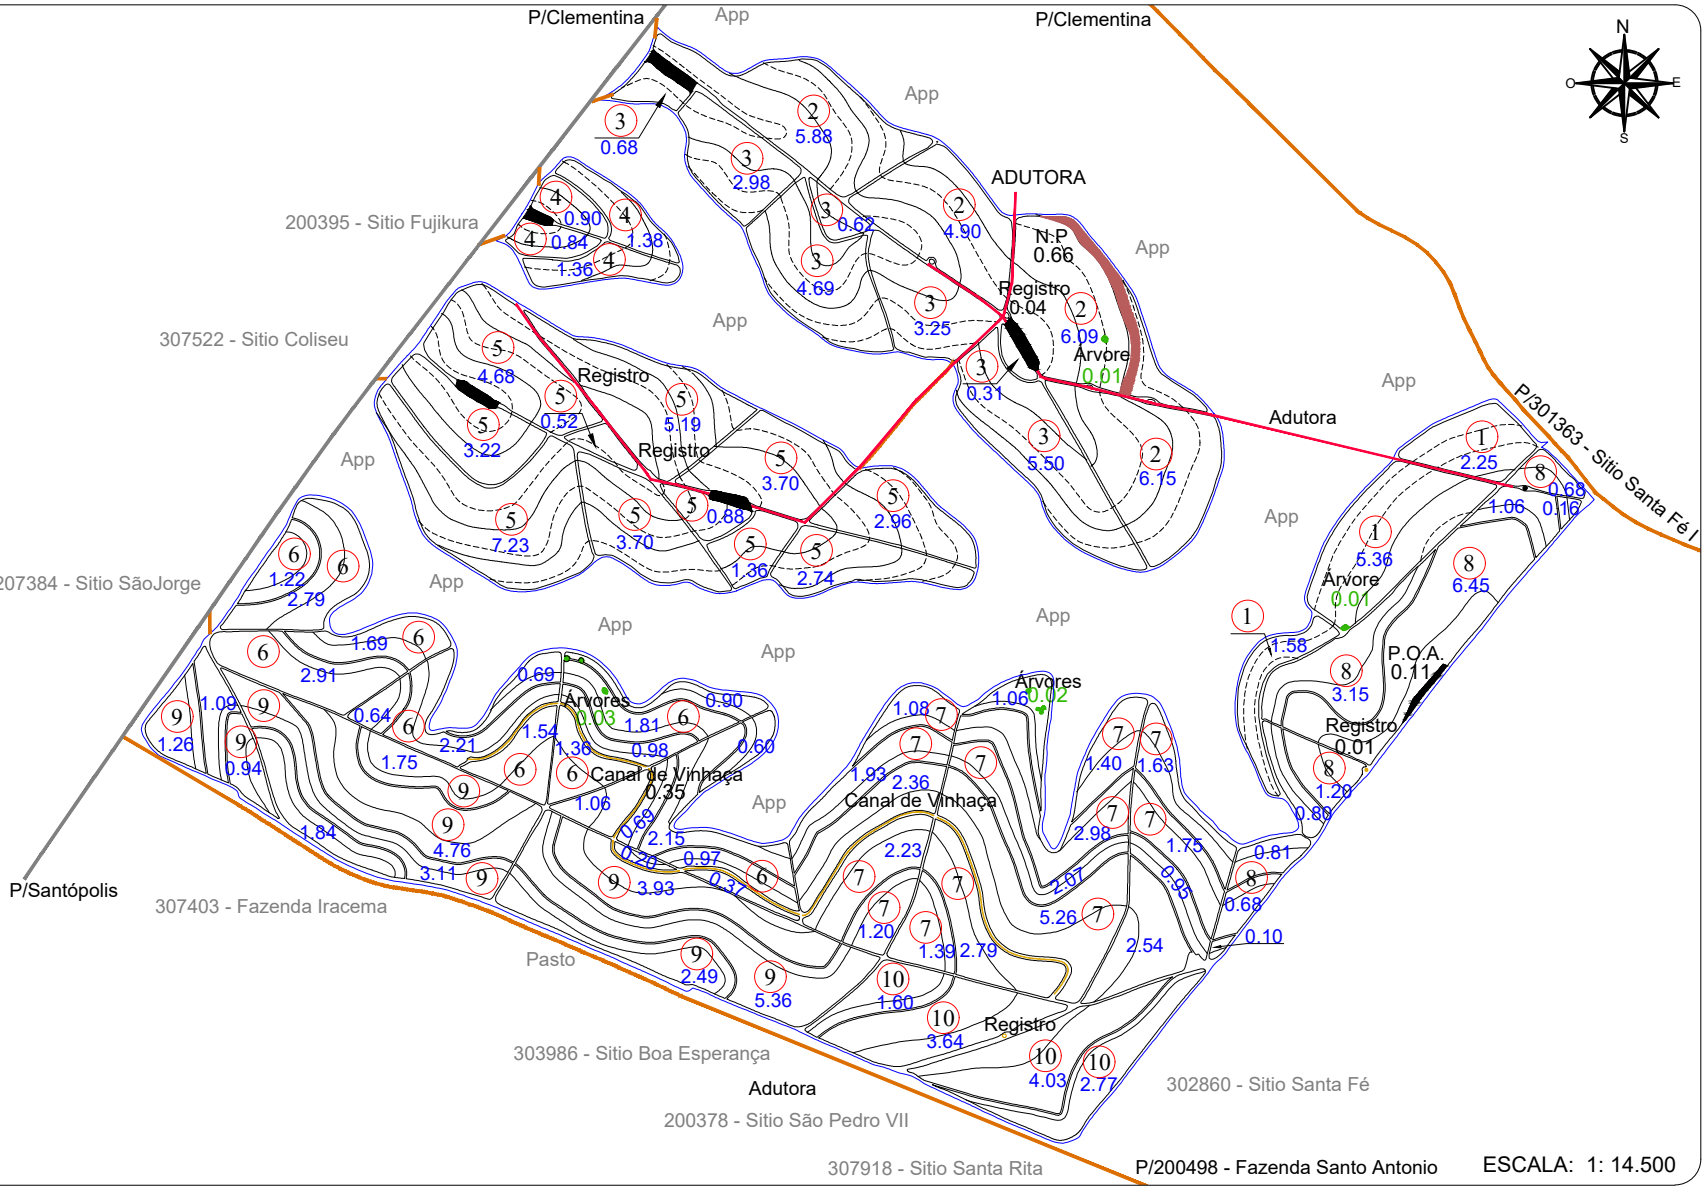


| (N.P)-NÃO PLANTOU | |
|---|---|
| TALHÃO | (ha) |
| 2 | 0.66 |
| Total | 0.66 |

| Nº TAL. | DATA PL. | ÁREA (ha) | VARIEDADE |
|---|---|---|---|
| 1 | 06/2025 | 9.19 | RB97 5033 |
| 2 | 05/2025 | 23.02 | RB96 6928 |
| 3 | | 18.03 | |
| 4 | | 4.48 | |
| 5 | | 36.18 | |
| 6 | 07/2021 | 24.41 | RB 97 5033 |
| 7 | | 32.62 | |
| 8 | | 15.09 | |
| 9 | | 26.90 | |
| 10 | | 12.04 | |
| TOTAL PLANTIO | | 201.96 | |

| ÁREAS | (ha) | (%) |
|---|---|---|
| PLANTIO | 201.96 | 90.01 |
| CARREADORES | 21.17 | 9.43 |
| OUTROS | 1.13 | 0.50 |
| SUB TOTAL AGRICULTÁVEL | 224.26 | 99.95 |
| AP.P. | 0.00 | 0.00 |
| ÁRVORES | 0.07 | 0.03 |
| OUTROS | 0.04 | 0.02 |
| SUB TOTAL NÃO AGRICULT. | 0.11 | 0.05 |
| ÁREA TOTAL | 224.37 | 100.00 |


| C. NÍVEL: | 26288.28 m/l | 6.05 ha | 2.69 % |
|---|---|---|---|

## LEGENDA

- FAZENDA
- TALHÃO
- REDE ELÉTRICA
- TERRAÇO BASE LARGA
- TERRAÇO EMBUTIDO

| ESPAÇAMENTO: | 1.50 x 1.50 | D.V: 7.91 % |
|---|---|---|
| TIRO MÉDIO ESTIMADO: | 000.00 m | |

## CROQUI DE ACESSO

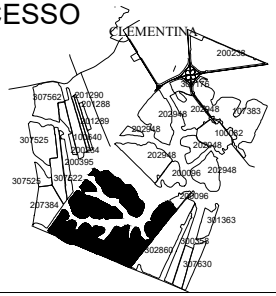


# FAZENDA SANTA LUIZA

PROPRIETÁRIO: FRANCISCO DE A. BRANDÃO F.
COMPRADOR: CLEALCO
MUNICÍPIO: CLEMENTINA - SP

DISTÂNCIAS (km):
UNID. I - Asfalto: 4.00 Terra.: 1.50
UNID.I I - Asfalto: 51.80 Terra.: 1.50

COORDENADAS: E(X): 555793.37 N(Y): 7611334.89
LAT: -21°36'0.4832" LONG: -50°27'39.5268"

CLEALCO - AÇÚCAR E ALCOOL S/A - DEPARTAMENTO DE GEOTECNOLOGIA

LEVANTAMENTO VIA:
SATÉLITE
GPS / VANT
GOOGLE

UNIDADE: I
PARTE: A/A
FUNDO AGRÍCOLA: 207251

ESCALA: 1: 14.500

M:\01-Mapa de safra\Mapas Atualizados\Clealco\207251 - Fazenda Santa Luiza (Francisco de Assis Brandão Filho)\207251 - Fazenda Santa Luiza (Francisco de Assis Brandão Filho).dwg

Bruno Gamboa 30/10/25