ZONA DV	Nº TAL.	DATA PL.	ÁREA (ha)	VARIEDADE
1 5.52 %	1	05/2023	28.72	DIVERSAS
TOTAL PLANTIO			28.72	--------


ÁREAS	(ha)	(%)
PLANTIO	28.72	92.94
CARREADORES	2.03	6.57
OUTROS	0.11	0.36
SUB TOTAL AGRICULTÁVEL	30.86	99.87
AP.P.	0.00	0.00
ÁRVORES	0.04	0.13
OUTROS	0.00	0.00
SUB TOTAL NÃO AGRICULT.	0.04	0.13
ÁREA TOTAL	30.90	100.00


C. NÍVEL: 7072.30 m/l 1.63 ha 5.26 %

LEGENDA

- FAZENDA
- TALHÃO
- CURVA DE NÍVEL
- CARREADOR
- CONFRONTANTE
- REDE ELÉTRICA
- TRAJETO VAZIO
- TRAJETO CARREGADO

PLANTIO MANUAL - ESPAÇAMENTO: 1.50 X 1.50
TIRO MÉDIO ESTIMADO: 203.46 m

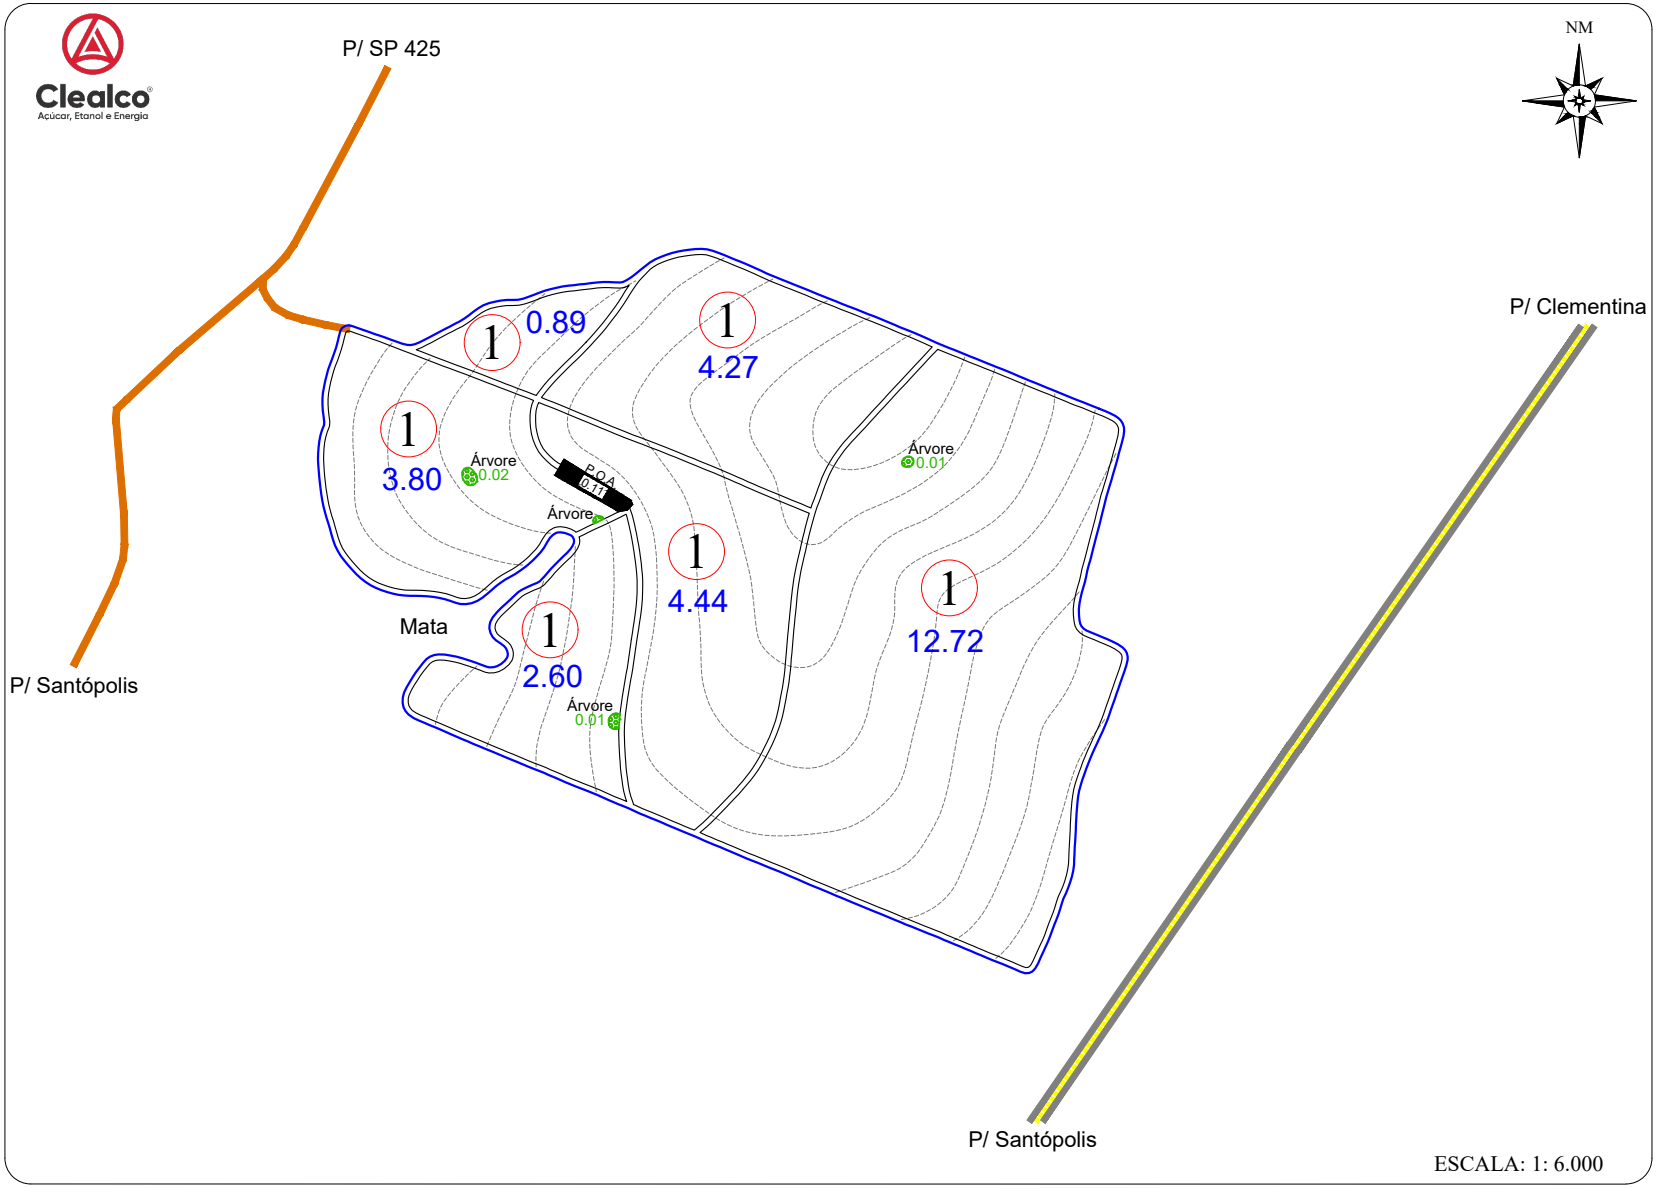

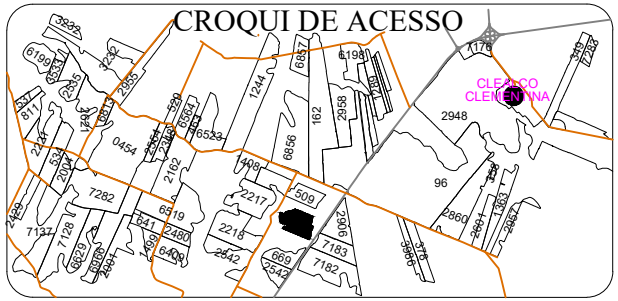

SÍTIO SÃO LUIZ II

PROPRIETÁRIO: SUMIE YDA
ARRENDATÁRIO: CLEALCO S/A
MUNICÍPIO: CLEMENTINA

DISTÂNCIAS (km):
UNID. I - Asfalto: 17.00 Terra.: 0.00
UNID.I I - Asfalto: 65.00 Terra.: 0.00
UNID. III -Asfalto: 67.00 Terra.: 0.00

COORDENADAS: E(X): 554148.46 N(Y): 7610721.42
LAT: -21°36'20.6186" LONG: -50°28'36.6625"

CLEALCO - AÇÚCAR E ALCOOL S/A - DEPARTAMENTO DE TOPOGRAFIA

UNIDADE: II
PARTE: A/A
FUNDO AGRÍCOLA: 207366

M:\01-Mapa de safra\Mapas Atualizados\Clealco\207366 - Sítio São Luiz II e IV (Sumie Yda)\207366 - Sítio São Luiz II e IV (Sumie Yda).dwg

Rafael 02/03/2023