
Clealco
Açúcar, Etanol e Energia

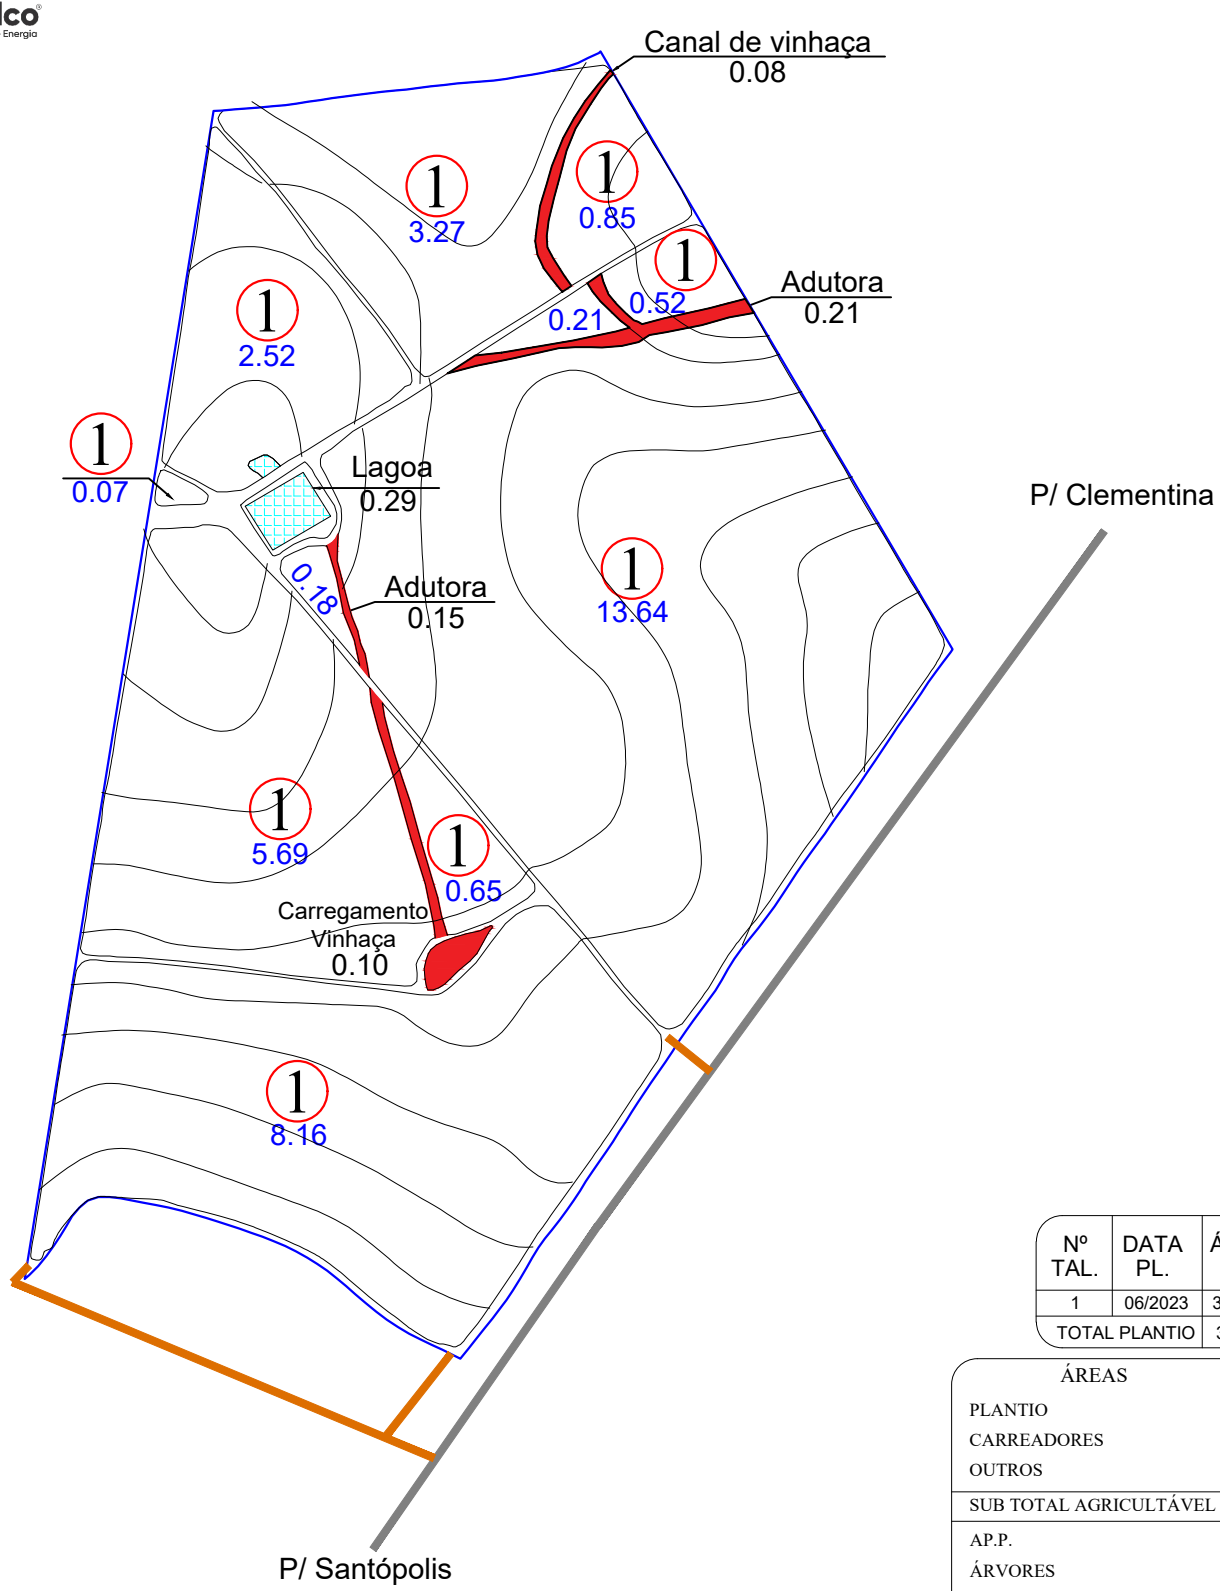

Nº TAL.	DATA PL.	ÁREA (ha)	VARIEDADE
1	06/2023	35.76	RB98 5476
TOTAL PLANTIO		35.76	

ÁREAS	(ha)	(%)
PLANTIO	35.76	93.89
CARREADORES	1.50	3.93
OUTROS	0.00	0.00
SUB TOTAL AGRICULTÁVEL	37.26	97.82
AP.P.	0.00	0.00
ÁRVORES	0.00	0.00
OUTROS	0.83	2.18
SUB TOTAL NÃO AGRICULT.	0.83	2.18
ÁREA TOTAL	38.09	100.00

C. NÍVEL: 6452.13 m/l 1.48 ha 3.90 %


ESCALA: 1: 5.500

LEGENDA

- FAZENDA
- TALHÃO
- REDE ELÉTRICA
- VAZIO
- TERRAÇO BASE LARGA
- TERRAÇO EMBUTIDO
- (P.O.A) PATIO DE OPERAÇÃO
- CARREGADO

ESPAÇAMENTO: 1.50 x 1.50
TIRO MÉDIO ESTIMADO: 000.00 m
D.V: 5.63 %

CROQUI DE ACESSO

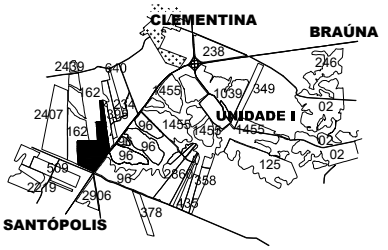

SITIO SÃO JORGE

PROPRIETÁRIO: LEONICE F. FERREIRA E OUTROS
COMPRADOR: CLEALCO
MUNICÍPIO: CLEMENTINA - SP

DISTÂNCIAS (km):
UNID. I - Asfalto: 4.00 Terra.: 1.50
UNID.I I - Asfalto: 51.80 Terra.: 1.50

COORDENADAS: E(X): 555199.64 N(Y): 7611922.54
LAT: -21°35'41.4368" LONG: -50°28'0.2456"

CLEALCO - AÇÚCAR E ALCOOL S/A - DEPARTAMENTO DE GEOTECNOLOGIA

LEVANTAMENTO VIA:
- SATÉLITE
- GPS / VANT
- GOOGLE

UNIDADE: I
PARTE: A/A
FUNDO AGRÍCOLA: 207384

M:\01-Mapa de safra\Mapas Atualizados\Clealco\207384 - Sítio São Jorge (Leonice Fernandes Ferreira)\207384 - Sítio São Jorge (Leonice Fernandes Ferreira).dwg

Bruno Gamboa 07/04/26