

Clealco
Açúcar, Etanol e Energia

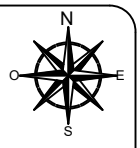

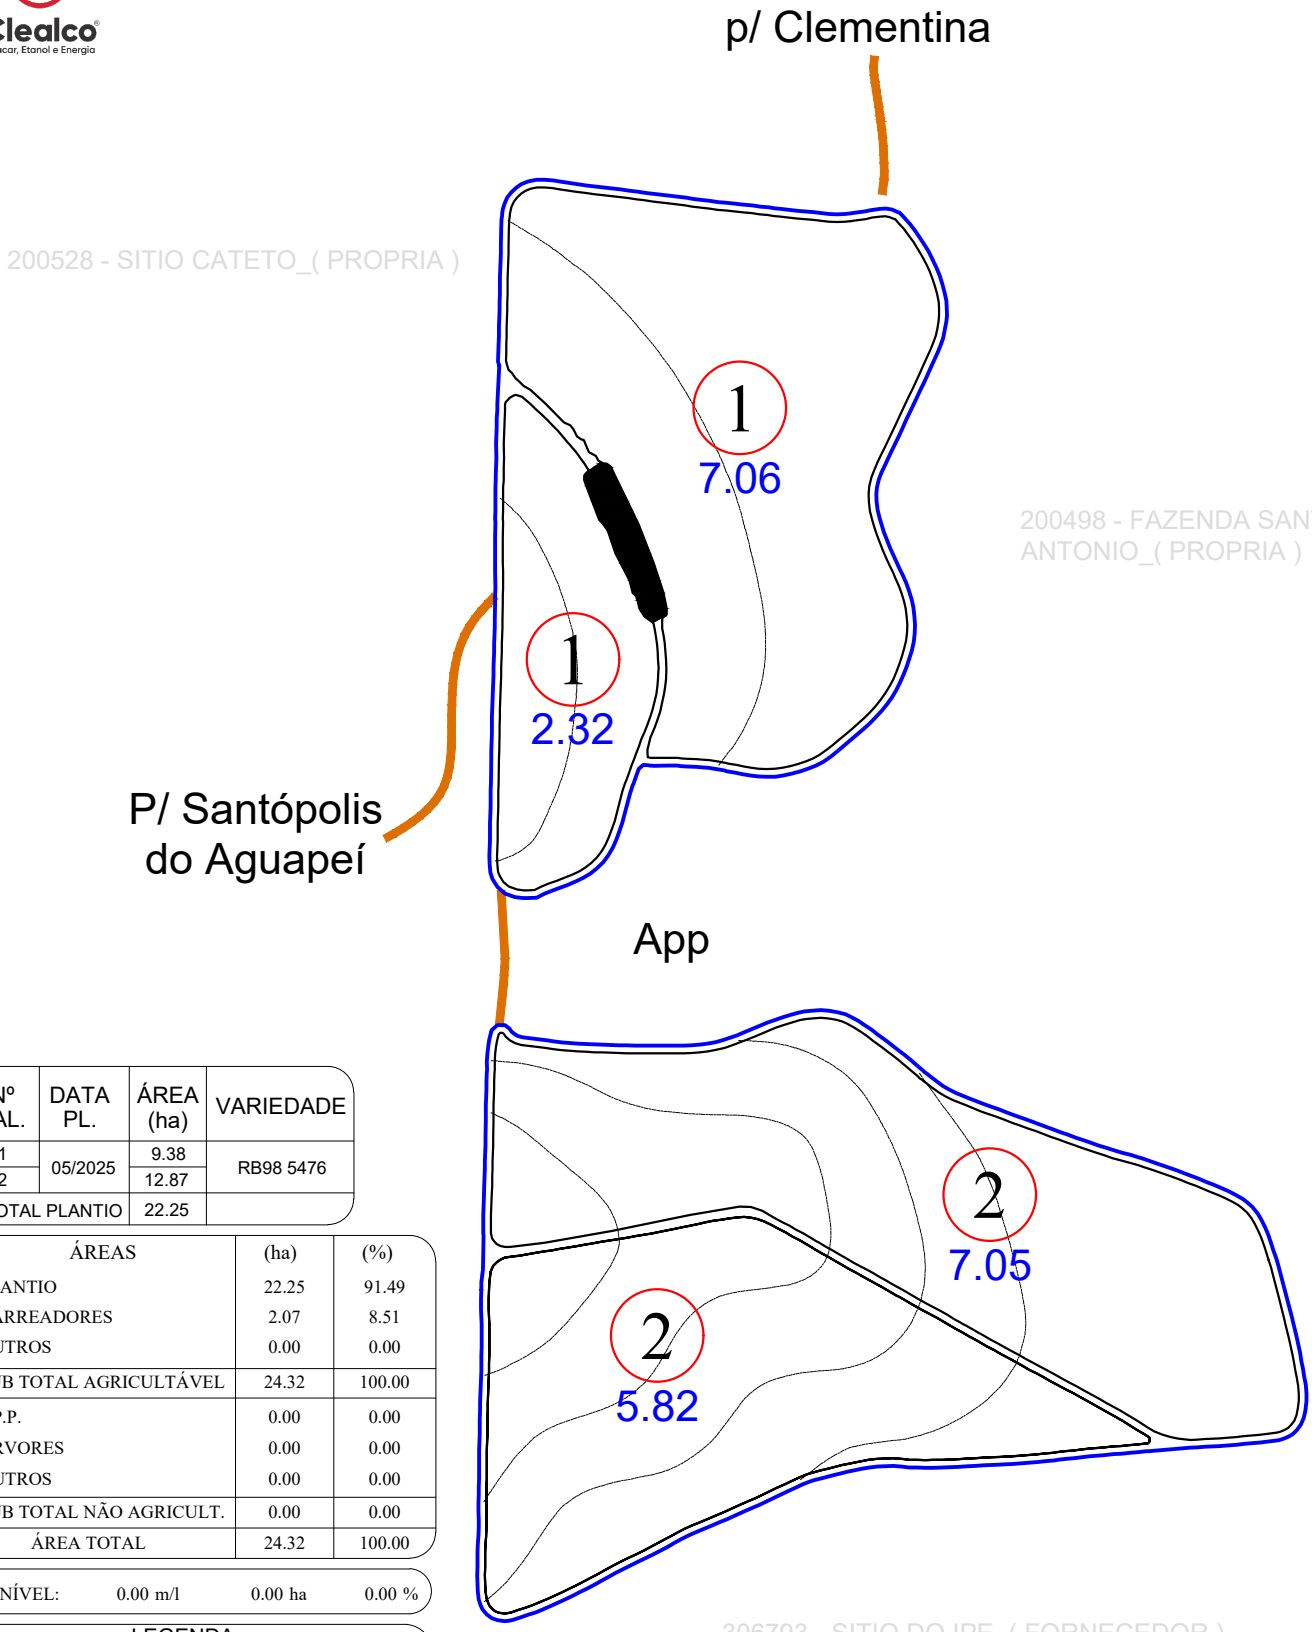

Nº TAL.	DATA PL.	ÁREA (ha)	VARIEDADE
1	05/2025	9.38	RB98 5476
2		12.87	
TOTAL PLANTIO		22.25	

ÁREAS	(ha)	(%)
PLANTIO	22.25	91.49
CARREADORES	2.07	8.51
OUTROS	0.00	0.00
SUB TOTAL AGRICULTÁVEL	24.32	100.00
AP.P.	0.00	0.00
ÁRVORES	0.00	0.00
OUTROS	0.00	0.00
SUB TOTAL NÃO AGRICULT.	0.00	0.00
ÁREA TOTAL	24.32	100.00

C. NÍVEL: 0.00 m/l 0.00 ha 0.00 %


LEGENDA

- FAZENDA
- TALHÃO
- REDE ELÉTRICA
- TERRAÇO BASE LARGA
- TERRAÇO EMBUTIDO
- (P.O.A) PATIO DE OPERAÇÃO

ESPAÇAMENTO: 1.50 x 1.50
TIRO MÉDIO ESTIMADO: 220.27 m
D.V: 0.00 %

ESCALA: 1: 5.000

CROQUI DE ACESSO

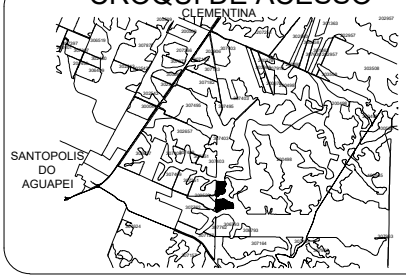

FAZENDA SANTO ANTONIO

PROPRIETÁRIO: HEITOR MASCHIETTO ROSSETTI
COMPRADOR: CLEALCO
MUNICÍPIO: CLEMENTINA - SP

DISTÂNCIAS (km):
UNID. I - Asfalto: 14.60 Terra.: 0.00
UNID.I I - Asfalto: 61.00 Terra.: 0.00

COORDENADAS: E(X): 555453.05 N(Y): 7606602.38
LAT: -21°38'34.4441" LONG: -50°27'50.7953"

CLEALCO - AÇÚCAR E ALCOOL S/A - DEPARTAMENTO DE GEOTECNOLOGIA

LEVANTAMENTO VIA:
- SATÉLITE
- GPS / VANT
- GOOGLE

UNIDADE: I
PARTE: A/A
FUNDO AGRÍCOLA: 207715

M:\01-Mapa de safra\Mapas Atualizados\Clealco\207715 - Fazenda Santo Antonio (Heitor Maschietto Rossetti)\207715 - Fazenda Santo Antonio (Heitor Maschietto Rossetti).dwg

Benati 18/09/2025