
Clealco
Açúcar, Etanol e Energia

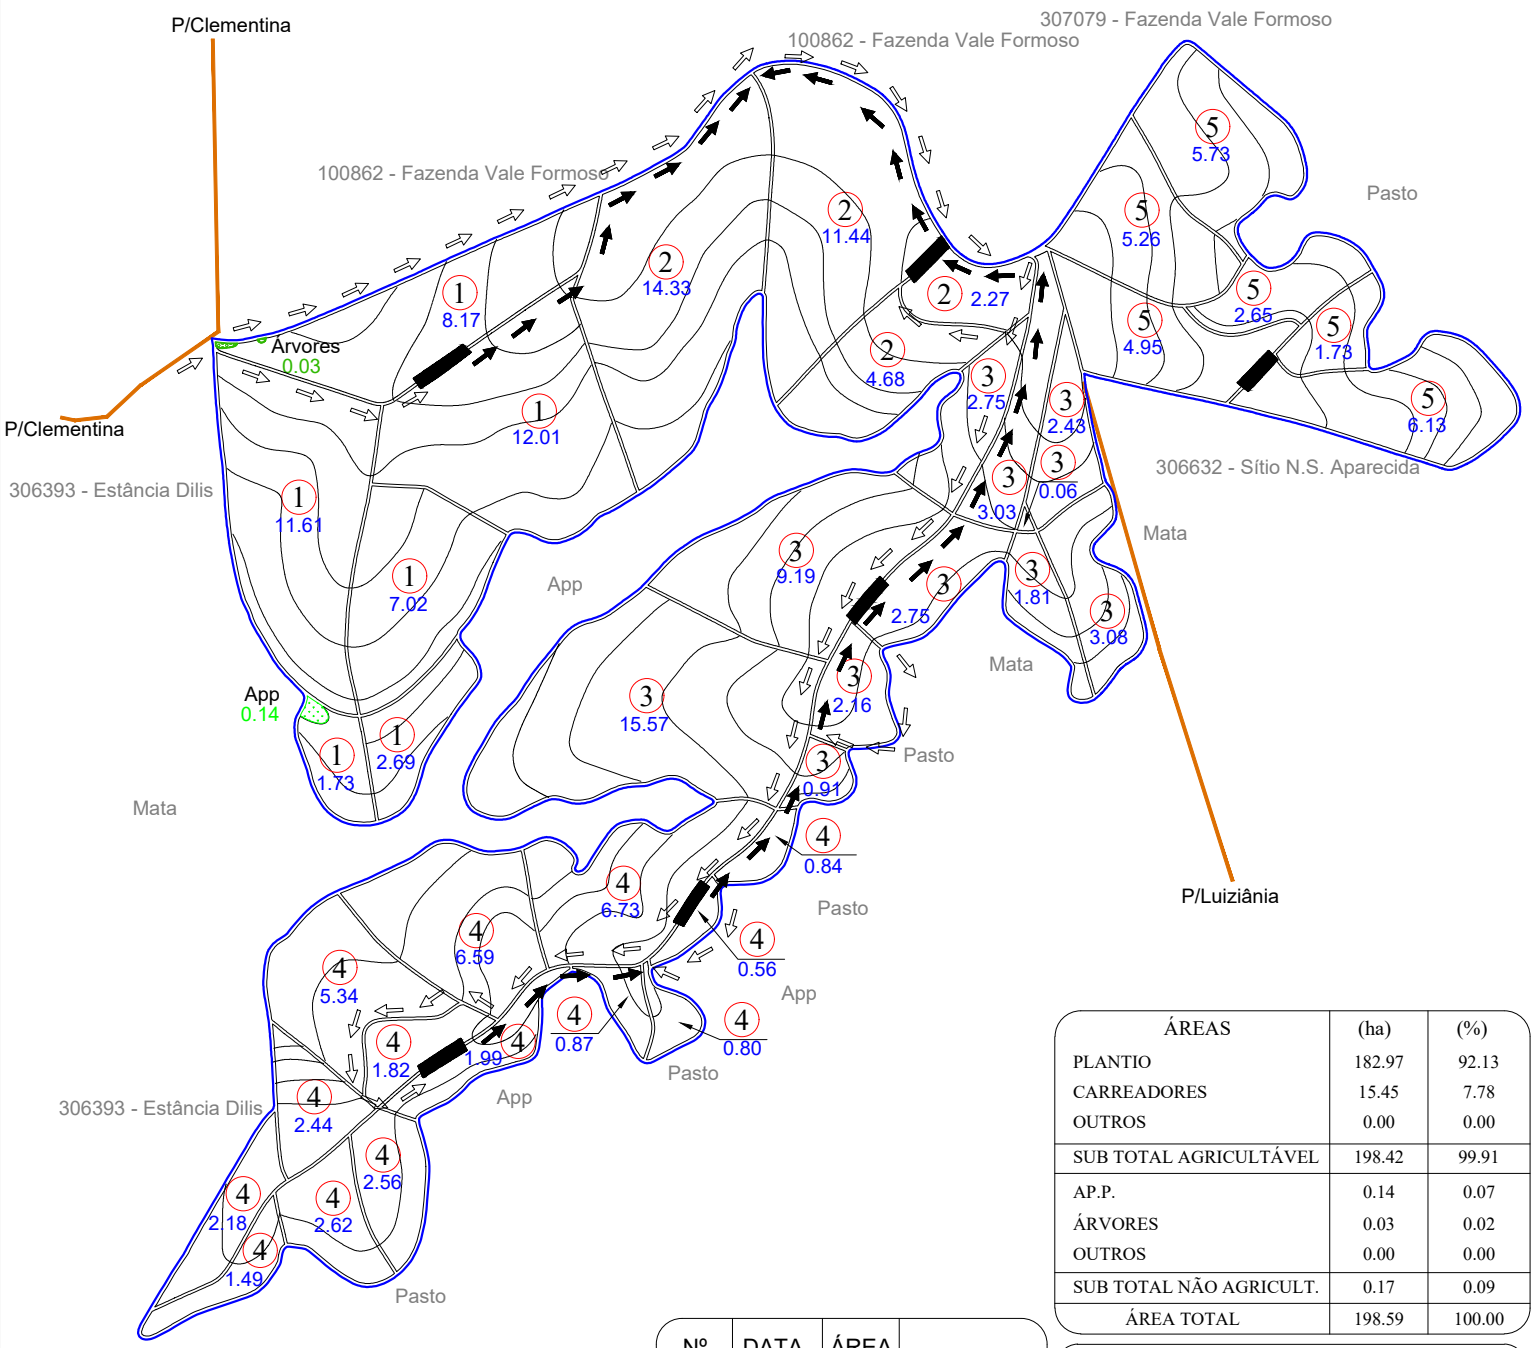

ÁREAS	(ha)	(%)
PLANTIO	182.97	92.13
CARREADORES	15.45	7.78
OUTROS	0.00	0.00
SUB TOTAL AGRICULTÁVEL	198.42	99.91
AP.P.	0.14	0.07
ÁRVORES	0.03	0.02
OUTROS	0.00	0.00
SUB TOTAL NÃO AGRICULT.	0.17	0.09
ÁREA TOTAL	198.59	100.00

Nº TAL.	DATA PL.	ÁREA (ha)	VARIEDADE
1	2026	43.23	PRÉ PLANTIO
2		32.72	
3		43.74	
4		36.83	
5		26.45	
TOTAL PLANTIO		182.92	

C. NÍVEL: 18669.64 m/l 4.29 ha 2.16 %

LEGENDA

- FAZENDA
- TALHÃO
- REDE ELÉTRICA
- TERRAÇO BASE LARGA
- TERRAÇO EMBUTIDO
- (P.O.A) PATIO DE OPERAÇÃO

ESPAÇAMENTO: 1.50 x 1.50
TIRO MÉDIO ESTIMADO: 206.42 m
D.V: 7.26 %

ESCALA: 1: 13.500

CROQUI DE ACESSO



FAZENDA NOSSA SENHORA APARECIDA

PROPRIETÁRIO: SIDONIO LEMOS DE M. JUNIOR
COMPRADOR: CLEALCO
MUNICÍPIO: BRAÚNA - SP

DISTÂNCIAS (km):
UNID. I - Asfalto: 12.50 Terra.: 3.00
UNID.I I - Asfalto: 23.00 Terra.: 17.50

COORDENADAS: E(X): 568864.90 N(Y): 7614438.18
LAT: -21°34'17.9072" LONG: -50°20'5.3856"

CLEALCO - AÇÚCAR E ALCOOL S/A - DEPARTAMENTO DE GEOTECNOLOGIA

LEVANTAMENTO VIA:
SATÉLITE
GPS / VANT
GOOGLE

UNIDADE: I
PARTE: A/A
FUNDO AGRÍCOLA: 207749

N:\IE-Mapa de safra\Mapas Atualizados\Clealco\207749 - Fazenda Nossa Senhora Aparecida - Sidonio Lemos De Melo Junior\207749 - Fazenda Nossa Senhora Aparecida - Sidonio Lemos De Melo Junior.dwg

Bruno Gamboa 30/04/26