
Clealco
Açúcar, Etanol e Energia

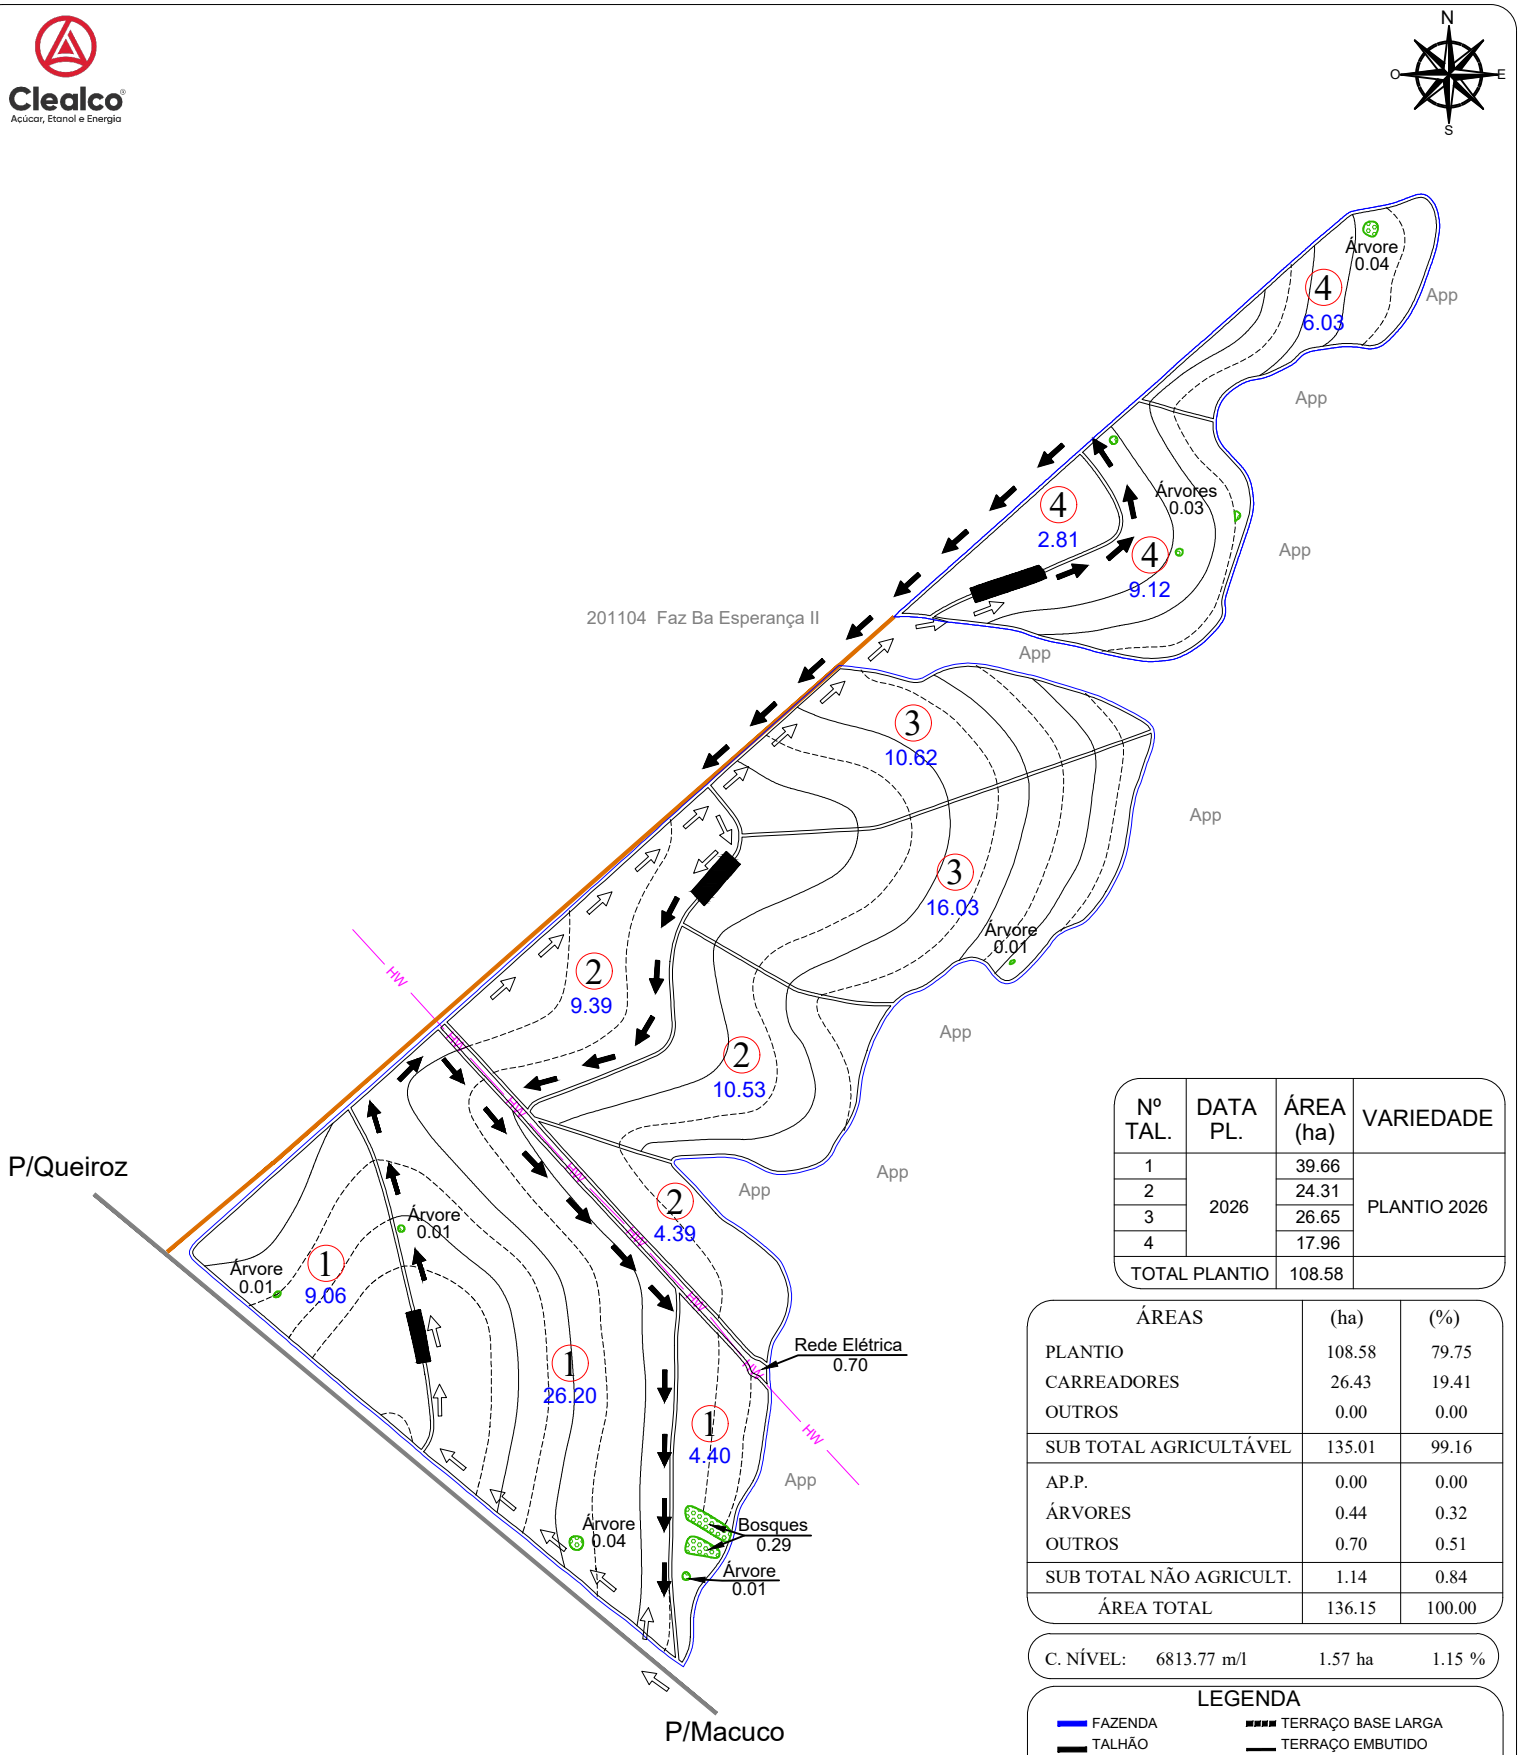

Nº TAL.	DATA PL.	ÁREA (ha)	VARIEDADE
1	2026	39.66	PLANTIO 2026
2		24.31	
3		26.65	
4		17.96	
TOTAL PLANTIO		108.58	

ÁREAS	(ha)	(%)
PLANTIO	108.58	79.75
CARREADORES	26.43	19.41
OUTROS	0.00	0.00
SUB TOTAL AGRICULTÁVEL	135.01	99.16
AP.P.	0.00	0.00
ÁRVORES	0.44	0.32
OUTROS	0.70	0.51
SUB TOTAL NÃO AGRICULT.	1.14	0.84
ÁREA TOTAL	136.15	100.00

C. NÍVEL: 6813.77 m/l 1.57 ha 1.15 %


LEGENDA

- FAZENDA
- TALHÃO
- REDE ELÉTRICA
- TERRAÇO BASE LARGA
- TERRAÇO EMBUTIDO
- (P.O.A) PATIO DE OPERAÇÃO

ESPAÇAMENTO: 1.50 x 1.50
TIRO MÉDIO ESTIMADO: 295.06 m
D.V: 5.61 %

ESCALA: 1: 12.000

CROQUI DE ACESSO

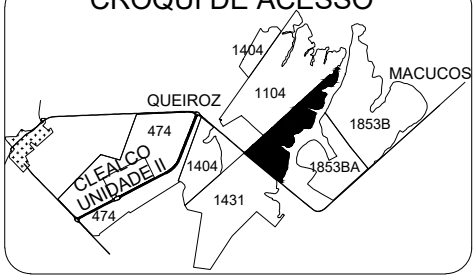

FAZENDA SANTA IZABEL

PROPRIETÁRIO: NILTON ZANCHETTA
COMPRADOR: CLEALCO
MUNICÍPIO: QUEIROZ - SP

DISTÂNCIAS (km):
UNID. I - Asfalto: 58.00 Terra.: 2.20
UNID.I I - Asfalto: 4.40 Terra.: 2.20

COORDENADAS: E(X): 584212.71 N(Y): 7589510.41
LAT: -21°47'46.2498" LONG: -50°11'7.1853"

CLEALCO - AÇÚCAR E ALCOOL S/A - DEPARTAMENTO DE GEOTECNOLOGIA

UNIDADE: II
PARTE: A/A
FUNDO AGRÍCOLA: 207969

M:\01-Mapa de safra\Mapas Atualizados\Clealco\207969 - Fazenda Santa Izabel (Nilton Zanchetta)\207969 - Fazenda Santa Izabel (Nilton Zanchetta) .dwg

Peterson Santos 01/06/2026