DV	CLA	Nº TAL.	DATA PL.	ÁREA (ha)	VAR.
7.32 %		1	07/2017	7.10	RB 867515
		2		17.88	
		3		5.70	
		4		0.32	
		5		12.07	
		6		14.24	
		7		2.18	
		8		11.11	
TOTAL PLANTIO				70.60	--------


ÁREAS	(ha)	(%)
PLANTIO	70.60	96.33
CARREADORES	2.65	3.62
OUTROS	0.00	0.00
SUB TOTAL AGRICULTÁVEL	73.25	99.95
AP.P.	0.00	0.00
ÁRVORES	0.04	0.05
OUTROS	0.00	0.00
SUB TOTAL NÃO AGRICULT.	0.04	0.05
ÁREA TOTAL	73.29	100.00

C. NÍVEL: 0.00 m/l 0.00 ha 0.00 %


LEGENDA

- FAZENDA
- TALHÃO
- CURVA DE NÍVEL
- CARREADOR
- CONFRONTANTE
- REDE ELÉTRICA
- TRAJETO VAZIO
- TRAJETO CARREGADO

PLANTIO MANUAL - ESPAÇAMENTO: 1.50 X 1.50

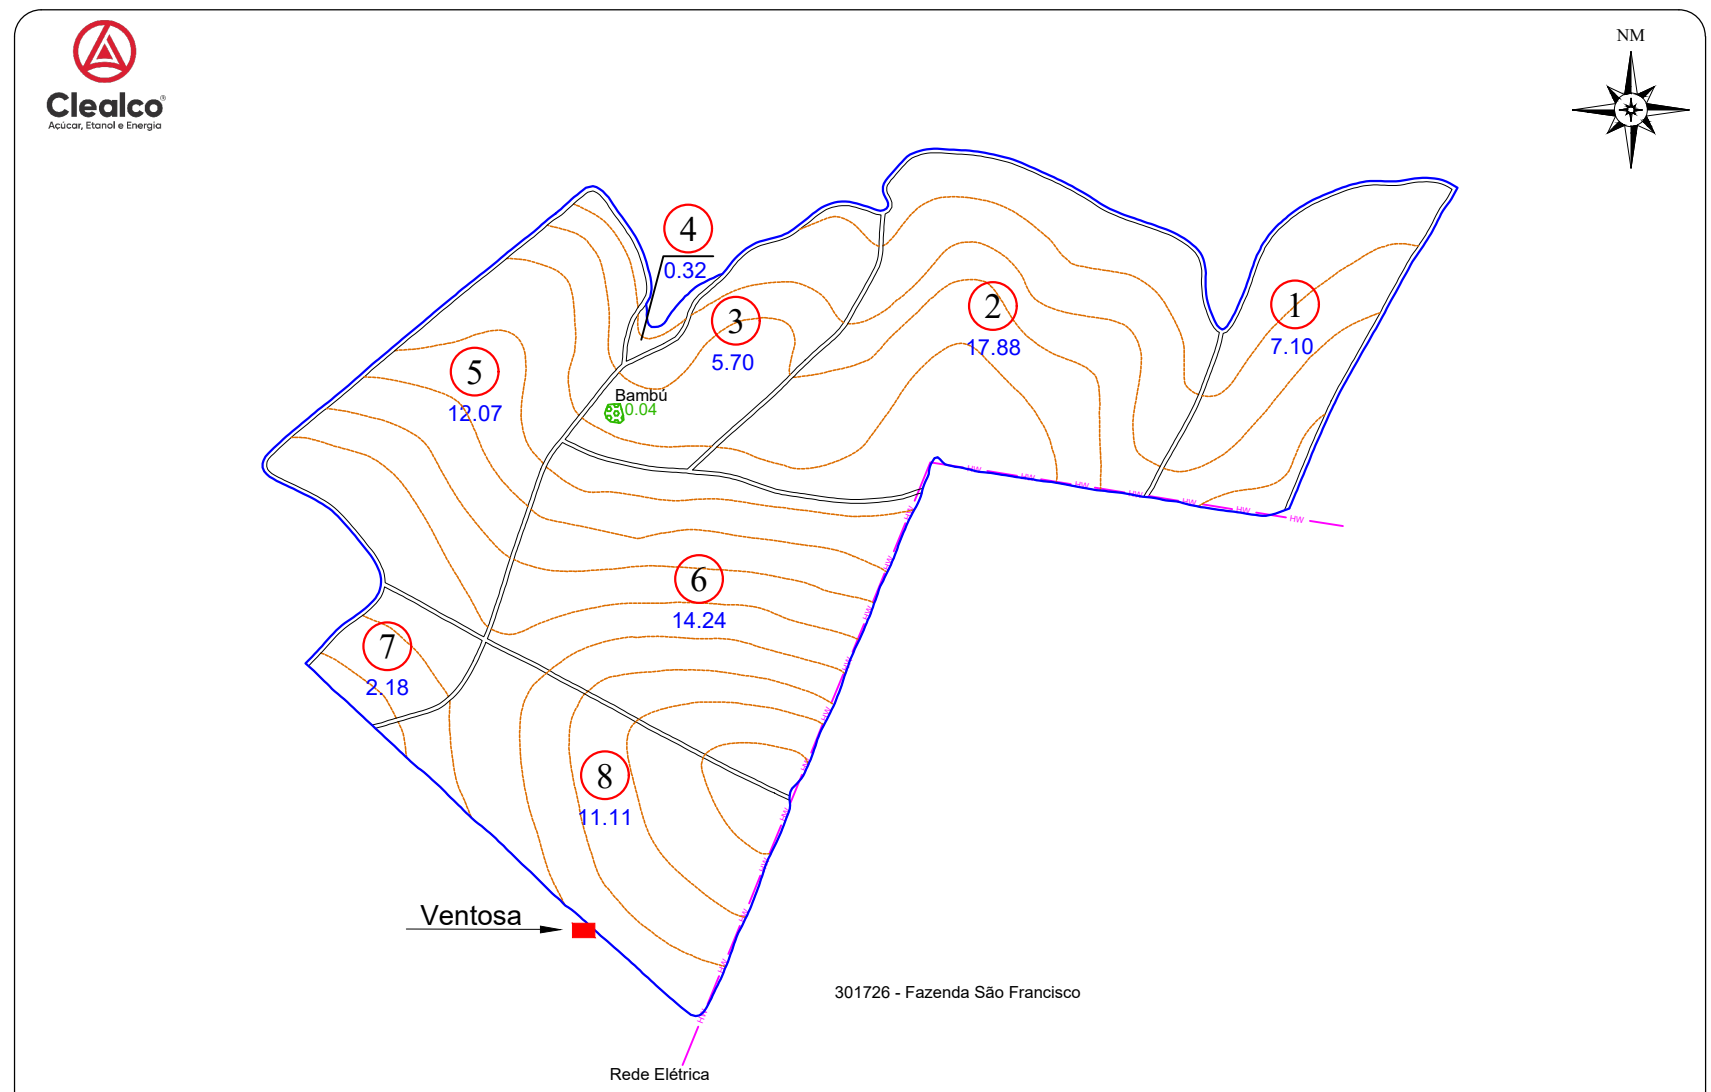

CROQUI DE ACESSO

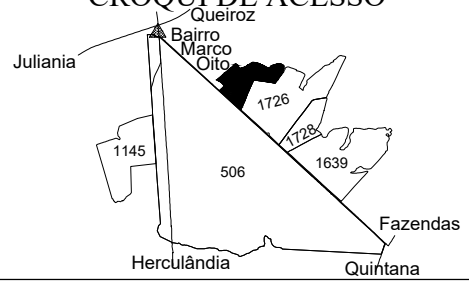

SÍTIO SÃO JOÃO

PROPRIETÁRIO: FELIPE DE F. FERRAZ
COMPRADOR: CLEALCO S/A
MUNICÍPIO: QUEIROZ

DISTÂNCIAS (km):
UNID. I - Asfalto: 69.00 Terra.: 3.00
UNID.I I - Asfalto: 16.00 Terra.: 4.00
UNID. III -Asfalto: 69.10 Terra.: 3.00

COORDENADAS: E(X): 571564.5360 N(Y): 7579949.763
LAT: 21º 52' 59.1967" LONG: 50º 18' 26.1496"

CLEALCO - AÇÚCAR E ALCOOL S/A - DEPARTAMENTO DE TOPOGRAFIA

UNIDADE: II
PARTE: A/A
FUNDO AGRÍCOLA: 301729

M:\01-Mapa de safra\Mapas Atualizados\Spot\301729 - Sítio São João (Felipe de Figueiredo Ferraz)\301729 - Sítio São João (Felipe de Figueiredo Ferraz).dwg