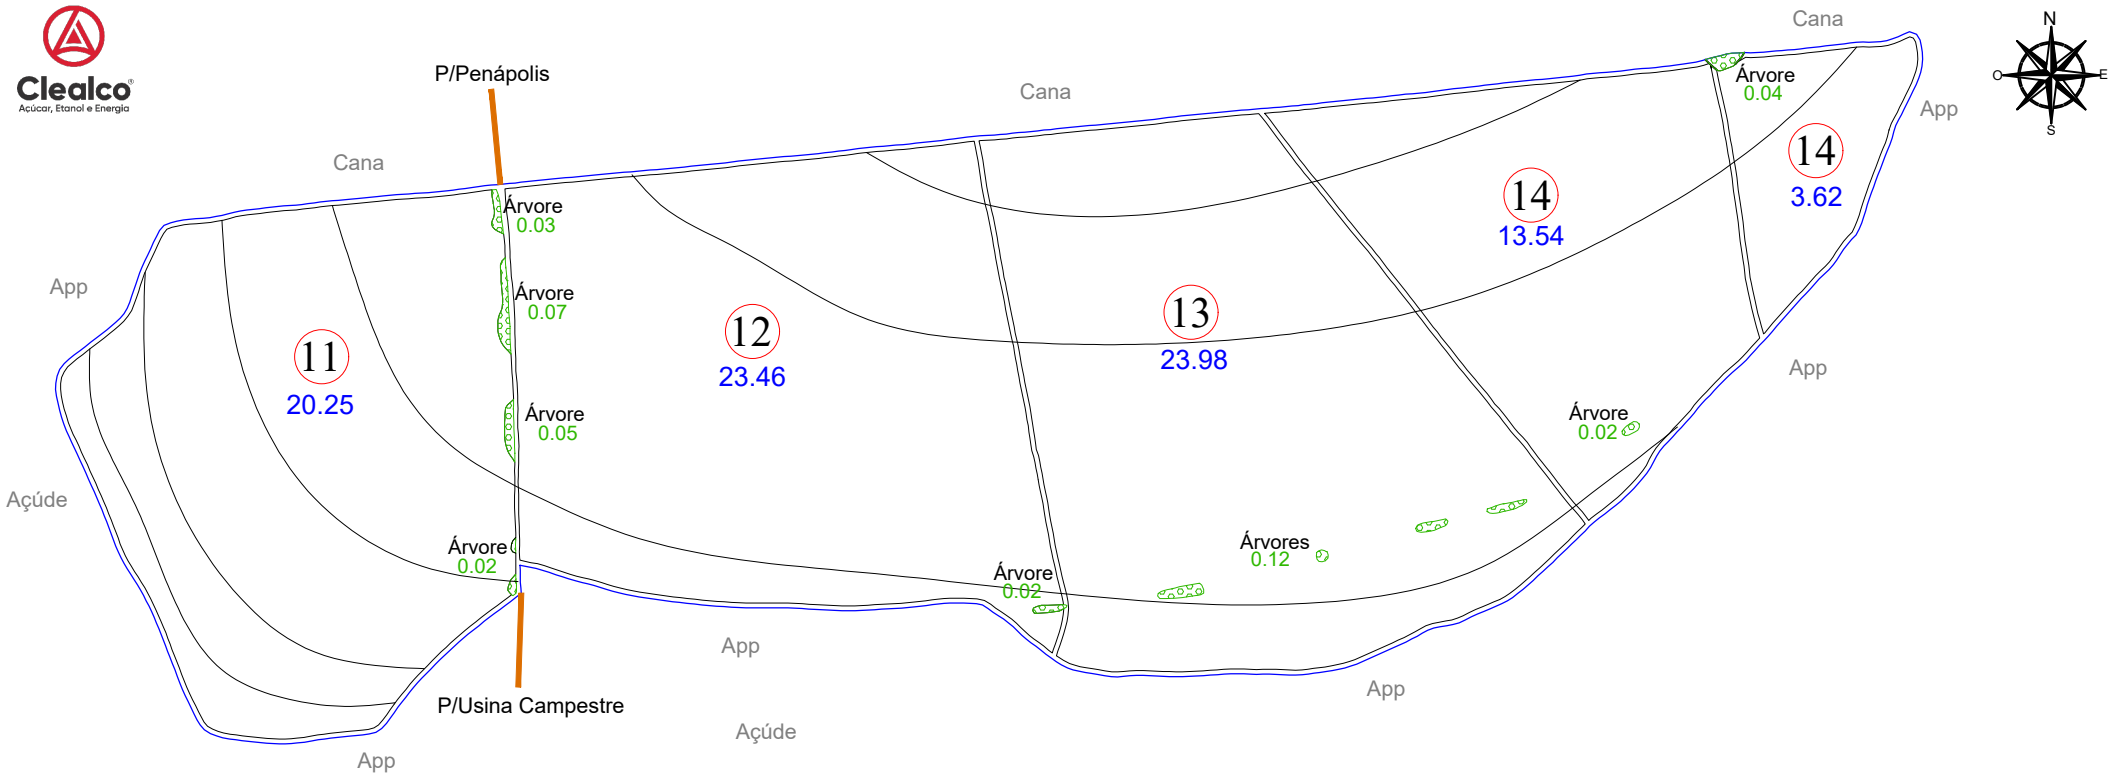


ÁREAS	(ha)	(%)
PLANTIO	84.85	95.99
CARREADORES	3.17	3.59
OUTROS	0.00	0.00
SUB TOTAL AGRICULTÁVEL	88.02	99.58
AP.P.	0.00	0.00
ÁRVORES	0.37	0.42
OUTROS	0.00	0.00
SUB TOTAL NÃO AGRICULT.	0.37	0.42
ÁREA TOTAL	88.39	100.00

C. NÍVEL: 5501.63 m/l 1.27 ha 1.43 %

Nº TAL.	DATA PL.	ÁREA (ha)	VARIEDADE
11	05/2021	20.25	CTC4
12	05/2022	23.46	RB965242
13		23.98	
14		17.16	
TOTAL PLANTIO		84.85	


ESCALA: 1: 8.000

LEGENDA

- FAZENDA
- TALHÃO
- REDE ELÉTRICA
- TERRAÇO BASE LARGA
- TERRAÇO EMBUTIDO

ESPAÇAMENTO: 1.50 x 1.50
TIRO MÉDIO ESTIMADO: 614.80 m
D.V: 4.08 %

CROQUI DE ACESSO

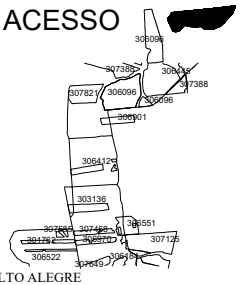

FAZENDA CAMPESTRE

PROPRIETÁRIO: WILLIAN ÁVILA P. E OUTRO
COMPRADOR: CLEALCO
MUNICÍPIO: PENÁPOLIS - SP

DISTÂNCIAS (km):
UNID. I - Asfalto: 60.70 Terra.: 2.50
UNID.I I - Asfalto: 49.50 Terra.: 2.50

COORDENADAS: E(X): 591656.85 N(Y): 7625588.28
LAT: -21°28'11.5915" LONG: -50°6'55.1082"

CLEALCO - AÇÚCAR E ALCOOL S/A - DEPARTAMENTO DE GEOTECNOLOGIA

LEVANTAMENTO VIA:
SATÉLITE
GPS / VANT
GOOGLE

UNIDADE: I
PARTE: C/C
FUNDO AGRÍCOLA: 306096

M:\01-Mapa de safra\Mapas Atualizados\Spot\306096 - Fazenda Campestre (Willian Ávila)\306096 C - Fazenda Campestre (Willian Ávila).dwg

Bruno Gamboa 28/08/26