
Clealco
Açúcar, Etanol e Energia

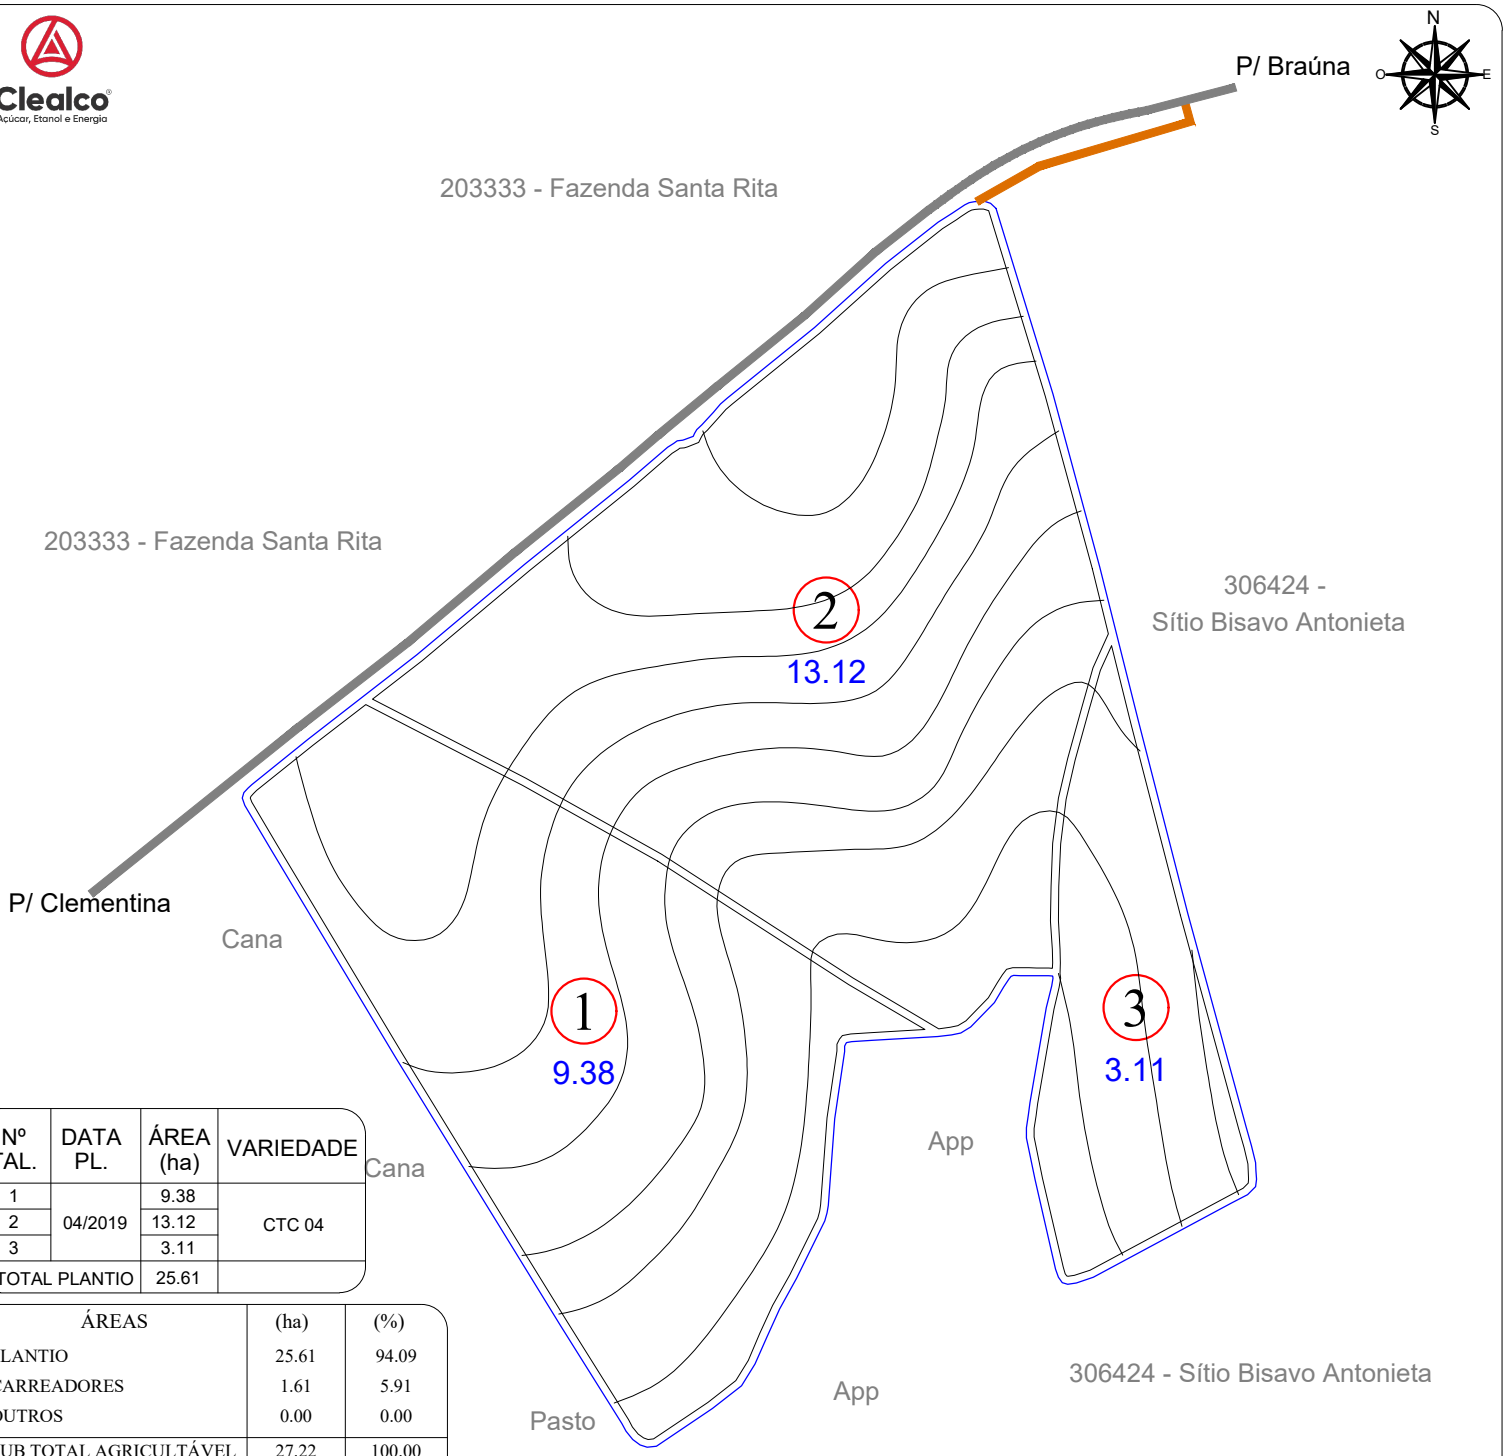

Nº TAL.	DATA PL.	ÁREA (ha)	VARIEDADE
1	04/2019	9.38	CTC 04
2		13.12	
3		3.11	
TOTAL PLANTIO		25.61	

ÁREAS	(ha)	(%)
PLANTIO	25.61	94.09
CARREADORES	1.61	5.91
OUTROS	0.00	0.00
SUB TOTAL AGRICULTÁVEL	27.22	100.00
AP.P.	0.00	0.00
ÁRVORES	0.00	0.00
OUTROS	0.00	0.00
SUB TOTAL NÃO AGRICULT.	0.00	0.00
ÁREA TOTAL	27.22	100.00

C. NÍVEL: 5459.23 m/l 1.26 ha 4.61 %


LEGENDA

- FAZENDA
- TALHÃO
- REDE ELÉTRICA
- VAZIO
- TERRAÇO BASE LARGA
- TERRAÇO EMBUTIDO
- (P.O.A) PATIO DE OPERAÇÃO
- CARREGADO

ESPAÇAMENTO: 1.50 x 1.50
TIRO MÉDIO ESTIMADO: 212.00 m
D.V: 5.47 %

ESCALA: 1: 5.000

CROQUI DE ACESSO

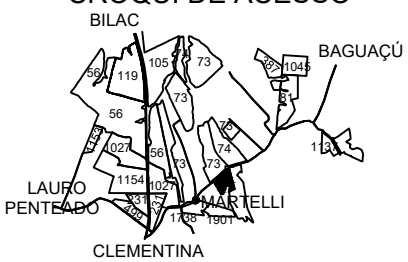

SÍTIO 4 IRMAOS

PROPRIETÁRIO: MARIA ANGELA P. MAROTA
COMPRADOR: CLEALCO
MUNICÍPIO: CLEMENTINA - SP

DISTÂNCIAS (km):
UNID. I - Asfalto: 10.00 Terra.: 0.00
UNID.I I - Asfalto: 69.50 Terra.: 1.00

COORDENADAS: E(X): 561411.61 N(Y): 7621711.71
LAT: -21°30'22.3181" LONG: -50°24'25.5058"

CLEALCO - AÇÚCAR E ALCOOL S/A - DEPARTAMENTO DE GEOTECNOLOGIA

LEVANTAMENTO VIA:
- SATÉLITE
- GPS / VANT
- GOOGLE

UNIDADE: I
PARTE: A/A
FUNDO AGRÍCOLA: 306601

M:\01-Mapa de safra\Mapas Atualizados\Terceiro\306601 - Sitio 04 Irmaos (Maria Angela Polachini Marotta)\306601 - Sitio 04 Irmaos (Maria Angela Polachini Marotta).dwg

Bruno Gamboa 15/04/26