D.V.	Nº TAL.	DATA PL.	ÁREA (ha)	VARIEDADE
4.41 %	1	04/2025	35.84	RB97 5242
TOTAL PLANTIO			35.84	--------


ÁREAS	(ha)	(%)
PLANTIO	35.84	95.75
CARREADORES	1.59	4.25
OUTROS	0.00	0.00
SUB TOTAL AGRICULTÁVEL	37.43	100.00
AP.P.	0.00	0.00
ÁRVORES	0.00	0.00
OUTROS	0.00	0.00
SUB TOTAL NÃO AGRICULT.	0.00	0.00
ÁREA TOTAL	37.43	100.00

C. NÍVEL: 4364.73 m/l 1.00 ha 2.68 %

LEGENDA


- FAZENDA
- TALHÃO
- CURVA DE NÍVEL
- CARREADOR
- CONFRONTANTE
- REDE ELÉTRICA
- TRAJETO VAZIO
- TRAJETO CARREGADO

PLANTIO MANUAL - ESPAÇAMENTO: 1.50 X 1.50
TIRO MÉDIO ESTIMADO: 249.72 m

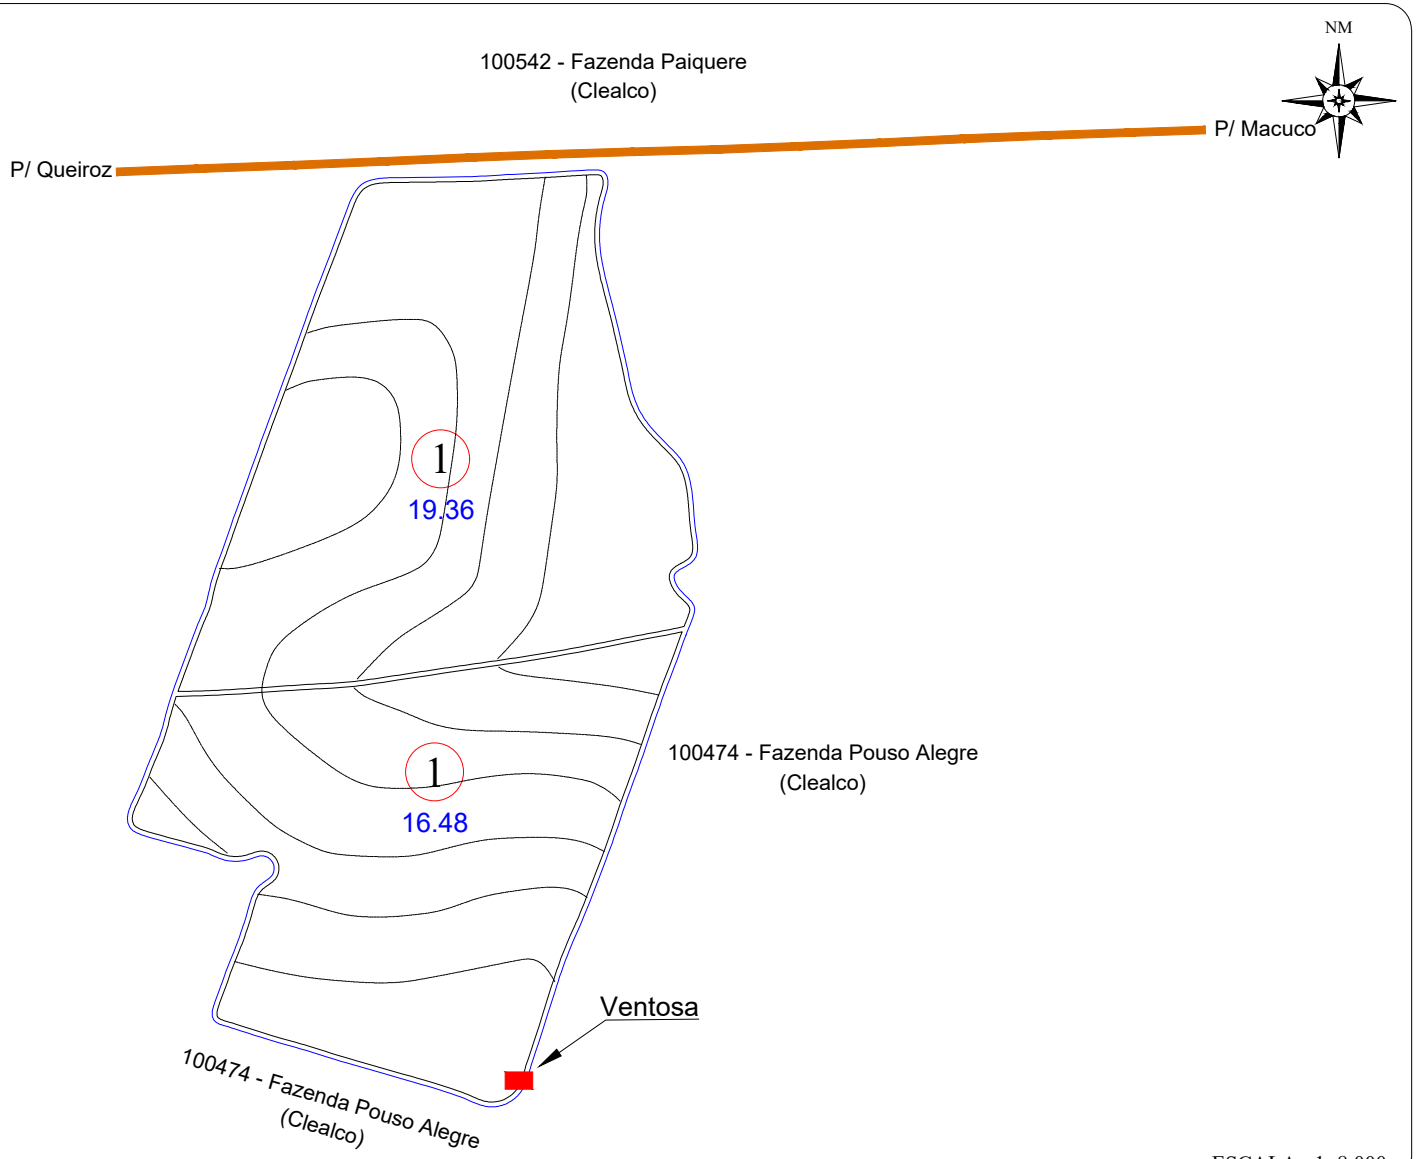

ESCALA: 1: 8.000

CROQUI DE ACESSO

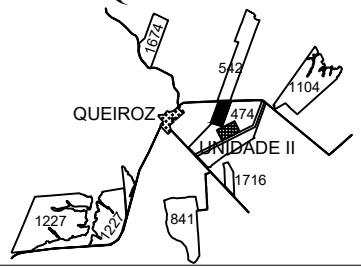

SÍTIO NOSSA SENHORA APARECIDA

PROPRIETÁRIO: MARCO F. BORRS FILHO
COMPRADOR: CLEALCO S/A
MUNICÍPIO: QUEIROZ

DISTÂNCIAS (km):

UNID. I - Asfalto:	53.00	Terra.:	1.00
UNID.I I - Asfalto:	4.50	Terra.:	1.00
UNID. III -Asfalto:	55.00	Terra.:	1.00

COORDENADAS: E(X): 580527.62 N(Y): 7589337.06
LAT: -21°47'52.5065" LONG: -50°13'15.4832"

CLEALCO - AÇÚCAR E ALCOOL S/A - DEPARTAMENTO DE TOPOGRAFIA

UNIDADE: II

PARTE: A/B

FUNDO AGRÍCOLA: 307497

M:\01-Mapa de safra\Mapas Atualizados\Spot\307497 - Sítio Nossa Senhora Aparecida (Marco F. Borrs Filho)\307497 A - Sítio Nossa Senhora Aparecida (Marco F. Borrs Filho).dwg

Bruno Gamboa 21/05/25