D.V.	Nº TAL.	DATA PL.	ÁREA (ha)	VARIEDADE
4.41 %	2	04/2025	34.01	CTC 9001
TOTAL PLANTIO			34.01	--------

ÁREAS	(ha)	(%)
PLANTIO	34.01	95.69
CARREADORES	1.53	4.31
OUTROS	0.00	0.00
SUB TOTAL AGRICULTÁVEL	35.54	100.00
AP.P.	0.00	0.00
ÁRVORES	0.00	0.00
OUTROS	0.00	0.00
SUB TOTAL NÃO AGRICULT.	0.00	0.00
ÁREA TOTAL	35.54	100.00

C. NÍVEL: 4984.04 m/l 1.15 ha 3.23 %

LEGENDA

- ▬ FAZENDA
- ▬ TALHÃO
- ▪▪▪ CURVA DE NÍVEL
- — CARREADOR
- ▬ CONFRONTANTE
- -·- REDE ELÉTRICA
- —▷ TRAJETO VAZIO
- —▶ TRAJETO CARREGADO

PLANTIO MANUAL - ESPAÇAMENTO: 1.50 X 1.50
TIRO MÉDIO ESTIMADO: 215.74 m

Clealco
Açúcar, Etanol e Energia

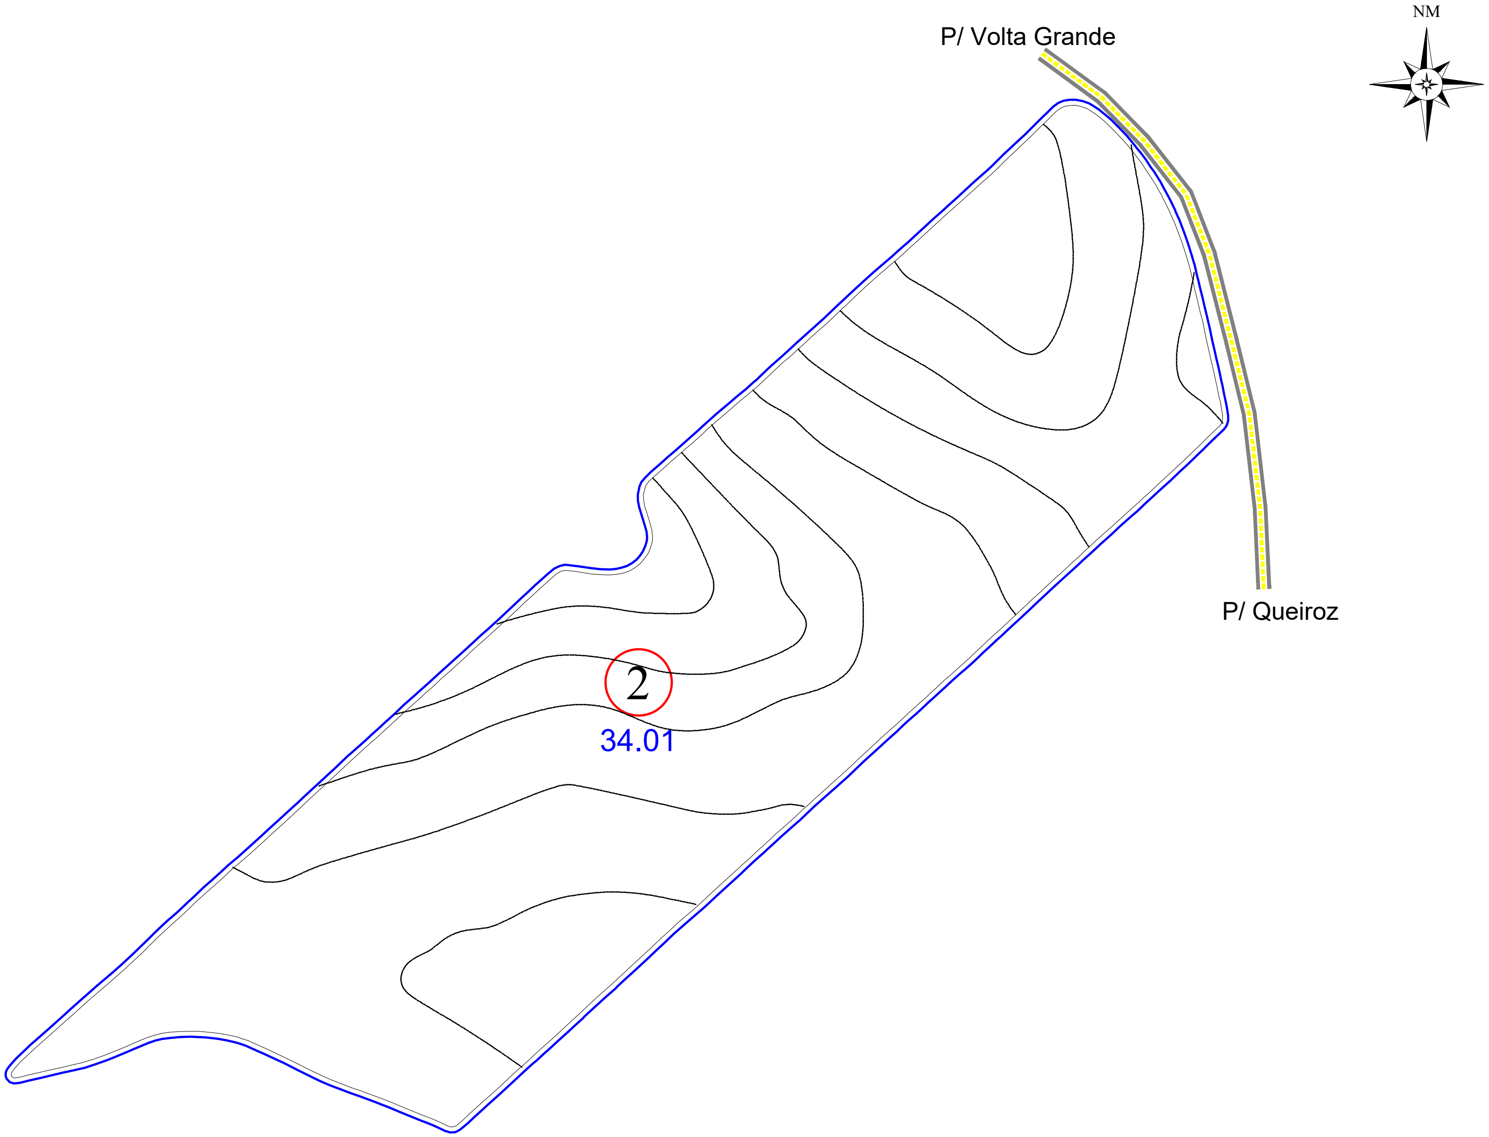

ESCALA: 1: 7.000

CROQUI DE ACESSO

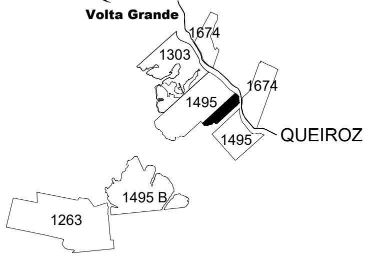

SÍTIO NOSSA SENHORA APARECIDA

PROPRIETÁRIO:	MARCO F. BORRS FILHO
COMPRADOR:	CLEALCO S/A
MUNICÍPIO:	QUEIROZ

DISTÂNCIAS (km):

UNID. I - Asfalto:	48.50	Terra.:	0.00
UNID.I I - Asfalto:	11.70	Terra.:	0.00
UNID. III -Asfalto:	45.50	Terra.:	0.00

COORDENADAS: E(X):	576847.59	N(Y):	7591929.67
LAT:	-21°46'28.7790"	LONG:	-50°15'24.0733"

CLEALCO - AÇÚCAR E ALCOOL S/A - DEPARTAMENTO DE TOPOGRAFIA

UNIDADE:
II

PARTE:
B/B

FUNDO AGRÍCOLA:
307497