ZONA D.V.	Nº TAL.	DATA PL.	ÁREA (ha)	VARIEDADE
999 4.46 %	1	06/2023	15.88	RB 975201
TOTAL PLANTIO			15.88	--------

ÁREAS	(ha)	(%)
PLANTIO	15.88	92.18
CARREADORES	1.28	7.42
OUTROS	0.00	0.00
SUB TOTAL AGRICULTÁVEL	17.16	99.59
AP.P.	0.00	0.00
ÁRVORES	0.01	0.06
OUTROS	0.06	0.35
SUB TOTAL NÃO AGRICULT.	0.07	0.41
ÁREA TOTAL	17.23	100.00

C. NÍVEL:	0.00 m/l	0.00 ha	0.00 %

LEGENDA

▬ FAZENDA	▬ CONFRONTANTE
▬ TALHÃO	-·- REDE ELÉTRICA
▪▪▪ CURVA DE NÍVEL	—▷ TRAJETO VAZIO
— CARREADOR	—▶ TRAJETO CARREGADO

PLANTIO MANUAL - ESPAÇAMENTO: 1.50 X 1.50
TIRO MÉDIO ESTIMADO: 121.45 m

Clealco
Açúcar, Etanol e Energia

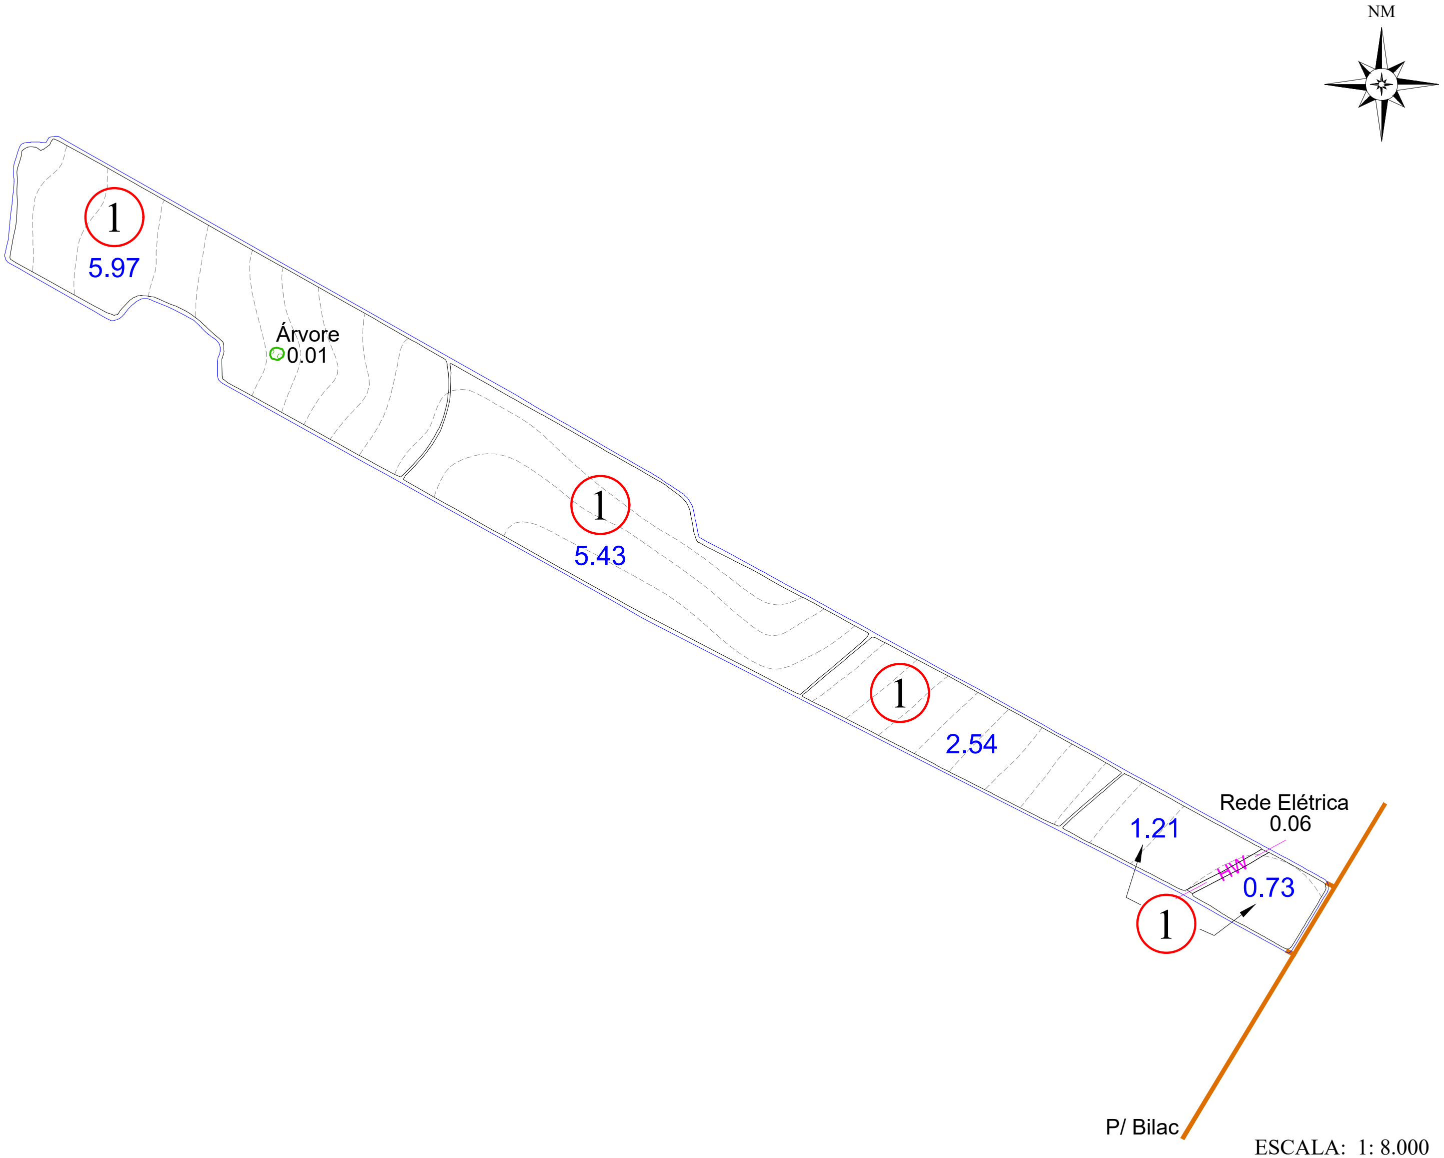
NM
1
5.97
Árvore
0.01
1
5.43
1
2.54
1.21
Rede Elétrica
0.06
0.73
1
P/ Bilac

ESCALA: 1: 8.000

CROQUI DE ACESSO

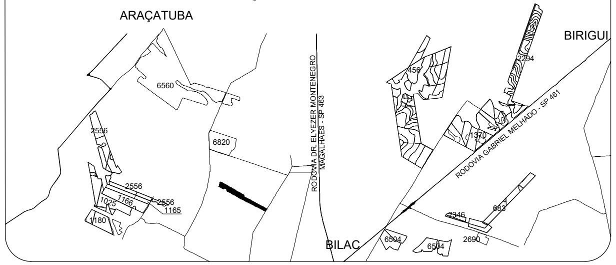
ARAÇATUBA
BIRIGUI
6560
2556
6820
2556
1025
1166
2556
1165
1180
RODOVIA DR. ELYEZER MONTENEGRO MAGALHAES - SP 463
456
2294
1370
RODOVIA GABRIEL MELHADO - SP 461
2346
683
BILAC
6504
6504
2690

SITIO JRS III

PROPRIETÁRIO:	LUIZ CARLOS GENARI
COMPRADOR:	CLEALCO S/A
MUNICÍPIO:	BILAC

DISTÂNCIAS (km):

	Asfalto:		Terra.:	
UNID. I -	Asfalto:	24.30	Terra.:	8.30
UNID.I I -	Asfalto:	80.10	Terra.:	8.30
UNID. III -	Asfalto:	65.00	Terra.:	5.00

COORDENADAS:

E(X):	553527.91	N(Y):	7637408.56
LAT:	-21°21'52.6834"	LONG:	-50°29'1.3084"

CLEALCO - AÇÚCAR E ALCOOL S/A - DEPARTAMENTO DE TOPOGRAFIA

UNIDADE:
I

PARTE:
A/A

FUNDO AGRÍCOLA:
307505

M:\03-Projetos (Sistematização, Pré, Pós e outros)\Terceiro\2023\Edvaldo\Pós Plantio\307505 - Sítio Jrs III (Luiz Carlos Genari) Pós Plantio -2023.dwg

Bruno Gamboa 19/12/23