D.V.	Nº TAL.	DATA PL.	ÁREA (ha)	VARIEDADE
4.43%	1	04/2023	12.33	RB 975242
	2	05/2024	10.42	
	3	04/2020	6.95	CTC 04
	4	04/2022	7.91	
TOTAL PLANTIO			37.61	

ÁREAS	(ha)	(%)
PLANTIO	37.61	96.19
CARREADORES	1.49	3.81
OUTROS	0.00	0.00
SUB TOTAL AGRICULTÁVEL	39.10	100.00
AP.P.	0.00	0.00
ÁRVORES	0.00	0.00
OUTROS	0.00	0.00
SUB TOTAL NÃO AGRICULT.	0.00	0.00
ÁREA TOTAL	39.10	100.00


C. NÍVEL: 6387.95 m/l 1.47 ha 3.76 %

LEGENDA

- FAZENDA
- TALHÃO
- REDE ELÉTRICA
- TERRAÇO BASE LARGA
- TERRAÇO EMBUTIDO


ESPAÇAMENTO: 1.50 x 1.50

TIRO MÉDIO ESTIMADO: 171.28 m

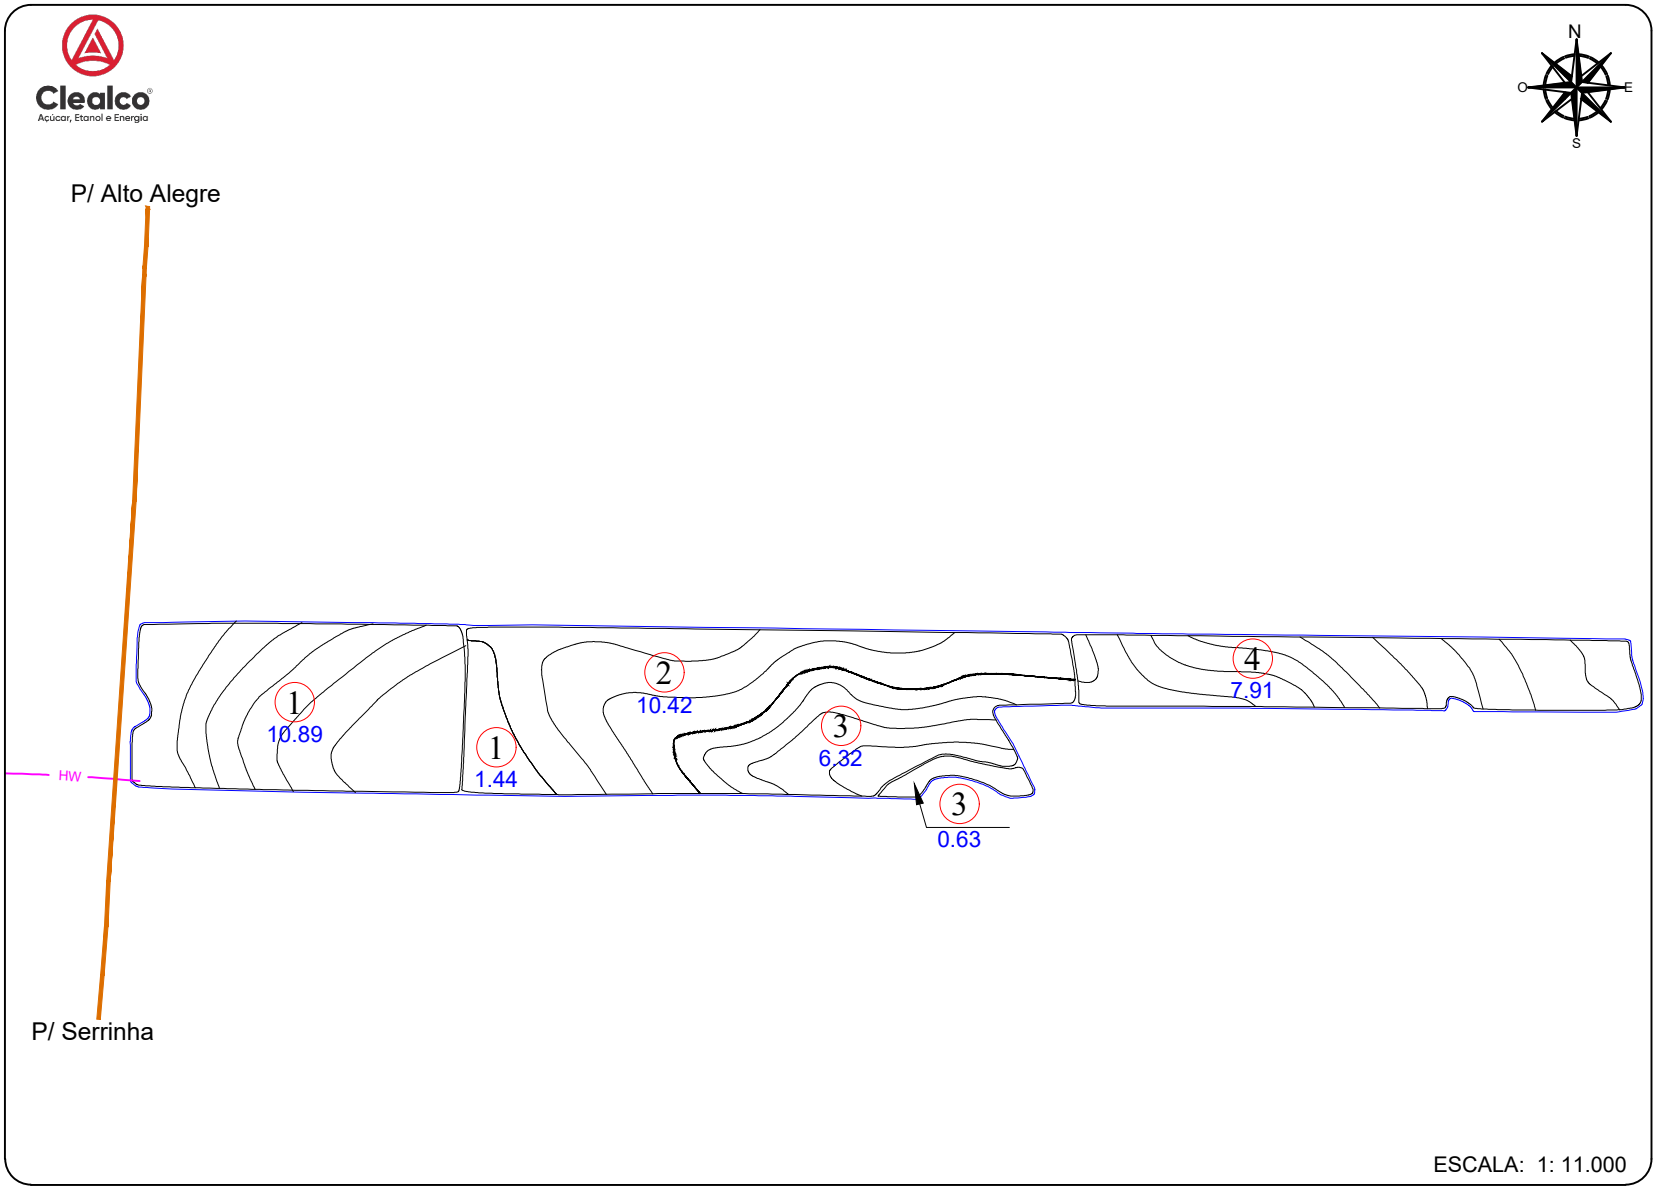

ESCALA: 1: 11.000

CROQUI DE ACESSO

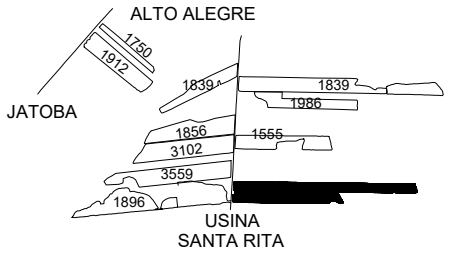

SÍTIO SÃO PEDRO

PROPRIETÁRIO: FATIMA MARIA LAGUNA MACHADO

COMPRADOR: CLEALCO S/A

MUNICÍPIO: ALTO ALEGRE - SP

DISTÂNCIAS (km):

UNID. I - Asfalto: 59.00 Terra.: 3.00

UNID.I I - Asfalto: 39.00 Terra.: 3.00

UNID. III -Asfalto: 16.00 Terra.: 3.00

COORDENADAS: E(X): 586564.56 N(Y): 7609281.08

LAT: -21°37'2.8566" LONG: -50°9'49.0029"

CLEALCO - AÇÚCAR E ALCOOL S/A - DEPARTAMENTO DE GEOTECNOLOGIA

UNIDADE: II

PARTE: A/A

FUNDO AGRÍCOLA: 307906