
Clealco
Açúcar, Etanol e Energia

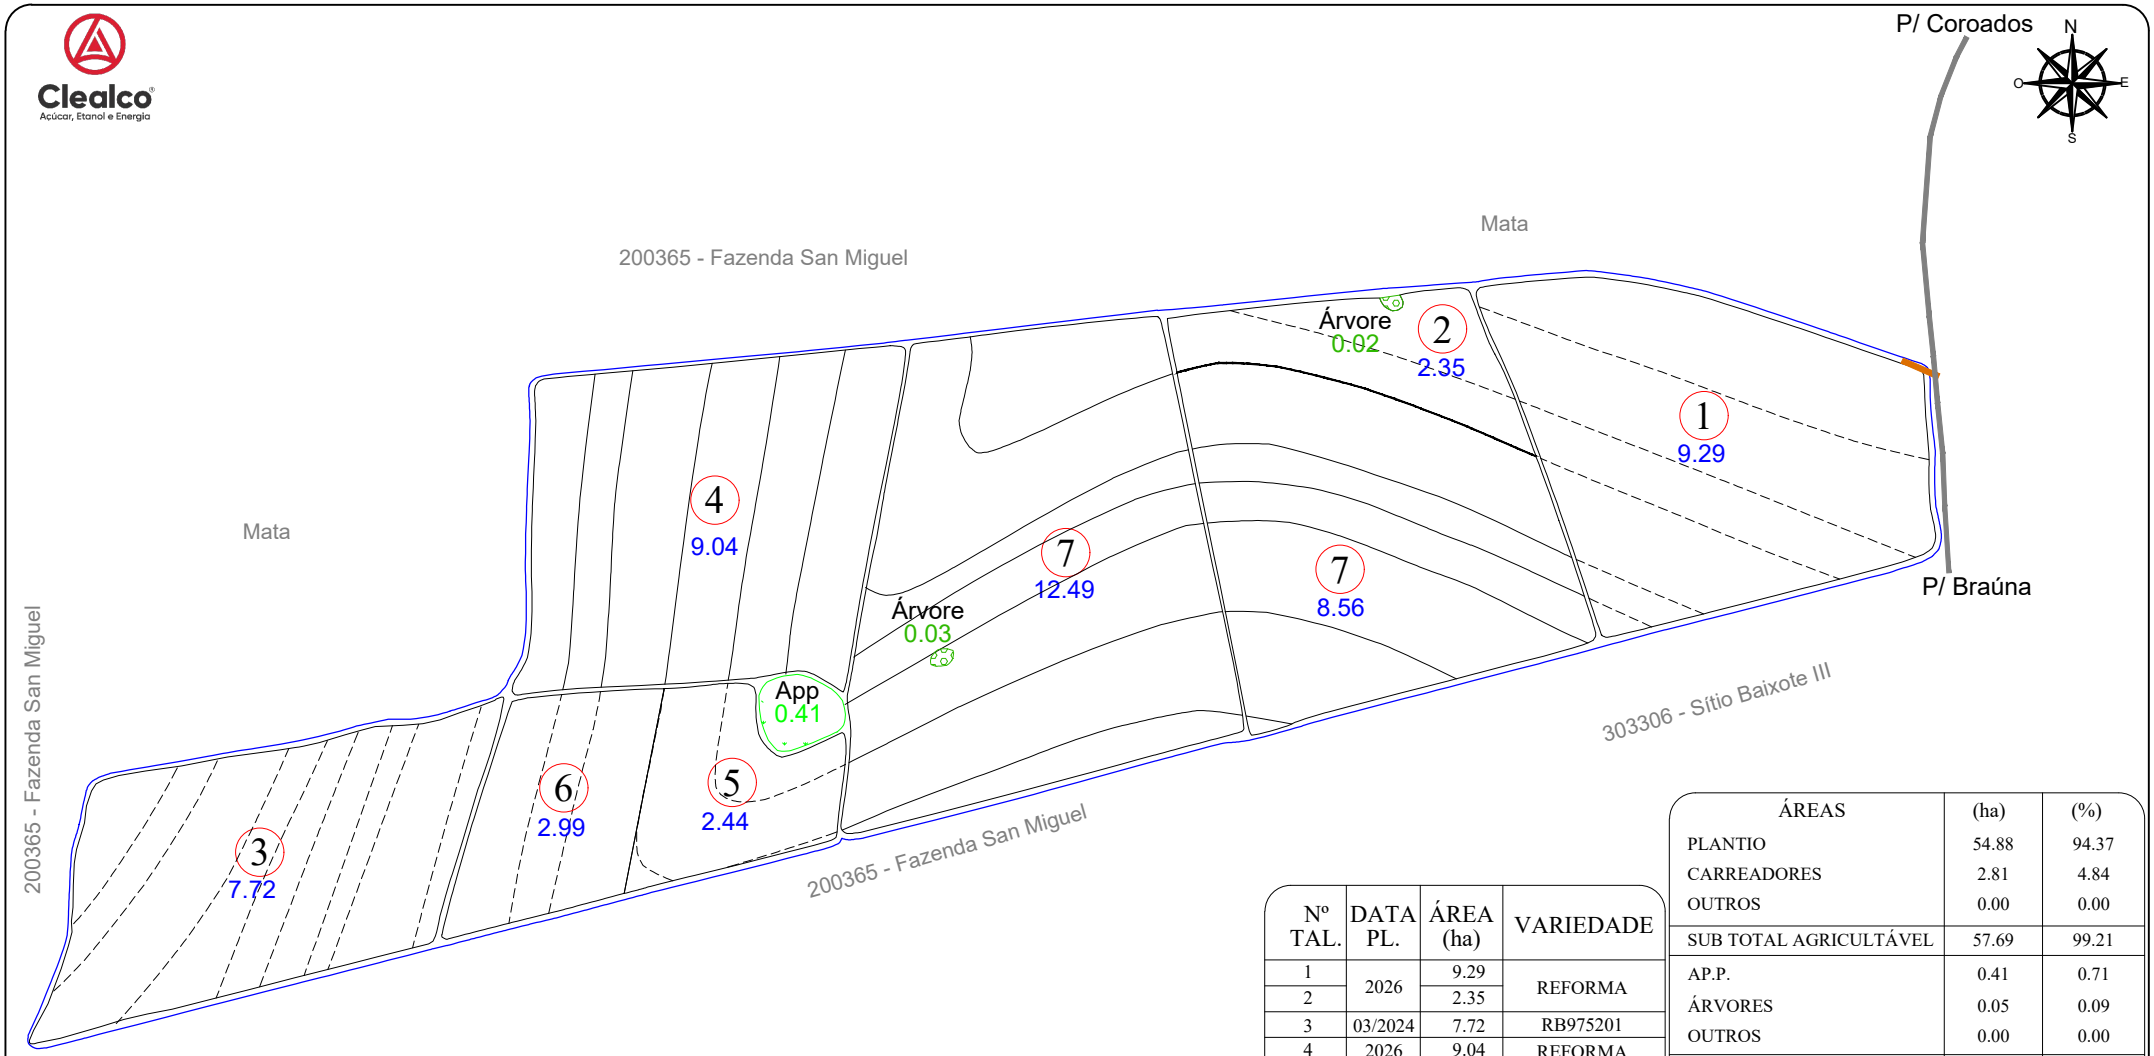

Nº TAL.	DATA PL.	ÁREA (ha)	VARIEDADE
1	2026	9.29	REFORMA
2		2.35	
3	03/2024	7.72	RB975201
4	2026	9.04	REFORMA
5	04/2025	2.44	IACSP01-5503
6		2.99	
7	2026	21.05	REFORMA
TOTAL PLANTIO		54.88	--------

ÁREAS	(ha)	(%)
PLANTIO	54.88	94.37
CARREADORES	2.81	4.84
OUTROS	0.00	0.00
SUB TOTAL AGRICULTÁVEL	57.69	99.21
AP.P.	0.41	0.71
ÁRVORES	0.05	0.09
OUTROS	0.00	0.00
SUB TOTAL NÃO AGRICULT.	0.46	0.79
ÁREA TOTAL	58.15	100.00

C. NÍVEL:	5259.39 m/l	1.21 ha	2.08 %


ESCALA: 1: 7.000

LEGENDA

- FAZENDA
- TALHÃO
- REDE ELÉTRICA
- TERRAÇO BASE LARGA
- TERRAÇO EMBUTIDO

ESPAÇAMENTO:	1.50 x 1.50	D.V: 4.92 %
TIRO MÉDIO ESTIMADO:	309.73 m	

CROQUI DE ACESSO

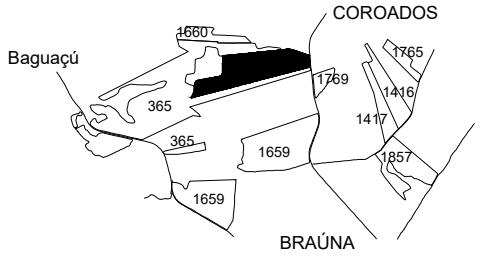

SÍTIO BAIXOTE

PROPRIETÁRIO:	ALESSANDRA G. MAROLATO
COMPRADOR:	CLEALCO
MUNICÍPIO:	COROADOS - SP

DISTÂNCIAS (km):
UNID. I - Asfalto: 21.00 Terra.: 0.00
UNID.I I - Asfalto: 75.00 Terra.: 0.00

COORDENADAS: E(X): 569652.94 N(Y): 7626176.52
LAT: -21°27'56.0187" LONG: -50°19'39.7416"

CLEALCO - AÇÚCAR E ALCOOL S/A - DEPARTAMENTO DE GEOTECNOLOGIA

LEVANTAMENTO VIA:
SATÉLITE
GPS / VANT
GOOGLE

UNIDADE: I

PARTE: A/A

FUNDO AGRÍCOLA: 308133

M:\01-Mapa de safra\Mapas Atualizados\Spot\308133 - Sítio Baixote (Alessandra Garcia Marolato)\308133 - Sítio Baixote (Alessandra Garcia Marolato).dwg

Bruno Gamboa 10/06/26