
Clealco
Açúcar, Etanol e Energia

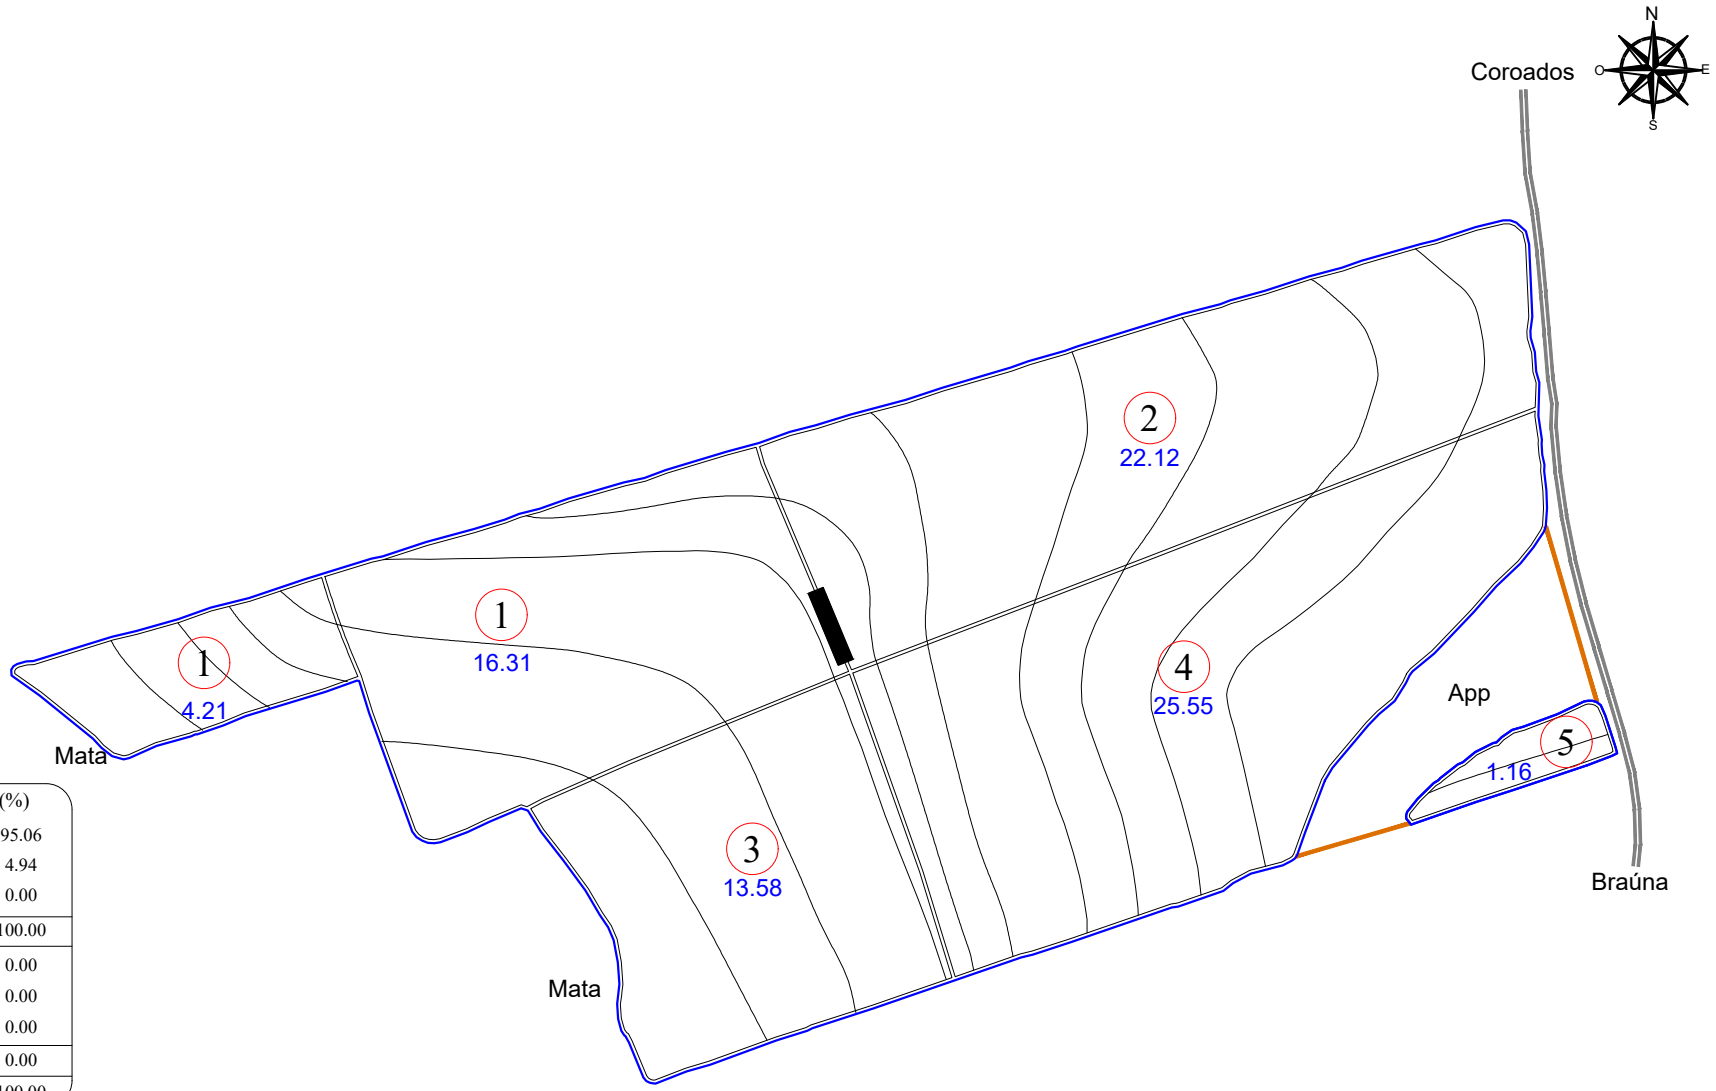

Nº TAL.	DATA PL.	ÁREA (ha)	VARIEDADE
1	04/2021	20.52	CTC 04
2		22.12	
3		13.58	
4		25.55	
5		1.16	
TOTAL PLANTIO		82.93	

ÁREAS	(ha)	(%)
PLANTIO	82.93	95.06
CARREADORES	4.31	4.94
OUTROS	0.00	0.00
SUB TOTAL AGRICULTÁVEL	87.24	100.00
AP.P.	0.00	0.00
ÁRVORES	0.00	0.00
OUTROS	0.00	0.00
SUB TOTAL NÃO AGRICULT.	0.00	0.00
ÁREA TOTAL	87.24	100.00

C. NÍVEL: 8112.06 m/l 1.87 ha 2.14 %


ESCALA: 1: 9.000

LEGENDA

- FAZENDA
- TALHÃO
- REDE ELÉTRICA
- TERRAÇO BASE LARGA
- TERRAÇO EMBUTIDO
- VAZIO
- CARREGADO

ESPAÇAMENTO: 1.50 x 1.50
TIRO MÉDIO ESTIMADO: 388.23 m
D.V: 3.35 %

CROQUI DE ACESSO

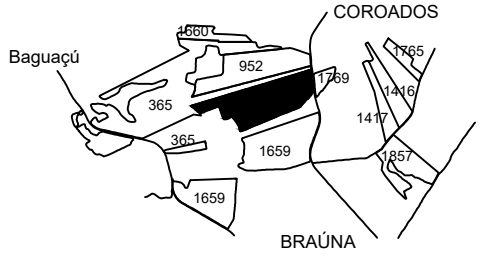

SÍTIO BAIXOTE III

PROPRIETÁRIO: ALESSANDRA G. MAROLATO
COMPRADOR: CLEALCO
MUNICÍPIO: COROADOS - SP

DISTÂNCIAS (km):
UNID. I - Asfalto: 28.20 Terra.: 0.50
UNID.I I - Asfalto: 75.00 Terra.: 0.50

COORDENADAS: E(X): 569579.50 N(Y): 7625704.52
LAT: -21°28'11.3802" LONG: -50°19'42.2228"

CLEALCO - AÇÚCAR E ALCOOL S/A - DEPARTAMENTO DE GEOTECNOLOGIA

LEVANTAMENTO VIA:
SATÉLITE
GPS / VANT
GOOGLE

UNIDADE: I
PARTE: A/A
FUNDO AGRÍCOLA: 308135

M:\01-Mapa de safra\Mapas Atualizados\Spot\308135 - Sítio Baixote III (Alessandra Garcia Marolato)\308135 - Sítio Baixote III (Alessandra Garcia Marolato).dwg

Bruno Gamboa 17/04/26