

Clealco
Açúcar, Etanol e Energia

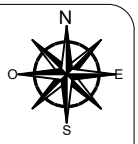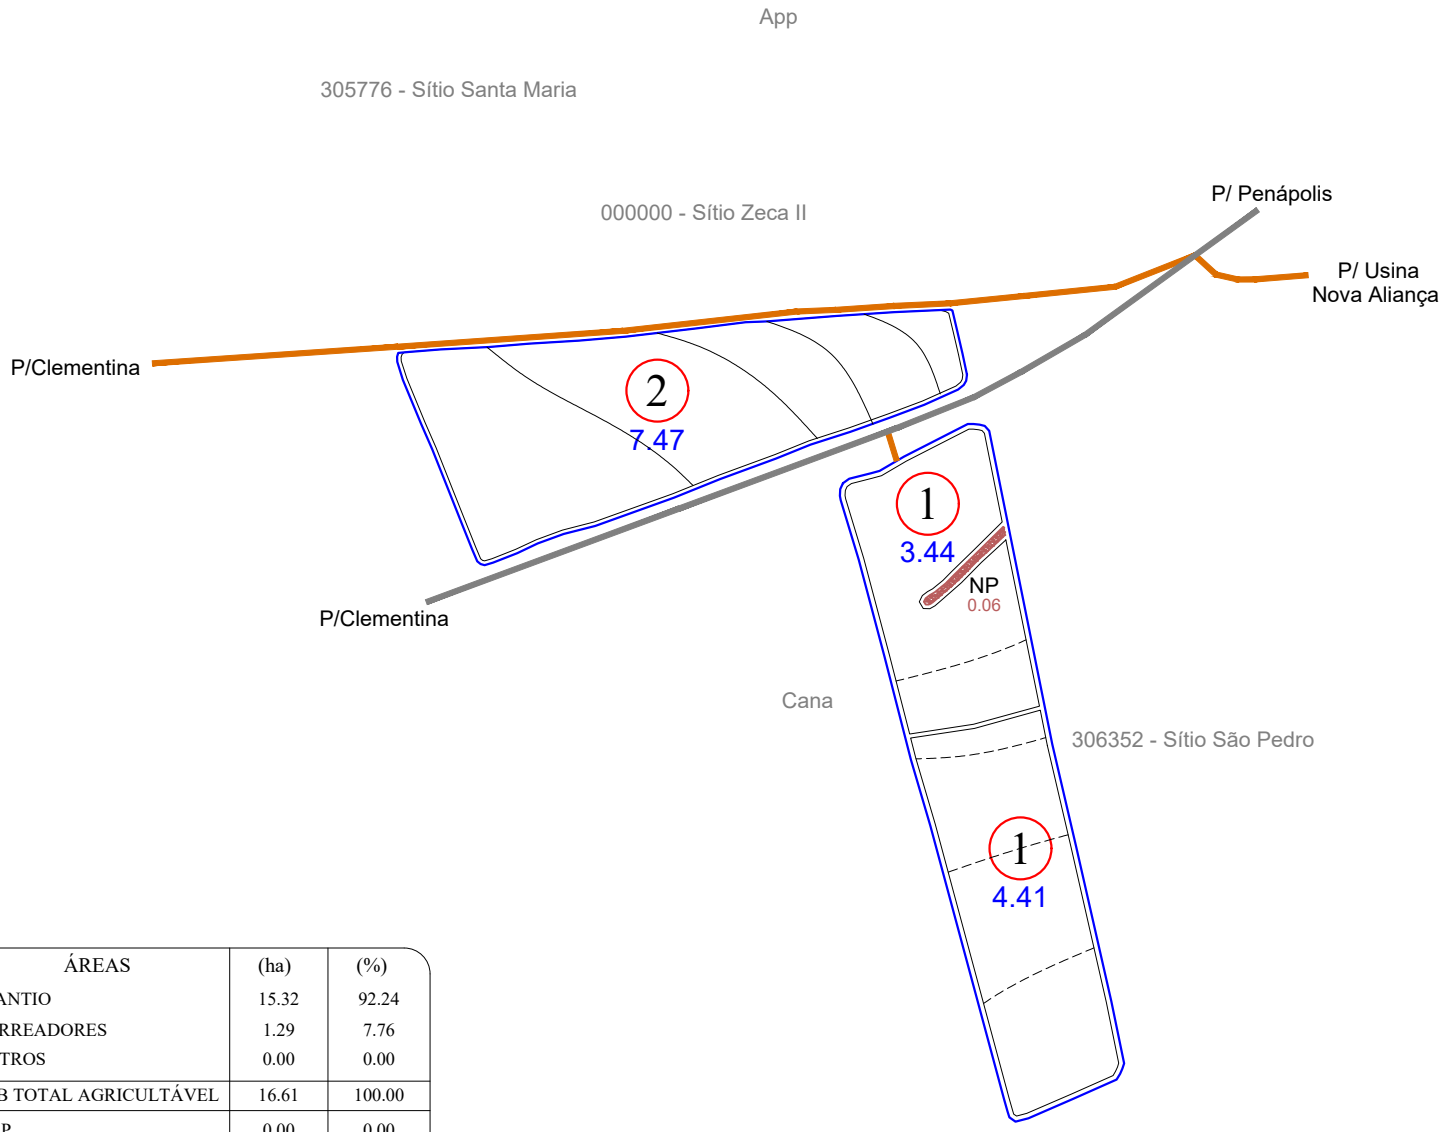


| ÁREAS | (ha) | (%) |
|---|---|---|
| PLANTIO | 15.32 | 92.24 |
| CARREADORES | 1.29 | 7.76 |
| OUTROS | 0.00 | 0.00 |
| SUB TOTAL AGRICULTÁVEL | 16.61 | 100.00 |
| AP.P. | 0.00 | 0.00 |
| ÁRVORES | 0.00 | 0.00 |
| OUTROS | 0.00 | 0.00 |
| SUB TOTAL NÃO AGRICULT. | 0.00 | 0.00 |
| ÁREA TOTAL | 16.61 | 100.00 |

| C. NÍVEL: | 695.50 m/l | 0.16 ha | 0.96 % |
|---|---|---|---|

LEGENDA

- FAZENDA
- TALHÃO
- REDE ELÉTRICA
- TERRAÇO BASE LARGA
- TERRAÇO EMBUTIDO
- (P.O.A) PATIO DE OPERAÇÃO

| ESPAÇAMENTO: | 1.50 x 1.50 | D.V: 3.85 % |
|---|---|---|
| TIRO MÉDIO ESTIMADO: | 214.18 m | |


(N.P)-NÃO PLANTOU

| TALHÃO | (ha) |
|---|---|
| 1 | 0.06 |
| | |
| | |
| Total | 0.06 |

| Nº TAL. | DATA PL. | ÁREA (ha) | VARIEDADE |
|---|---|---|---|
| 1 | 04/2021 | 7.85 | RB 975201 |
| 2 | | 7.47 | |
| | | | |
| TOTAL PLANTIO | | 15.32 | -------- |

ESCALA: 1: 7.500

CROQUI DE ACESSO

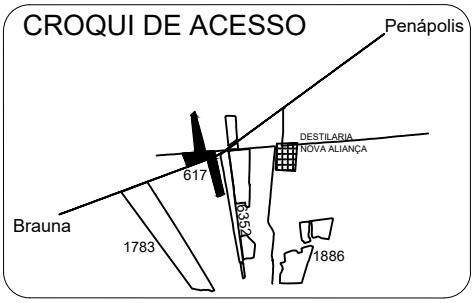


# SÍTIO DO ZECA I

PROPRIETÁRIO: MILENE GARBELINE
COMPRADOR: CLEALCO
MUNICÍPIO: PENÁPOLIS - SP

DISTÂNCIAS (km):
UNID. I - Asfalto: 30.00 Terra.: 2.80
UNID.I I - Asfalto: 69.00 Terra.: 2.80

COORDENADAS: E(X): 582058.96 N(Y): 7623742.72
LAT: -21°29'13.2872" LONG: -50°12'28.2655"
CLEALCO - AÇÚCAR E ALCOOL S/A - DEPARTAMENTO DE GEOTECNOLOGIA

LEVANTAMENTO VIA:
SATÉLITE
GPS / VANT
GOOGLE

UNIDADE: I
PARTE: A/A
FUNDO AGRÍCOLA: 308177

M:\01-Mapa de safra\Mapas Atualizados\Spot\308177 - Sitio do Zeca I (Milene Garbelini)\308177 - Sitio do Zeca I (Milene Garbelini).dwg

Bruno Gamboa 25/02/26