
Clealco
Açúcar, Etanol e Energia

Nº TAL.	DATA PL.	ÁREA (ha)	VARIEDADE
1	00/2021	22.67	RB 975201
2		4.01	
3		1.96	
4		6.94	
5		19.04	
6		13.10	
7	2026	7.32	REFORMA
TOTAL PLANTIO		75.04	

ÁREAS	(ha)	(%)
PLANTIO	75.04	94.20
CARREADORES	4.24	5.32
OUTROS	0.00	0.00
SUB TOTAL AGRICULTÁVEL	79.28	99.52
AP.P.	0.00	0.00
ÁRVORES	0.10	0.13
OUTROS	0.28	0.35
SUB TOTAL NÃO AGRICULT.	0.38	0.48
ÁREA TOTAL	79.66	100.00

C. NÍVEL: 10112.45 m/l 2.33 ha 2.92 %

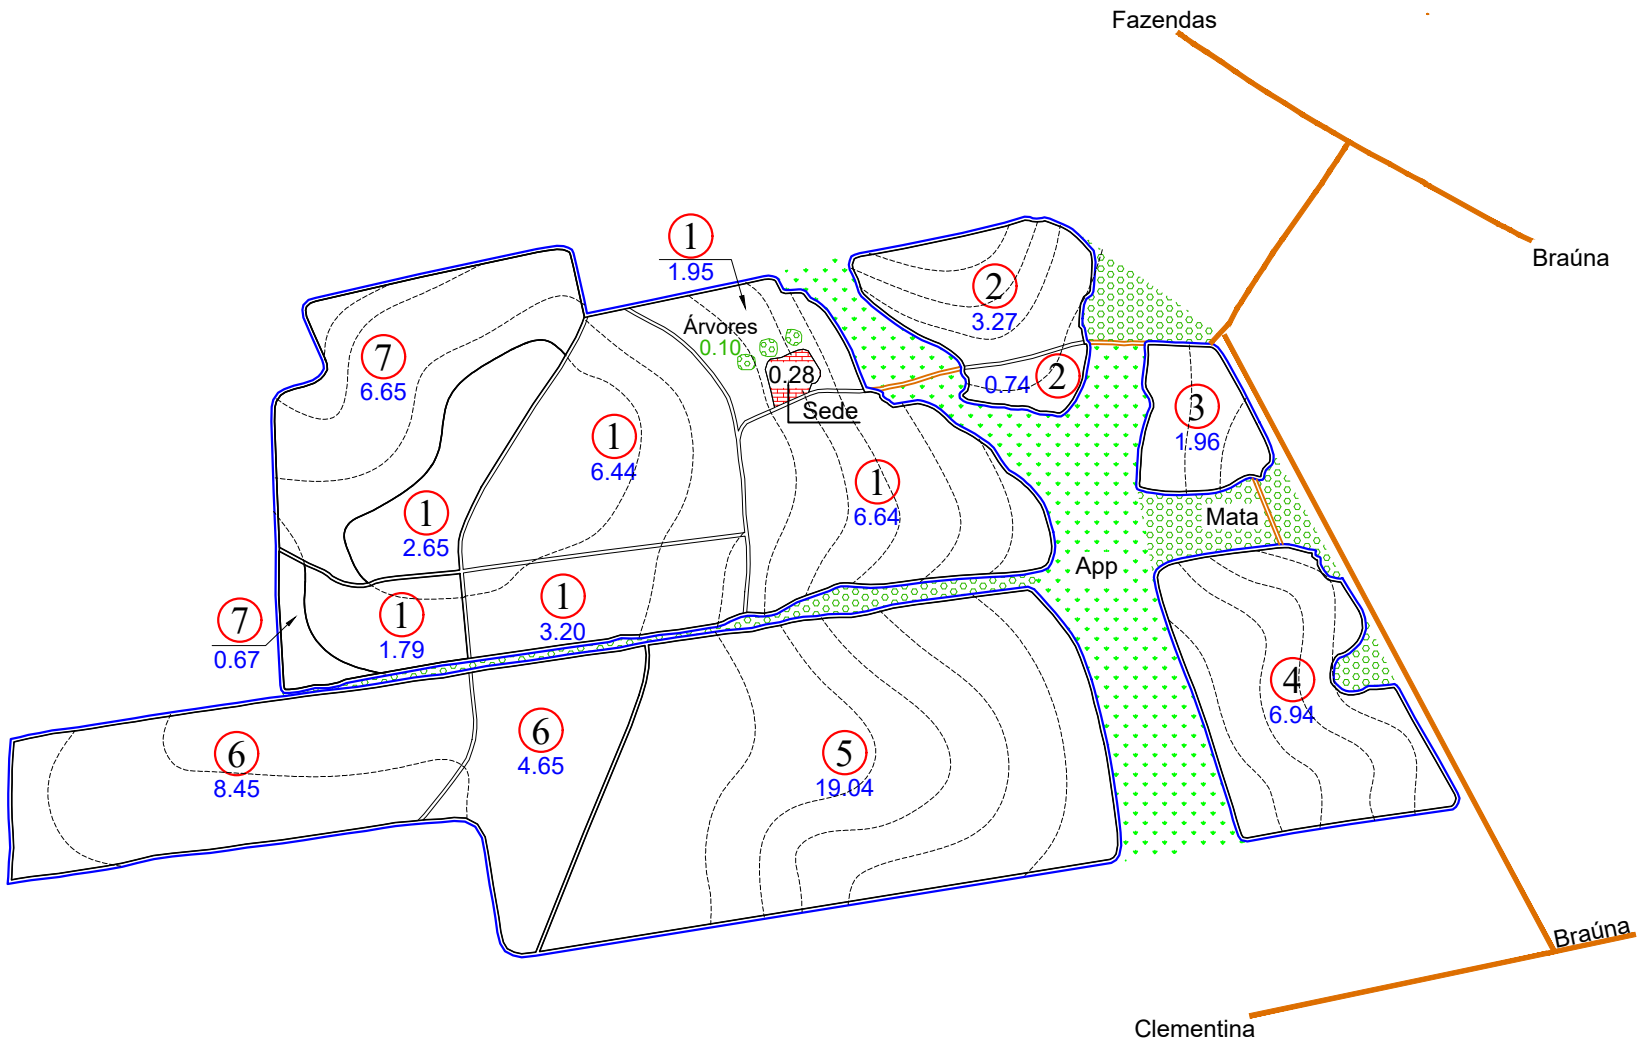


ESCALA: 1: 9.000

LEGENDA
- FAZENDA
- TALHÃO
- REDE ELÉTRICA
- TERRAÇO BASE LARGA
- TERRAÇO EMBUTIDO

ESPAÇAMENTO: 1.50 x 1.50 D.V: 0.00 %
TIRO MÉDIO ESTIMADO: 216.84 m

CROQUI DE ACESSO

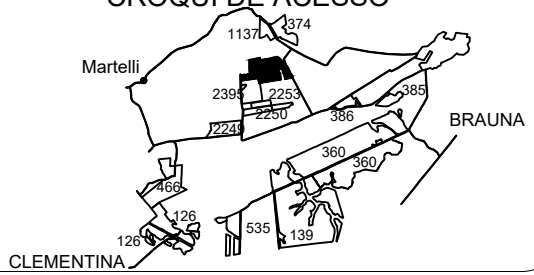

SÍTIO NOSSO RANCHO E SÍTIO SANTA LEOPOLDINA

PROPRIETÁRIO: JOSÉ FRANCISCO MARTINS
COMPRADOR: CLEALCO
MUNICÍPIO: BRAÚNA - SP

DISTÂNCIAS (km):
UNID. I - Asfalto: 8.00 Terra.: 8.00
UNID.I I - Asfalto: 64.50 Terra.: 8.00

COORDENADAS: E(X): 564369.09 N(Y): 7621294.34
LAT: -21°30'35.5191" LONG: -50°22'42.6590"
CLEALCO - AÇÚCAR E ALCOOL S/A - DEPARTAMENTO DE GEOTECNOLOGIA

LEVANTAMENTO VIA:
- SATÉLITE
- GPS / VANT
- GOOGLE

UNIDADE: I
PARTE: A/A
FUNDO AGRÍCOLA: 300398

M:\01-Mapa de safra\Mapas Atualizados\Terceiro\300398 - Sítio Nosso Rancho e Sítio Santa Leopoldina (José Francisco Martins)\300398 - Sítio Nosso Rancho e Sítio Santa Leopoldina (José Francisco Martins).dwg

Fabiano Castro 04/03/26