ZONA D.V.	Nº TAL.	DATA PL.	ÁREA (ha)	VAR.
999 4.00%	1	05/2022	24.24	RB975201
	2		19.97	
TOTAL PLANTIO			44.21	--------


ÁREAS	(ha)	(%)
PLANTIO	44.21	95.07
CARREADORES	2.29	4.93
OUTROS	0.00	0.00
SUB TOTAL AGRICULTÁVEL	46.50	100.00
AP.P.	0.00	0.00
ÁRVORES	0.00	0.00
OUTROS	0.00	0.00
SUB TOTAL NÃO AGRICULT.	0.00	0.00
ÁREA TOTAL	46.50	100.00

C. NÍVEL: 7593.08 m/l 1.75 ha 3.76 %


LEGENDA

- FAZENDA
- TALHÃO
- CURVA DE NÍVEL
- CARREADOR
- CONFRONTANTE
- REDE ELÉTRICA
- TRAJETO VAZIO
- TRAJETO CARREGADO

PLANTIO MANUAL - ESPAÇAMENTO: 1.50 X 1.50

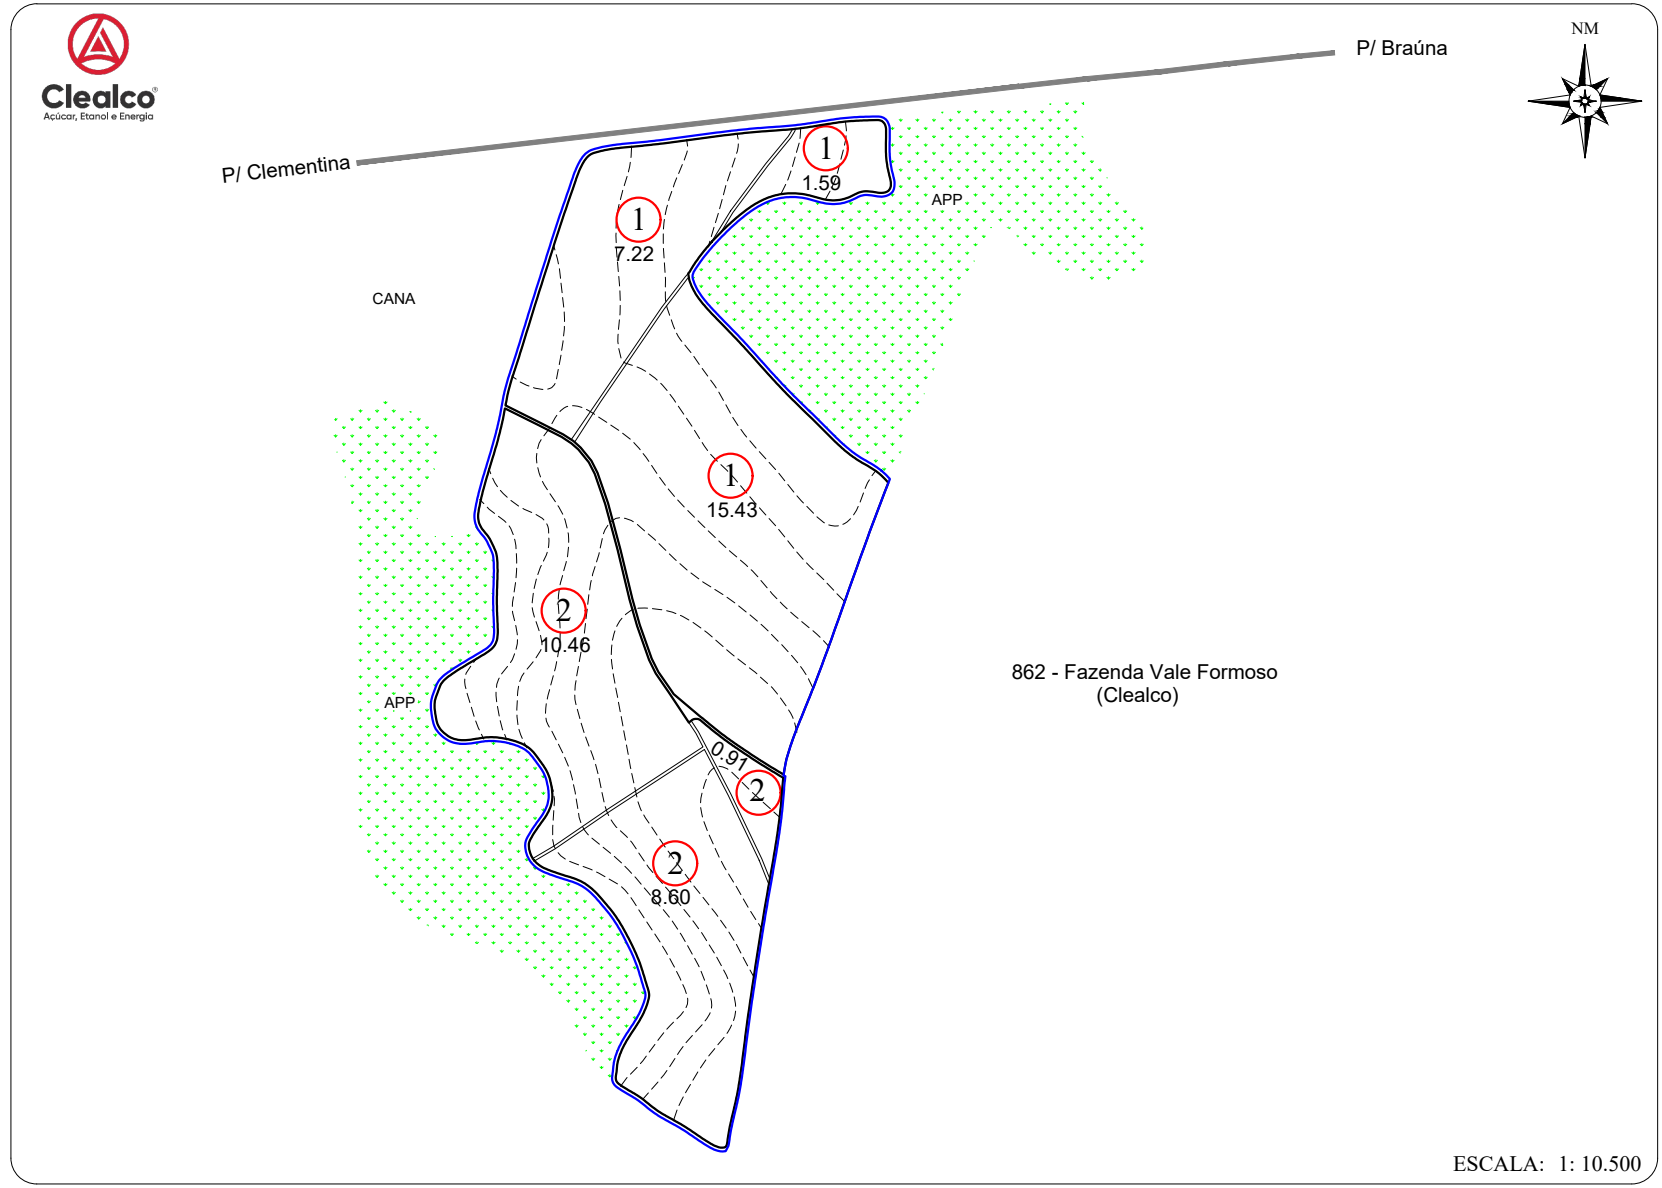

CROQUI DE ACESSO

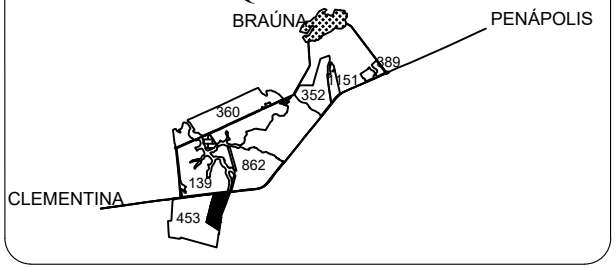

SÍTIO ANDORINHA

PROPRIETÁRIO: ESIO NILTON PITTA
ARRENDATÁRIO: ESIO NILTON PITTA
MUNICÍPIO: BRAÚNA

DISTÂNCIAS (km):

UNID. I - Asfalto:	9.50	Terra.:	0.50
UNID.I I - Asfalto:	24.00	Terra.:	13.60
UNID. III -Asfalto:	35.20	Terra.:	0.50

COORDENADAS: E(X): 566373 N(Y): 7615233
LAT: 21º 33' 52,12836" LONG: 50º 21' 32,15449"

CLEALCO - AÇÚCAR E ALCOOL S/A - DEPARTAMENTO DE TOPOGRAFIA

UNIDADE: I

PARTE: A/A

FUNDO AGRÍCOLA: 301272