ZONA DV	CLA.	Nº TAL.	ANO PL.	ÁREA (ha)	VAR.
999 4.65 %		1	04/2019	42.18	RB 975242
		2	04/2020	51.25	
		3		42.12	
TOTAL PLANTIO				135.55	--------

ÁREAS	(ha)	(%)
PLANTIO	135.55	92.98
CARREADORES	4.87	3.34
OUTROS	0.00	0.00
SUB TOTAL AGRICULTÁVEL	140.42	96.32
AP.P.	5.36	3.68
ÁRVORES	0.00	0.00
OUTROS	0.00	0.00
SUB TOTAL NÃO AGRICULT.	5.36	3.68
ÁREA TOTAL	145.78	100.00


C. NÍVEL: 12312.81 m/l 2.83 ha 1.94 %

LEGENDA

- FAZENDA
- TALHÃO
- CURVA DE NÍVEL
- CARREADOR
- CONFRONTANTE
- REDE ELÉTRICA
- TRAJETO VAZIO
- TRAJETO CARREGADO


PLANTIO MANUAL - ESPAÇAMENTO: 1.50 X 1.50
TIRO MÉDIO ESTIMADO: 345.53m

Clealco
Açúcar, Etanol e Energia

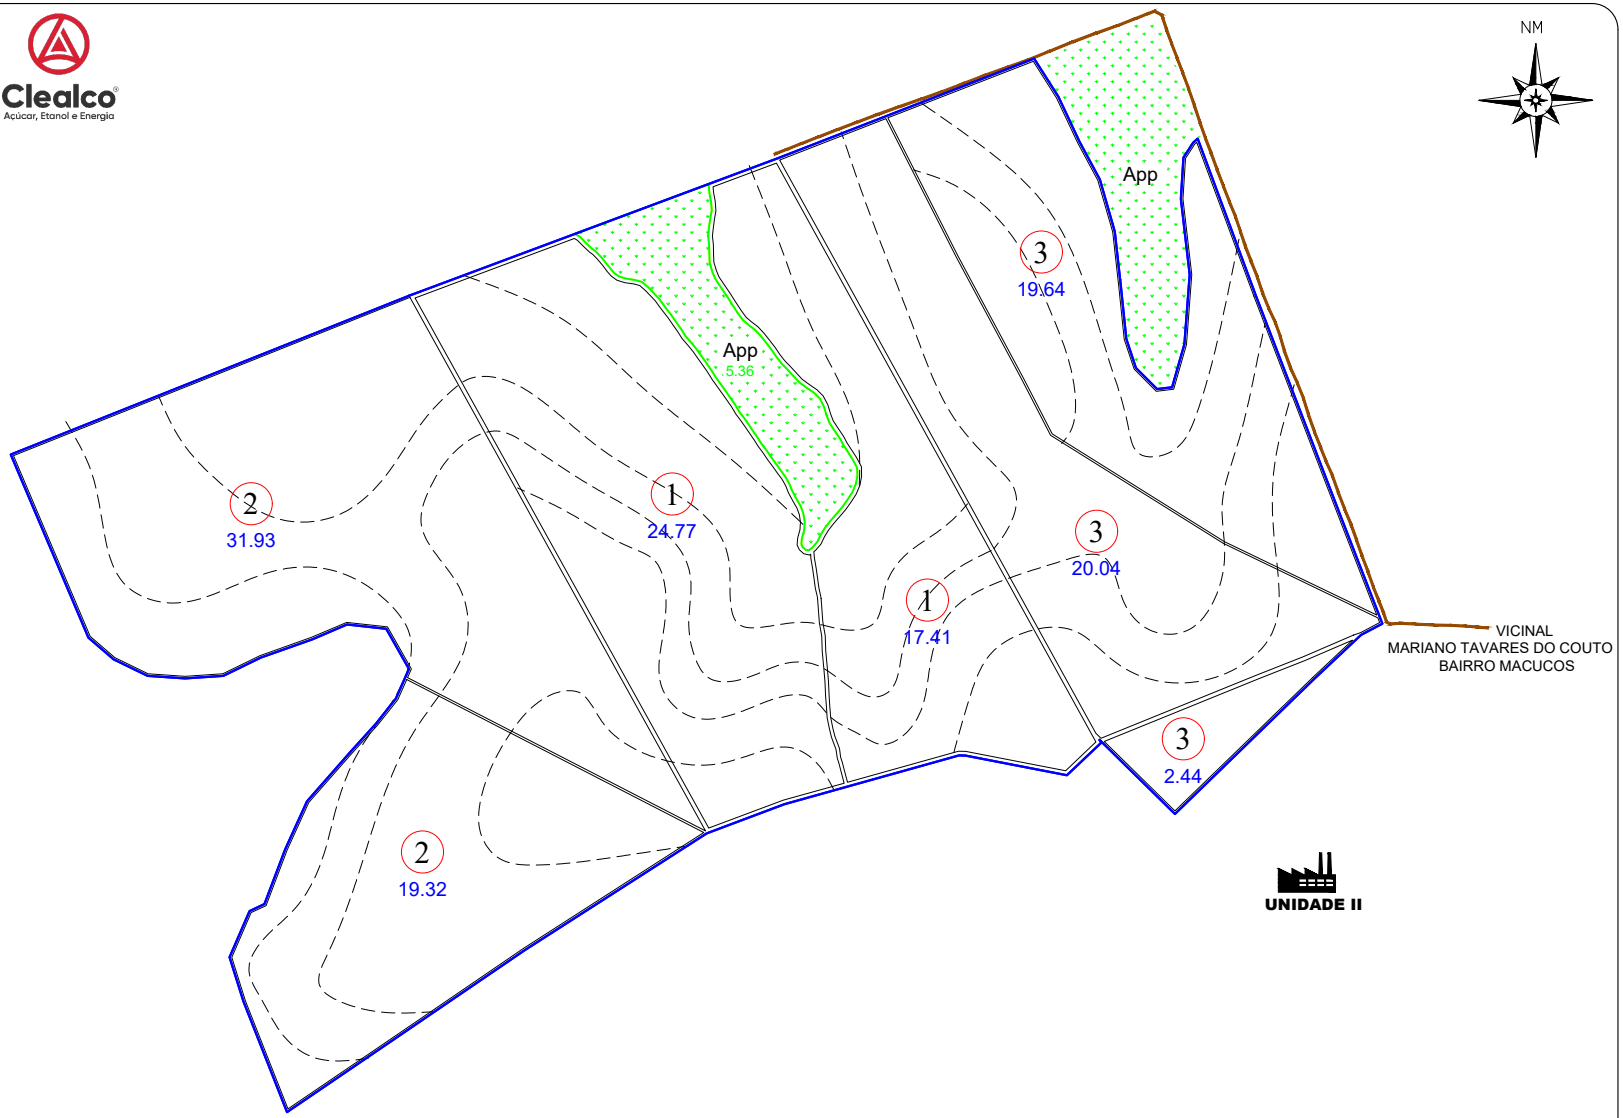

ESCALA: 1: 11.000

CROQUI DE ACESSO

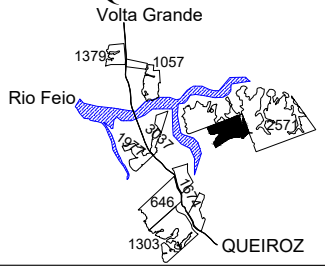

FAZENDA RIBEIRÃO DOS BUGRES

PROPRIETÁRIO: ELIANE RIBAS VICENTE
COMPRADOR: CLEALCO S/A
MUNICÍPIO: QUEIROZ

DISTÂNCIAS (km):
UNID. I - Asfalto: 68.00 Terra.: 15.50
UNID.I I - Asfalto: 14.60 Terra.: 15.50
UNID. III -Asfalto: 37.00 Terra.: 5.00

COORDENADAS: E(X): 577890 N(Y): 7598477
LAT: 21º 42' 55,40845" LONG: 50º 14' 48,89900"

CLEALCO - AÇÚCAR E ALCOOL S/A - DEPARTAMENTO DE TOPOGRAFIA

UNIDADE: II
PARTE: A/A
FUNDO AGRÍCOLA: 301581