
Clealco
Açúcar, Etanol e Energia

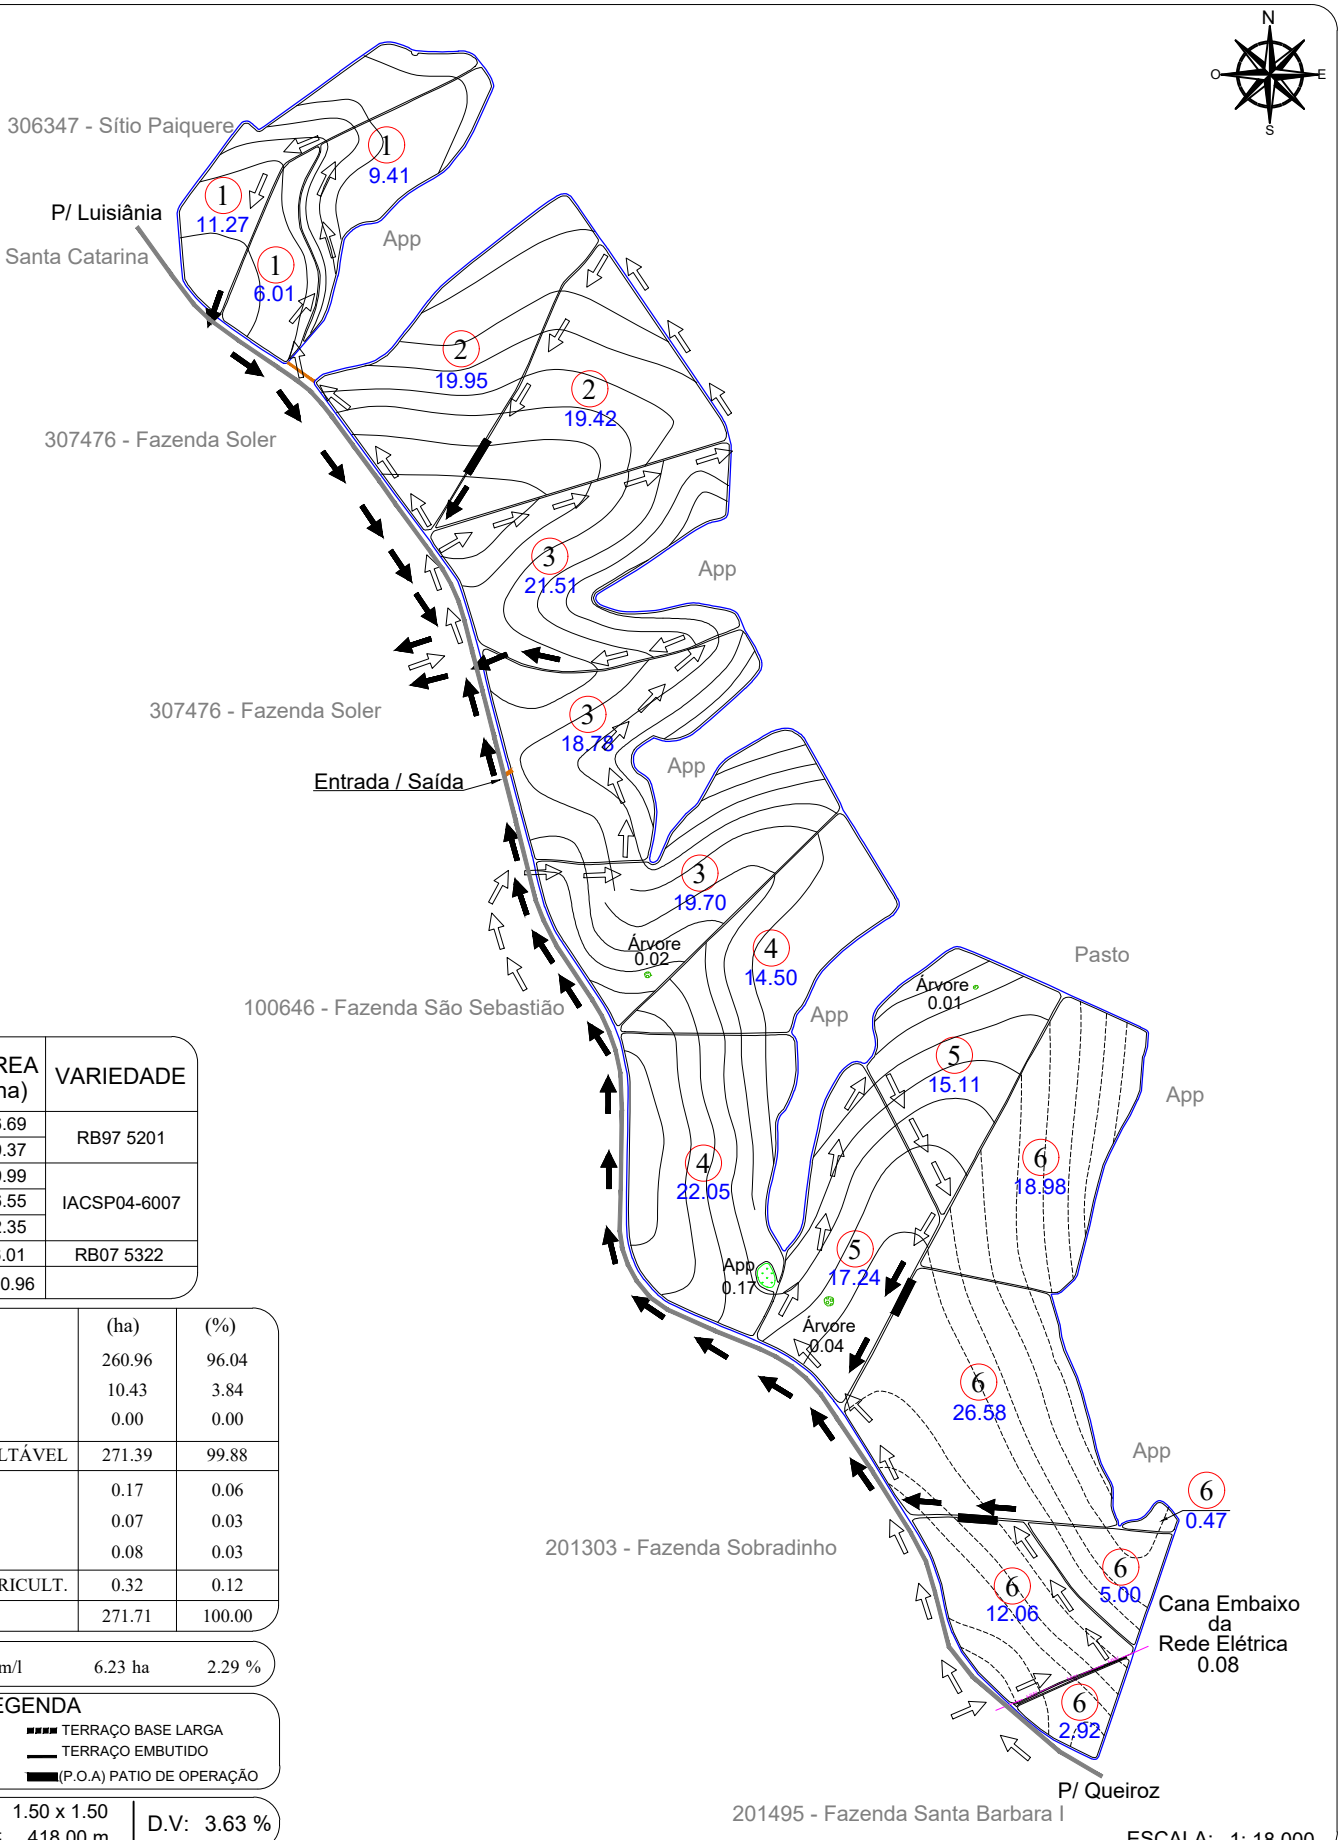

Nº TAL.	DATA PL.	ÁREA (ha)	VARIEDADE
1	05/2025	26.69	RB97 5201
2		39.37	
3	06/2025	59.99	IACSP04-6007
4		36.55	
5		32.35	
6	04/2026	66.01	RB07 5322
TOTAL PLANTIO		260.96	

ÁREAS	(ha)	(%)
PLANTIO	260.96	96.04
CARREADORES	10.43	3.84
OUTROS	0.00	0.00
SUB TOTAL AGRICULTÁVEL	271.39	99.88
AP.P.	0.17	0.06
ÁRVORES	0.07	0.03
OUTROS	0.08	0.03
SUB TOTAL NÃO AGRICULT.	0.32	0.12
ÁREA TOTAL	271.71	100.00

C. NÍVEL: 27082.05 m/l | 6.23 ha | 2.29 %


LEGENDA

- FAZENDA
- TALHÃO
- REDE ELÉTRICA
- TERRAÇO BASE LARGA
- TERRAÇO EMBUTIDO
- (P.O.A) PATIO DE OPERAÇÃO

ESPAÇAMENTO: 1.50 x 1.50
TIRO MÉDIO ESTIMADO: 418.00 m
D.V: 3.63 %

ESCALA: 1: 18.000

CROQUI DE ACESSO

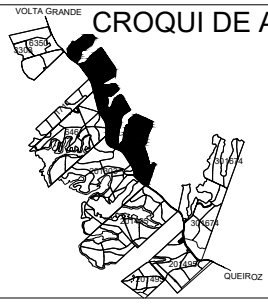

FAZENDA CACHOEIRA

PROPRIETÁRIO: ELIANE RIBAS VICENTE
COMPRADOR: CLEALCO
MUNICÍPIO: QUEIROZ - SP

DISTÂNCIAS (km):
UNID. I - Asfalto: 45.00 Terra.: 0.00
UNID.I I - Asfalto: 12.70 Terra.: 0.00

COORDENADAS: E(X): 576106.15 N(Y): 7594018.23
LAT: -21°45'20.9687" LONG: -50°15'50.2359"

CLEALCO - AÇÚCAR E ALCOOL S/A - DEPARTAMENTO DE GEOTECNOLOGIA

LEVANTAMENTO VIA:
SATÉLITE
GPS / VANT
GOOGLE

UNIDADE: II
PARTE: A/B
FUNDO AGRÍCOLA: 301674

M:\01-Mapa de safra\Mapas Atualizados\Terceiro\301674 - Fazenda Cachoeira (Eliana Ribas Vicente)\301674 A - Fazenda Cachoeira (Eliana Ribas Vicente).dwg

Bruno Gamboa 03/09/26