
Clealco
Açúcar, Etanol e Energia

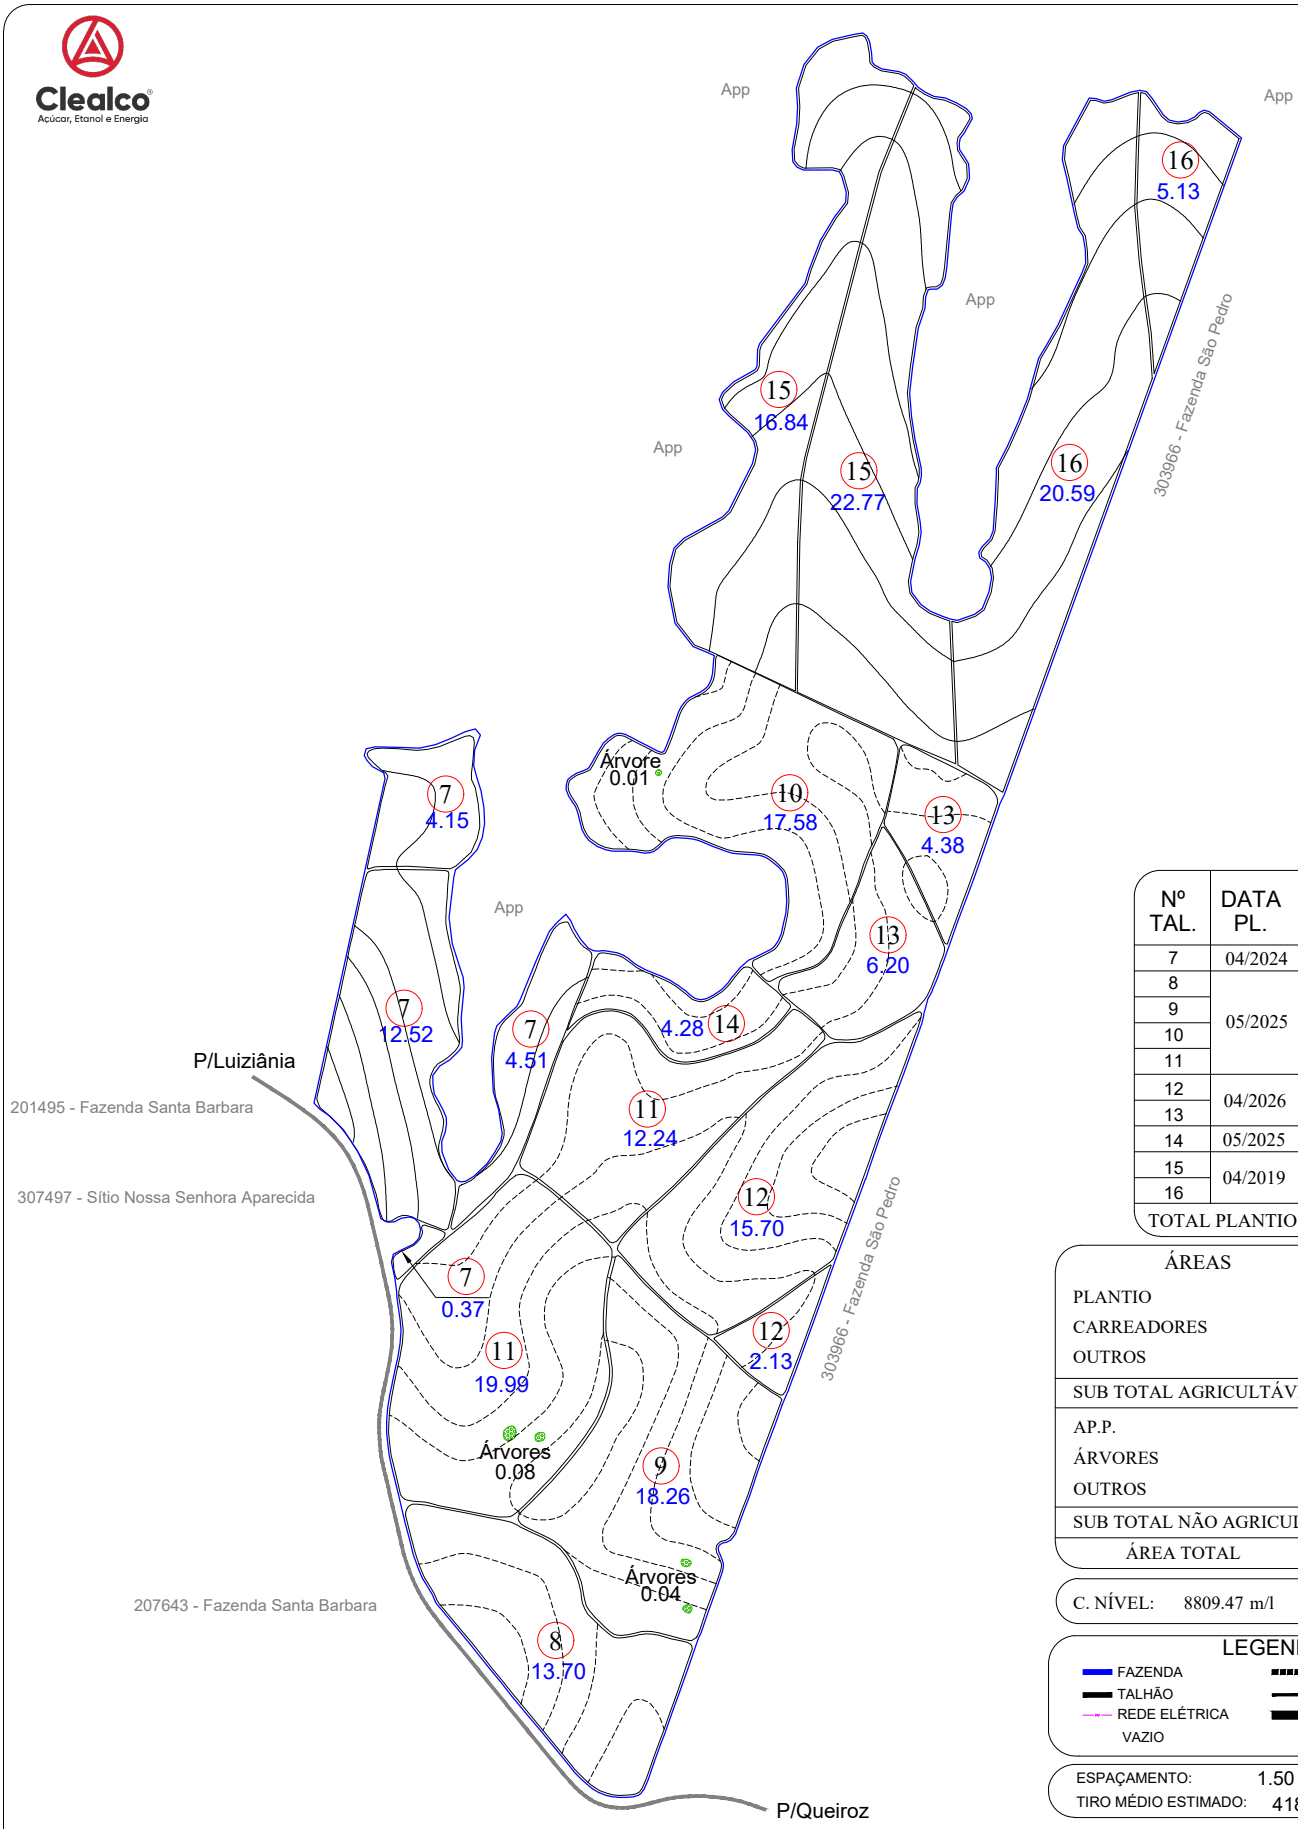

Nº TAL.	DATA PL.	ÁREA (ha)	VARIEDADE
7	04/2024	21.55	RB97 5201
8	05/2025	13.70	RB12 7825
9		18.26	
10		17.58	
11		32.23	
12	04/2026	17.83	
13		10.58	
14	05/2025	4.28	
15	04/2019	39.61	RB97 5242
16		25.72	
TOTAL PLANTIO		201.34	

ÁREAS	(ha)	(%)
PLANTIO	201.34	95.72
CARREADORES	8.86	4.21
OUTROS	0.00	0.00
SUB TOTAL AGRICULTÁVEL	210.20	99.94
AP.P.	0.00	0.00
ÁRVORES	0.13	0.06
OUTROS	0.00	0.00
SUB TOTAL NÃO AGRICULT.	0.13	0.06
ÁREA TOTAL	210.33	100.00

C. NÍVEL: 8809.47 m/l 2.03 ha 0.96 %


LEGENDA

- FAZENDA
- TALHÃO
- REDE ELÉTRICA VAZIO
- TERRAÇO BASE LARGA
- TERRAÇO EMBUTIDO
- (P.O.A) PATIO DE OPERAÇÃO CARREGADO

ESPAÇAMENTO: 1.50 x 1.50
TIRO MÉDIO ESTIMADO: 418.00 m
D.V: 2.98 %

ESCALA: 1: 14.500

CROQUI DE ACESSO

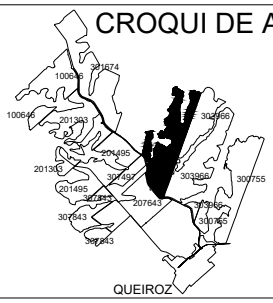

FAZENDA CACHOEIRA

PROPRIETÁRIO: ELIANE RIBAS VICENTE
COMPRADOR: CLEALCO
MUNICÍPIO: QUEIROZ - SP

DISTÂNCIAS (km):
UNID. I - Asfalto: 45.00 Terra.: 0.00
UNID.I I - Asfalto: 12.70 Terra.: 0.00

COORDENADAS: E(X): 578250.07 N(Y): 7592824.50
LAT: -21°45'59.4551" LONG: -50°14'35.3931"

CLEALCO - AÇÚCAR E ALCOOL S/A - DEPARTAMENTO DE GEOTECNOLOGIA

LEVANTAMENTO VIA:
SATÉLITE
GPS / VANT
GOOGLE

UNIDADE: II
PARTE: B/B
FUNDO AGRÍCOLA: 301674

M:\01-Mapa de safra\Mapas Atualizados\Terceiro\301674 - Fazenda Cachoeira (Eliana Ribas Vicente)\301674 B - Fazenda Cachoeira (Eliana Ribas Vicente).dwg

Bruno Gamboa 28/09/26