
Clealco
Açúcar, Etanol e Energia

Nº TAL.	DATA PL.	ÁREA (ha)	VARIEDADE
1	05/2023	7.18	RB 975242
2		9.67	
3		7.26	
4	04/2021	18.12	CTC 04
5	2026	4.77	REFORMA
TOTAL PLANTIO		47.00	

ÁREAS	(ha)	(%)
PLANTIO	47.00	95.29
CARREADORES	2.32	4.71
OUTROS	0.00	0.00
SUB TOTAL AGRICULTÁVEL	49.32	100.00
AP.P.	0.00	0.00
ÁRVORES	0.00	0.00
OUTROS	0.00	0.00
SUB TOTAL NÃO AGRICULT.	0.00	0.00
ÁREA TOTAL	49.32	100.00

C. NÍVEL: 8754.74 m/l 2.01 ha 4.08 %

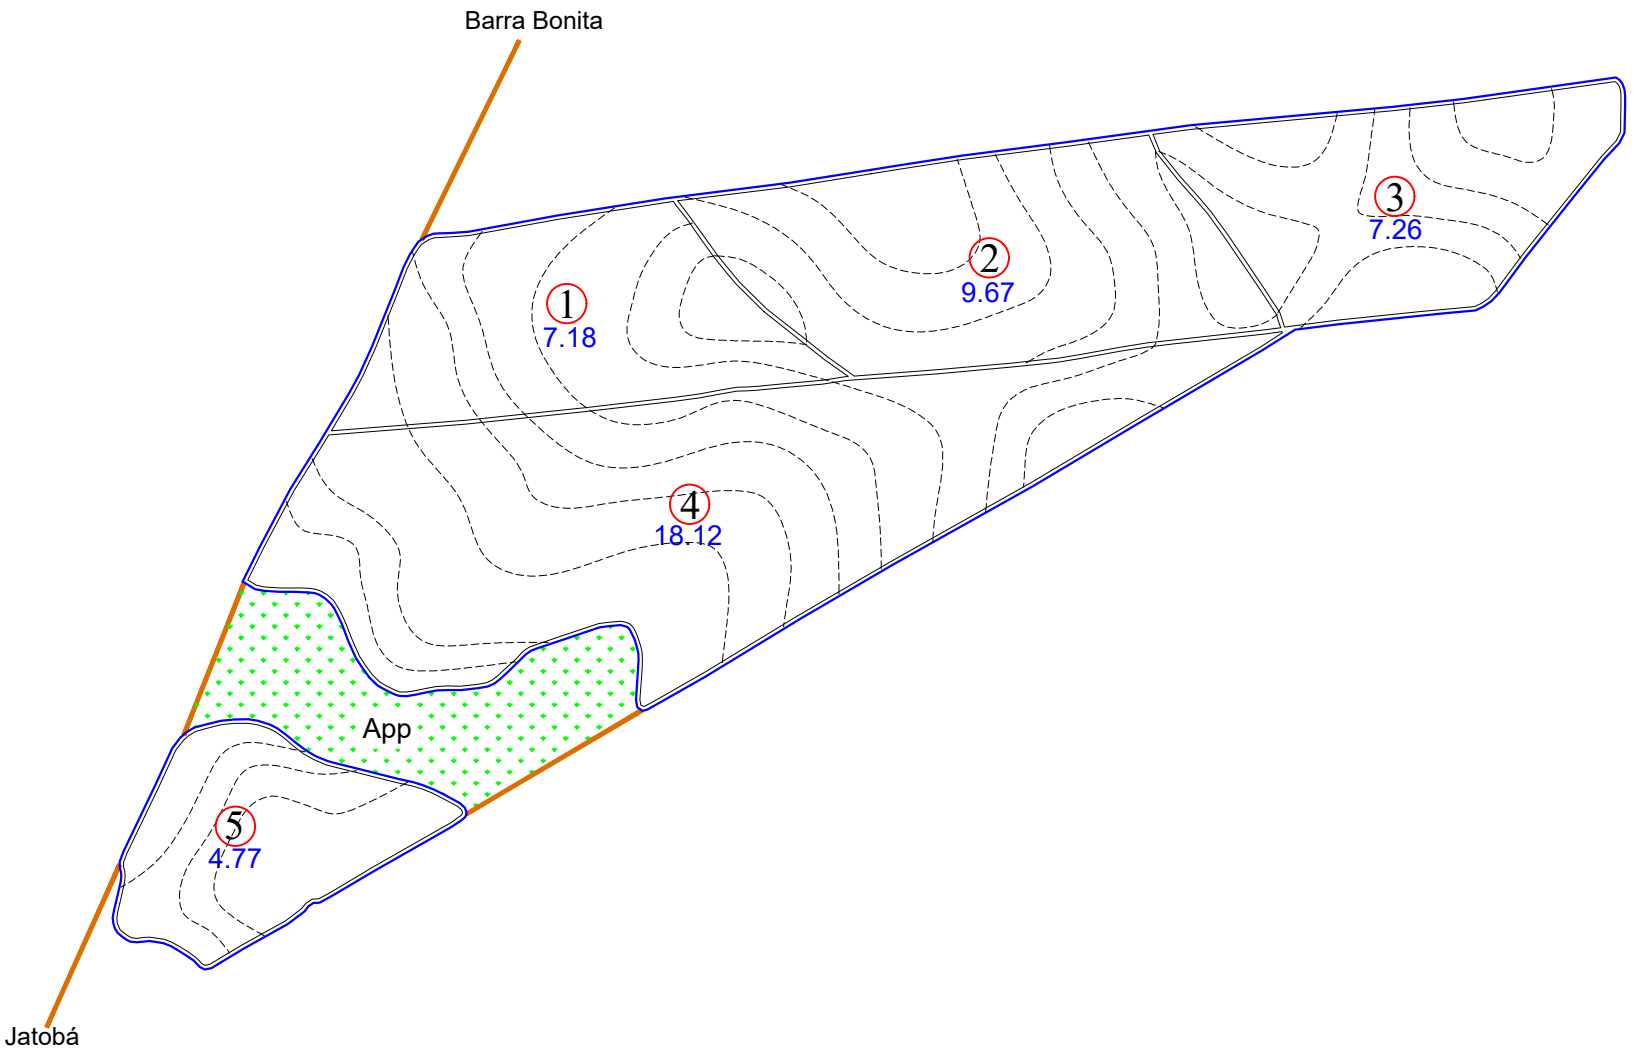


ESCALA: 1: 7.800

LEGENDA
- FAZENDA
- TALHÃO
- REDE ELÉTRICA
- TERRAÇO BASE LARGA
- TERRAÇO EMBUTIDO

ESPAÇAMENTO: 1.50 x 1.50 D.V: 5.50 %
TIRO MÉDIO ESTIMADO: 000.00 m

CROQUI DE ACESSO

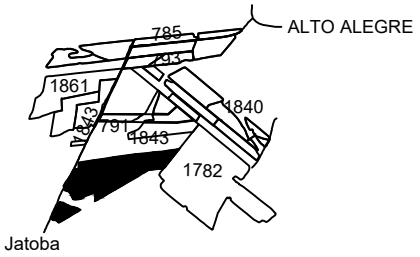

SITIO AURORA I,II,III,IV,V

PROPRIETÁRIO: DURVAL C. CRUZ MARTINS
COMPRADOR: CLEALCO
MUNICÍPIO: ALTO ALEGRE - SP

DISTÂNCIAS (km):
UNID. I - Asfalto: 37.00 Terra.: 4.80
UNID.I I - Asfalto: 32.20 Terra.: 12.00

COORDENADAS: E(X): 579934.03 N(Y): 7611505.86
LAT: -21°35'51.6154" LONG: -50°13'40.0019"

CLEALCO - AÇÚCAR E ALCOOL S/A - DEPARTAMENTO DE GEOTECNOLOGIA

LEVANTAMENTO VIA:
- SATÉLITE
- GPS / VANT
- GOOGLE

UNIDADE: I
PARTE: A/A
FUNDO AGRÍCOLA: 301724

M:\01-Mapa de safra\Mapas Atualizados\Terceiro\301724 - Sitio Aurora I, II, III, IV, V (Durval Cesar Cruz Martins)\301724 - Sitio Aurora I, II, III, IV, V (Durval Cesar Cruz Martins).dwg

Fabiano Castro 04/03/26