ZONA DV	Nº TAL.	DATA PL.	ÁREA (ha)	VARIEDADE
999 4.22 %	1	06/2020	6.45	RB867515
	2		7.41	
	3	06/2022	3.58	
	4		6.11	
TOTAL PLANTIO			23.55	--------


ÁREAS	(ha)	(%)
PLANTIO	23.55	91.97
CARREADORES	2.04	7.99
OUTROS	0.00	0.00
SUB TOTAL AGRICULTÁVEL	25.59	99.96
AP.P.	0.00	0.00
ÁRVORES	0.01	0.04
OUTROS	0.00	0.00
SUB TOTAL NÃO AGRICULT.	0.01	0.04
ÁREA TOTAL	25.60	100.00

C. NÍVEL: 2421.23 m/l 0.56 ha 2.17 %


LEGENDA

- FAZENDA
- TALHÃO
- CURVA DE NÍVEL
- CARREADOR
- CONFRONTANTE
- REDE ELÉTRICA
- TRAJETO VAZIO
- TRAJETO CARREGADO

PLANTIO MANUAL - ESPAÇAMENTO: 1.50 X 1.50
TIRO MÉDIO ESTIMADO: 146.19 m

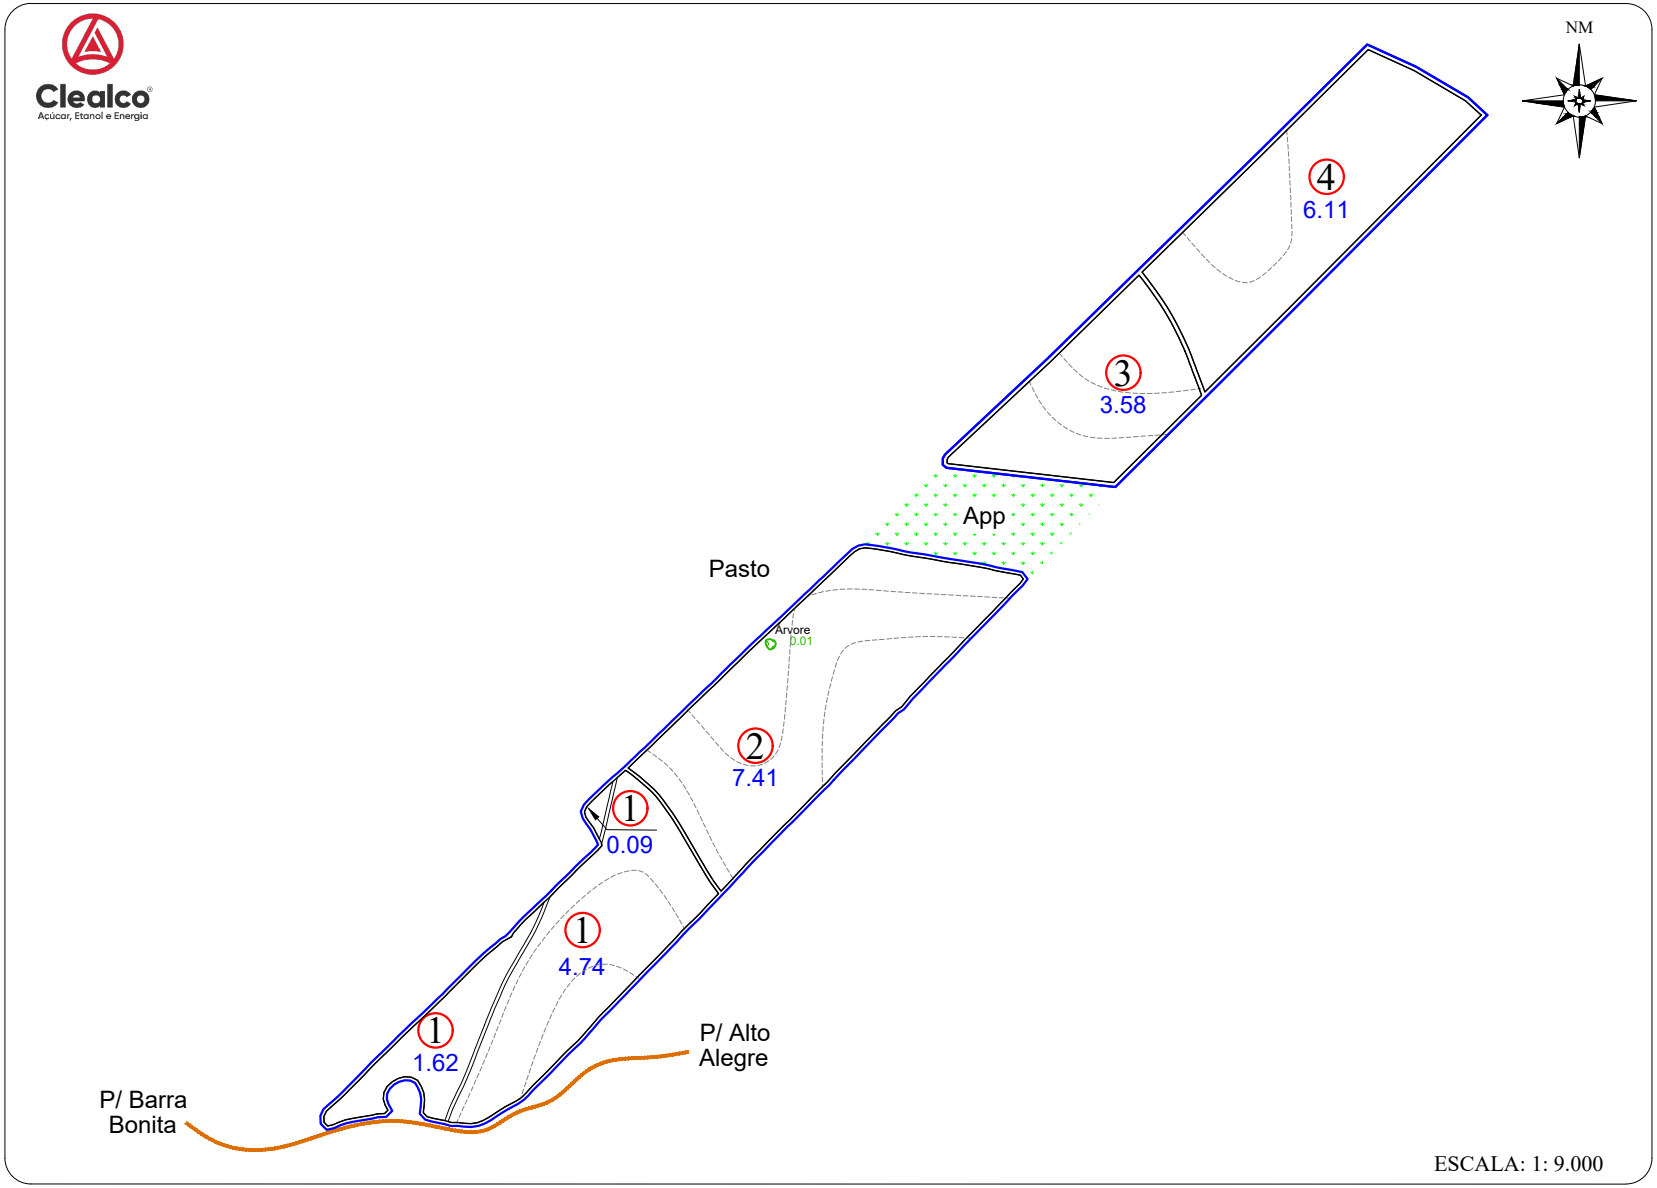

CROQUI DE ACESSO

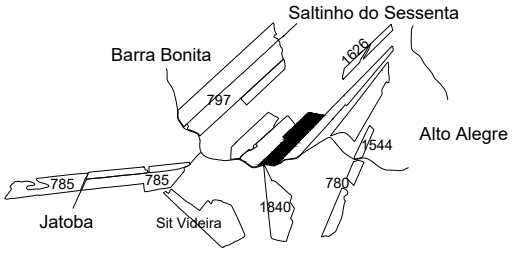

SITIO SAO PEDRO

PROPRIETÁRIO: LUIZ ANTONIO F. MARTINES
ARRENDATÁRIO: CLEALCO S/A
MUNICÍPIO: ALTO ALEGRE

DISTÂNCIAS (km):
UNID. I - Asfalto: 48.00 Terra.: 4.30
UNID.I I - Asfalto: 36.10 Terra.: 4.30
UNID. III -Asfalto: 13.00 Terra.: 4.30

COORDENADAS: E(X): 583438.33 N(Y): 7614060.64
LAT: -21°34'27.9489" LONG: -50°11'38.5956"

CLEALCO - AÇÚCAR E ALCOOL S/A - DEPARTAMENTO DE TOPOGRAFIA

UNIDADE: I
PARTE: A/A
FUNDO AGRÍCOLA: 301761

M:\01-Mapa de safra\Mapas Atualizados\Terceiro\301761 - Sítio São Pedro (Luiz Antonio Fernandes Martines)\301761 - Sítio São Pedro (Luiz Antonio Fernandes Martines).dwg

Fernanda Bezerra 01/03/23