
Estudo N°: 256

Clealco
Açúcar, Etanol e Energia

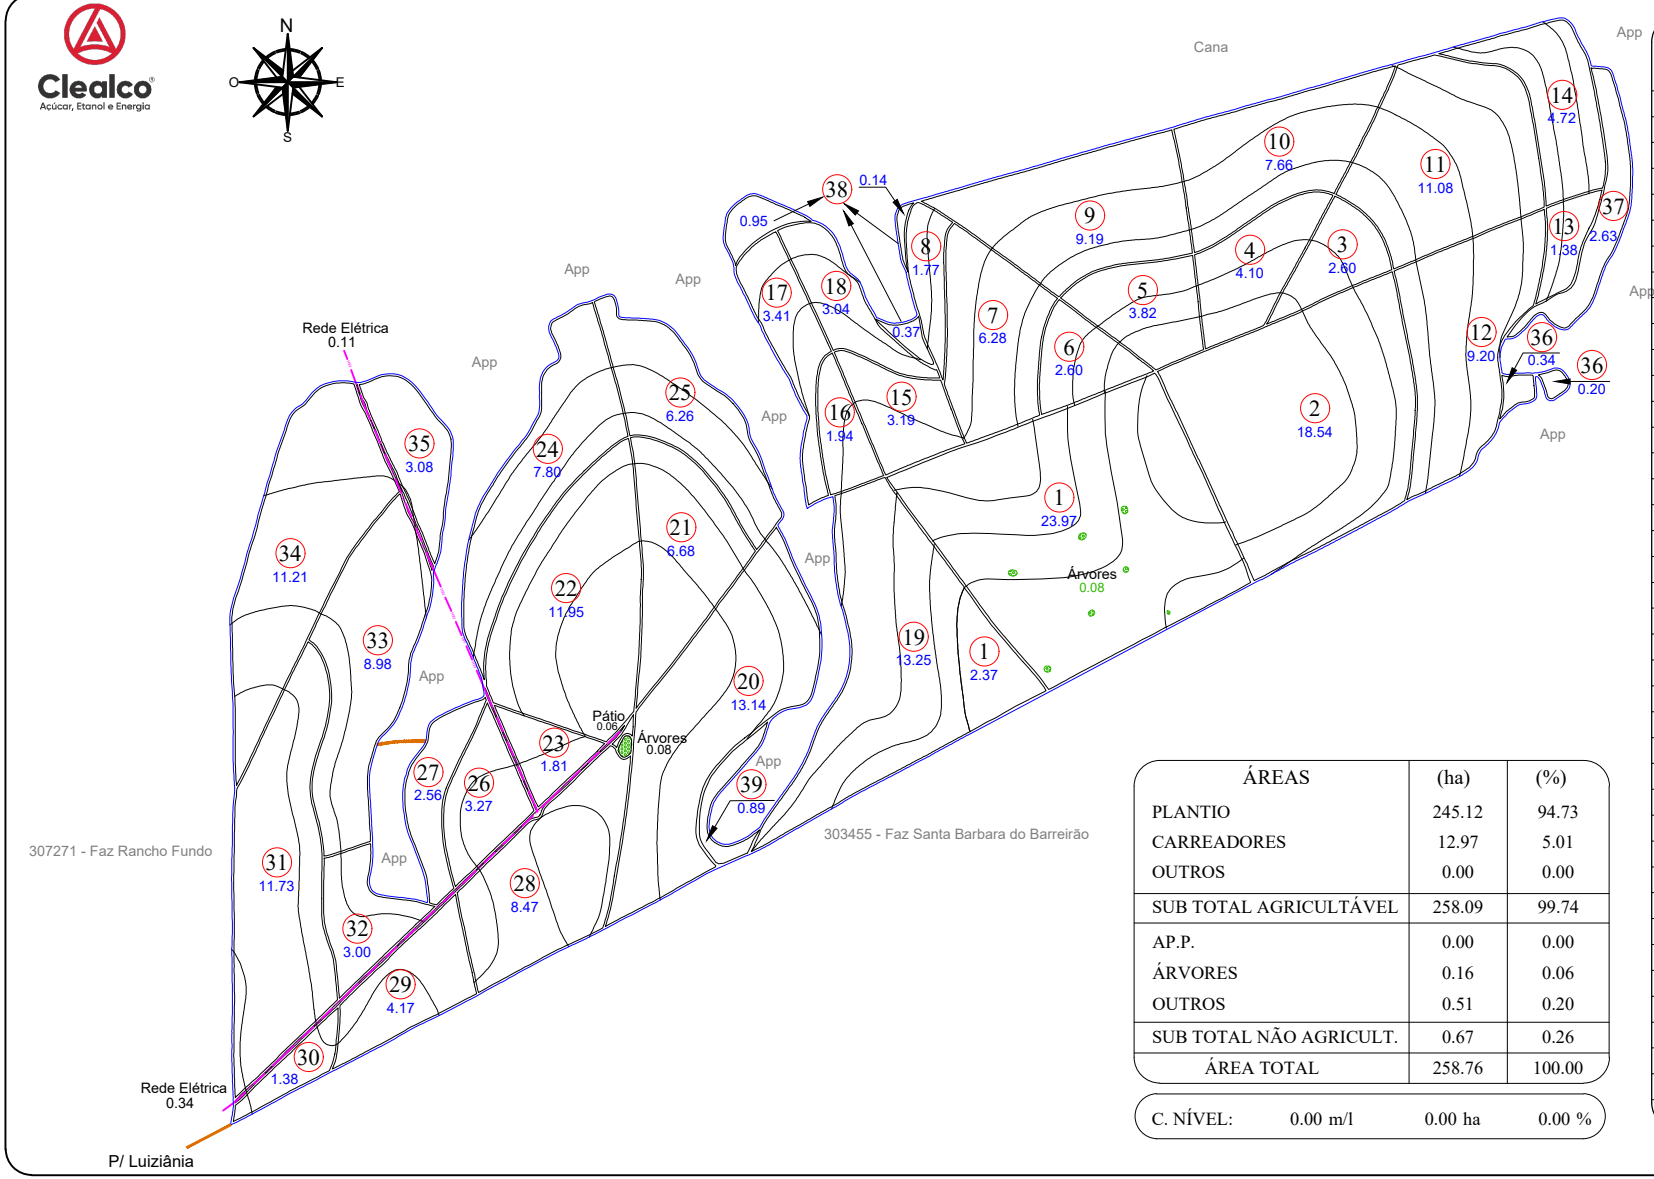

ÁREAS	(ha)	(%)
PLANTIO	245.12	94.73
CARREADORES	12.97	5.01
OUTROS	0.00	0.00
SUB TOTAL AGRICULTÁVEL	258.09	99.74
AP.P.	0.00	0.00
ÁRVORES	0.16	0.06
OUTROS	0.51	0.20
SUB TOTAL NÃO AGRICULT.	0.67	0.26
ÁREA TOTAL	258.76	100.00

C. NÍVEL:	0.00 m/l	0.00 ha	0.00 %

Nº TAL.	DATA PL.	ÁREA (ha)	VAR.
1	2022	26.34	RB 867515
2		18.54	
3		2.60	
4		4.10	
5		3.82	
6		2.60	
7		6.28	
8		1.77	
9		9.19	
10		7.66	
11		11.08	
12		9.20	
13		1.38	
14		4.72	
15		3.19	
16		1.94	
17		3.41	
18	05/2025	3.04	RB 975242
19		13.25	
20		13.14	
21		6.68	
22		11.95	
23		1.81	
24		7.80	
25		6.26	
26		3.27	
27		2.56	
28		8.47	
29		4.17	
30		1.38	
31		11.73	
32		3.00	
33		8.98	
34		11.21	
35		3.08	
36	2024	0.54	--------
37		2.63	
38		1.46	
39		0.89	
TOTAL PLANTIO		245.12	--------


ESCALA: 1: 15.000

LEGENDA

- FAZENDA
- TALHÃO
- REDE ELÉTRICA
- TERRAÇO BASE LARGA
- TERRAÇO EMBUTIDO

ESPAÇAMENTO: 1.50 x 1.50
TIRO MÉDIO ESTIMADO: 000.00 m
D.V: 7.60 %

CROQUI DE ACESSO

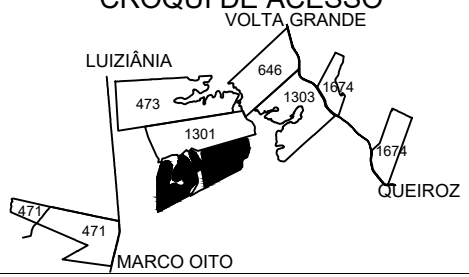

FAZENDA SANTO ANTONIO

PROPRIETÁRIO: FELIPE FERRAZ
COMPRADOR: CLEALCO
MUNICÍPIO: QUEIROZ - SP

DISTÂNCIAS (km):
UNID. I - Asfalto: 36.20 Terra.: 11.50
UNID.I I - Asfalto: 16.60 Terra.: 12.50

COORDENADAS: E(X): 571467.71 N(Y): 7591454.29
LAT: -21°46'45.0522" LONG: -50°18'31.3224"
CLEALCO - AÇÚCAR E ALCOOL S/A - DEPARTAMENTO DE GEOTECNOLOGIA

LEVANTAMENTO VIA:
SATÉLITE
GPS / VANT
GOOGLE

UNIDADE: II
PARTE: A/A
FUNDO AGRÍCOLA: 301962

M:\01-Mapa de safra\Mapas Atualizados\Terceiro\301962 - Fazenda Santo Antonio do Barreirão (Alexandre de F. Ferraz)\301962 - Fazenda Santo Antonio - (Felipe Ferraz) - 256.dwg

Peterson Santos 25/03/2026