
Clealco
Açúcar, Etanol e Energia

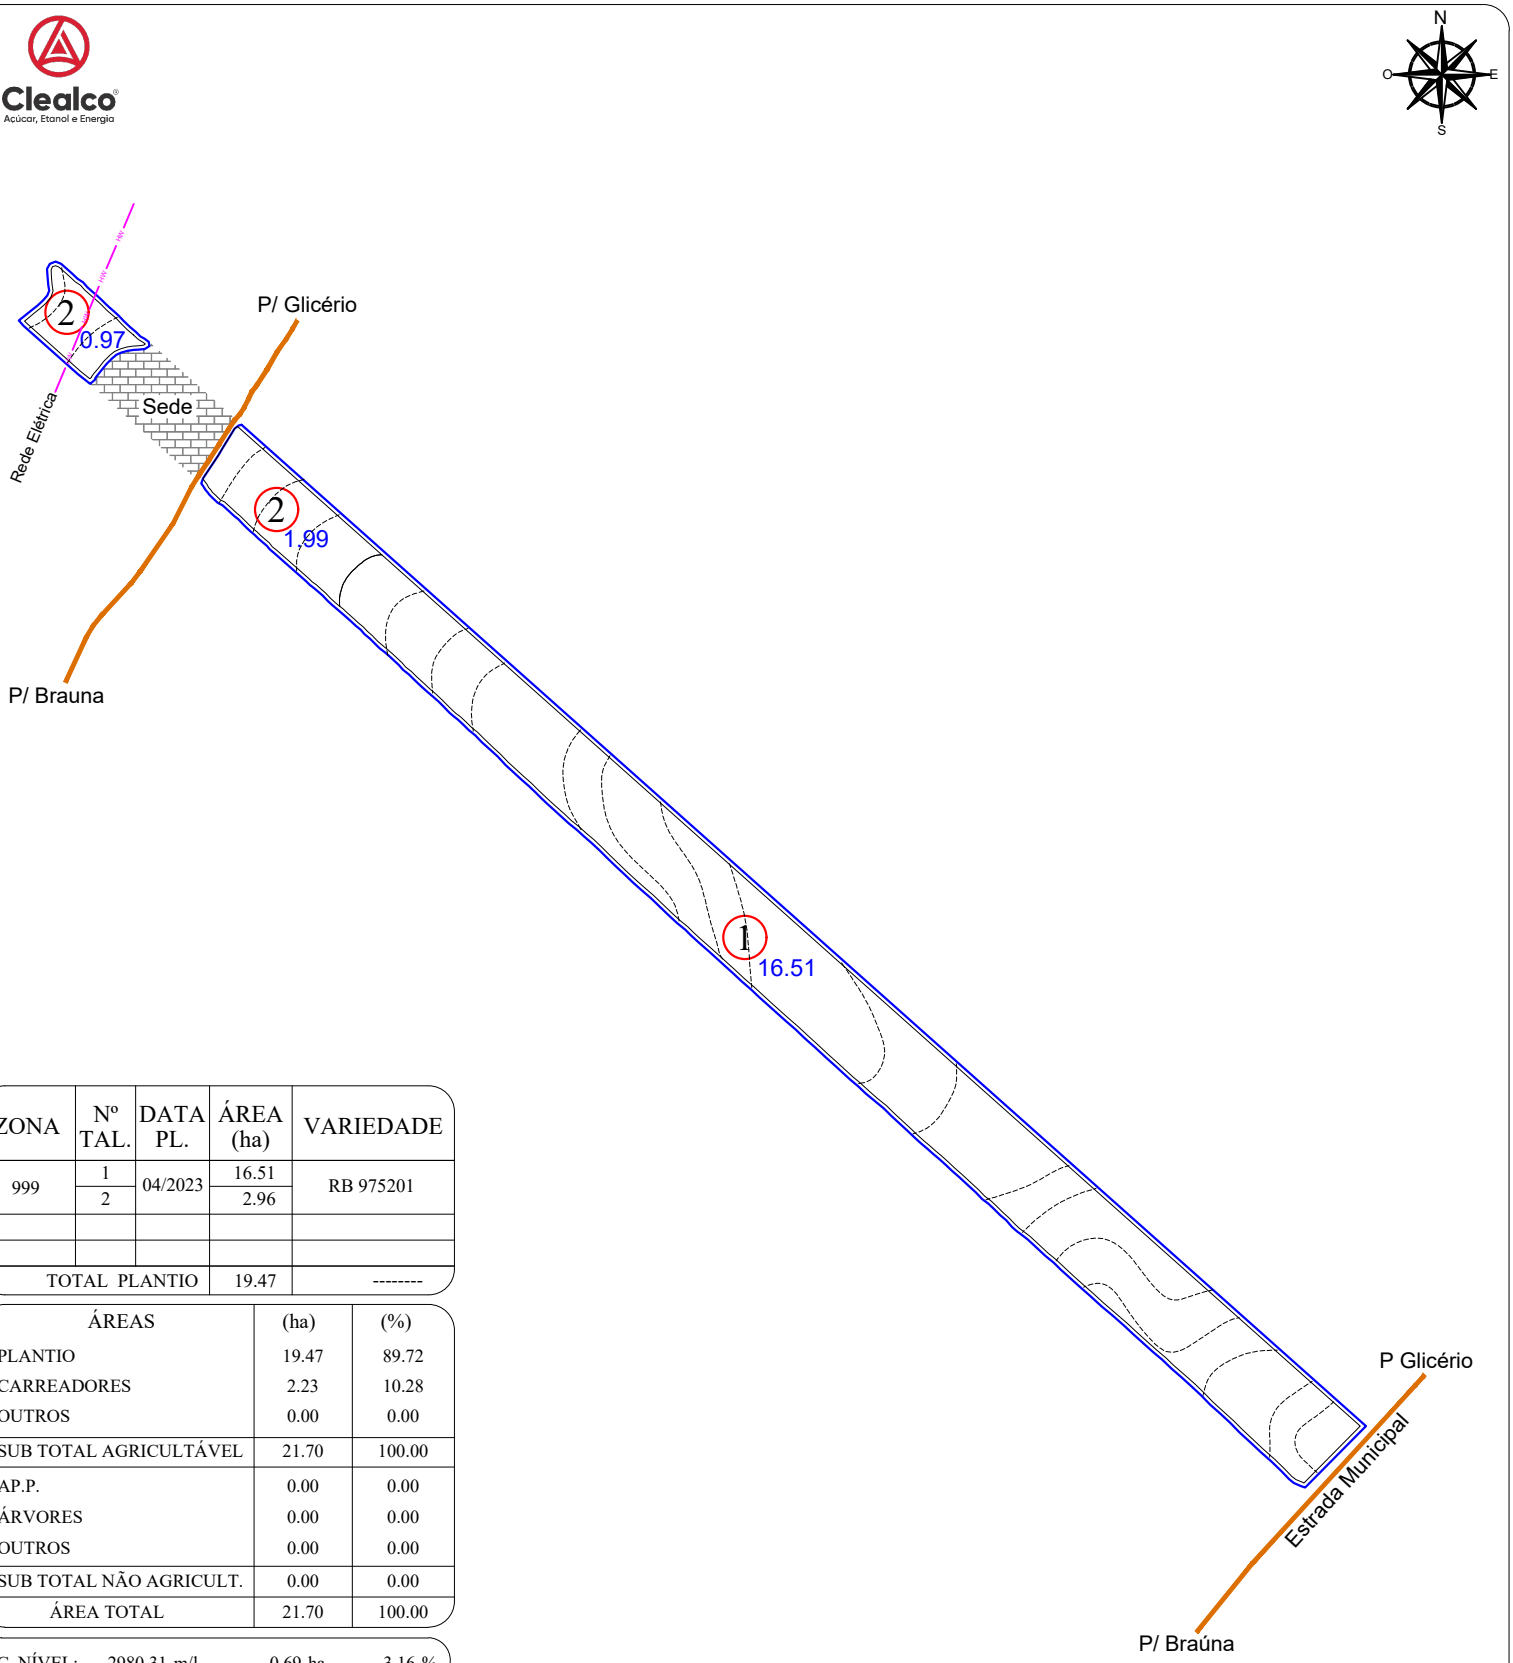

ZONA	Nº TAL.	DATA PL.	ÁREA (ha)	VARIEDADE
999	1	04/2023	16.51	RB 975201
	2		2.96	
TOTAL PLANTIO			19.47	--------

ÁREAS	(ha)	(%)
PLANTIO	19.47	89.72
CARREADORES	2.23	10.28
OUTROS	0.00	0.00
SUB TOTAL AGRICULTÁVEL	21.70	100.00
AP.P.	0.00	0.00
ÁRVORES	0.00	0.00
OUTROS	0.00	0.00
SUB TOTAL NÃO AGRICULT.	0.00	0.00
ÁREA TOTAL	21.70	100.00

C. NÍVEL: 2980.31 m/l 0.69 ha 3.16 %


LEGENDA

- FAZENDA
- TALHÃO
- REDE ELÉTRICA
- TERRAÇO BASE LARGA
- TERRAÇO EMBUTIDO
- (P.O.A) PATIO DE OPERAÇÃO

ESPAÇAMENTO: 1.50 x 1.50
TIRO MÉDIO ESTIMADO: 388.53 m
D.V: 4.10 %

ESCALA: 1: 10.000

CROQUI DE ACESSO

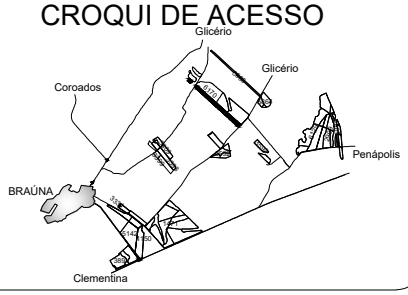

SÍTIO FORMOSO

PROPRIETÁRIO: JOSÉ APARECIDO FERREIRA
COMPRADOR: CLEALCO
MUNICÍPIO: GLICÉRIO - SP

DISTÂNCIAS (km):
UNID. I - Asfalto: 18.50 Terra.: 5.10
UNID.I I - Asfalto: 29.00 Terra.: 22.50

COORDENADAS: E(X): 574283.77 N(Y): 7626135.91
LAT: -21°27'56.6710" LONG: -50°16'58.8352"

CLEALCO - AÇÚCAR E ALCOOL S/A - DEPARTAMENTO DE GEOTECNOLOGIA

LEVANTAMENTO VIA:
- SATÉLITE
- GPS / VANT
- GOOGLE

UNIDADE: I
PARTE: A/A
FUNDO AGRÍCOLA: 301999

M:\01-Mapa de safra\Mapas Atualizados\Terceiro\301999 - Sítio Formoso (José Aparecido Ferreira)\301999 - Sítio Formoso (José Aparecido Ferreira).dwg

Bruno Gamboa 23/07/25