
Clealco
Açúcar, Etanol e Energia

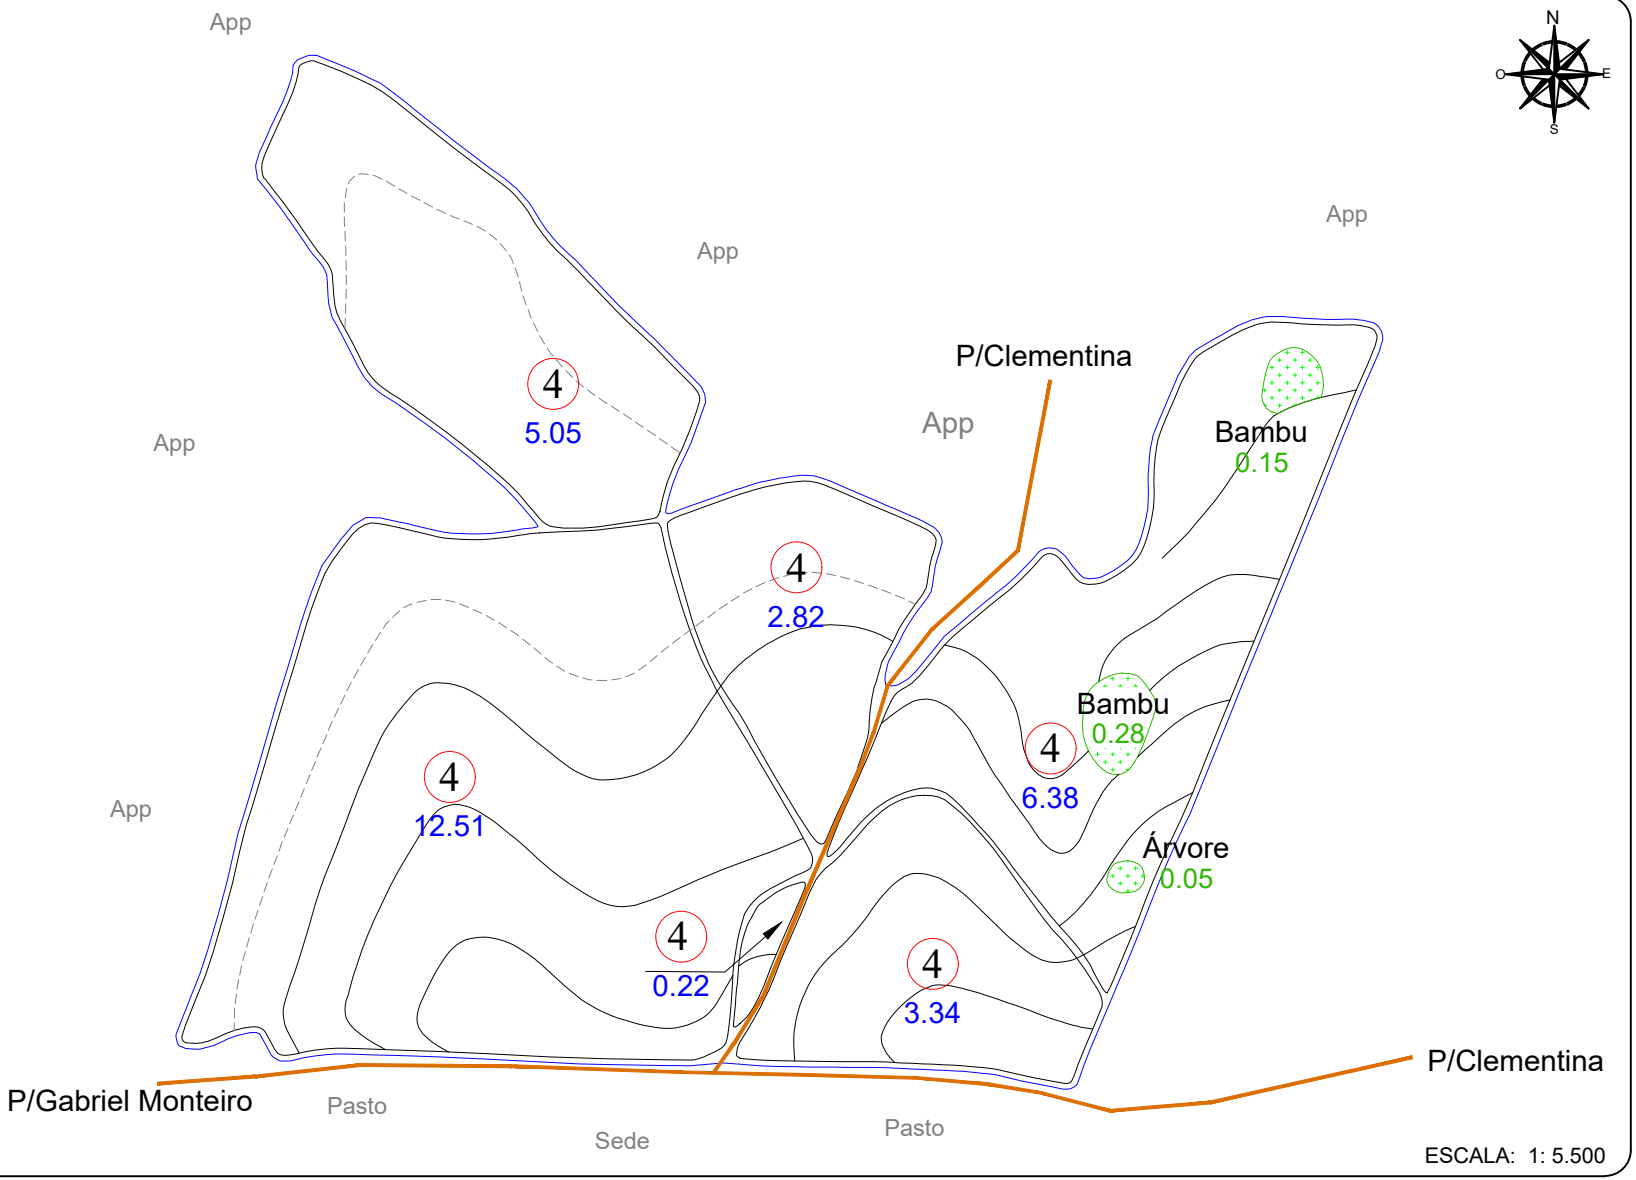

Nº TAL.	DATA PL.	ÁREA (ha)	VARIEDADE
4	07/2025	30.32	RB975201
TOTAL PLANTIO		30.32	

ÁREAS	(ha)	(%)
PLANTIO	30.32	92.75
CARREADORES	1.89	5.78
OUTROS	0.00	0.00
SUB TOTAL AGRICULTÁVEL	32.21	98.53
AP.P.	0.00	0.00
ÁRVORES	0.48	1.47
OUTROS	0.00	0.00
SUB TOTAL NÃO AGRICULT.	0.48	1.47
ÁREA TOTAL	32.69	100.00

C. NÍVEL: 3161.81 m/l 0.73 ha 2.22 %

ESCALA: 1: 5.500


LEGENDA

- FAZENDA
- TALHÃO
- REDE ELÉTRICA
- TERRAÇO BASE LARGA
- TERRAÇO EMBUTIDO

ESPAÇAMENTO: 1.50 x 1.50
TIRO MÉDIO ESTIMADO: 161.08 m

D.V: 5.09 %

CROQUI DE ACESSO

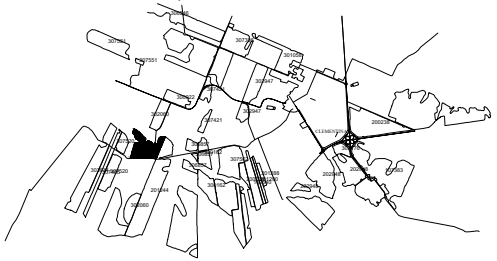

SÍTIO SÃO JOÃO

PROPRIETÁRIO: RAFAEL YUKIO RIBEIRO IDA
COMPRADOR: CLEALCO
MUNICÍPIO: CLEMENTINA - SP

DISTÂNCIAS (km):
UNID. I - Asfalto: 6.50 Terra.: 3.50
UNID.I I - Asfalto: 54.00 Terra.: 3.50

COORDENADAS: E(X): 553305.76 N(Y): 7614535.63
LAT: -21°34'16.6540" LONG: -50°29'6.4100"

CLEALCO - AÇÚCAR E ALCOOL S/A - DEPARTAMENTO DE GEOTECNOLOGIA

LEVANTAMENTO VIA:
SATÉLITE
GPS / VANT
GOOGLE

UNIDADE: I

PARTE: C/C

FUNDO AGRÍCOLA: 302060

M:\01-Mapa de safra\Mapas Atualizados\Terceiro\302060 - Fazenda São João I (Rafael Yukio Ribeiro Ida)\302060 C - Fazenda São João I (Rafael Yukio Ribeiro Ida).dwg

Peterson Santos 26/01/2026