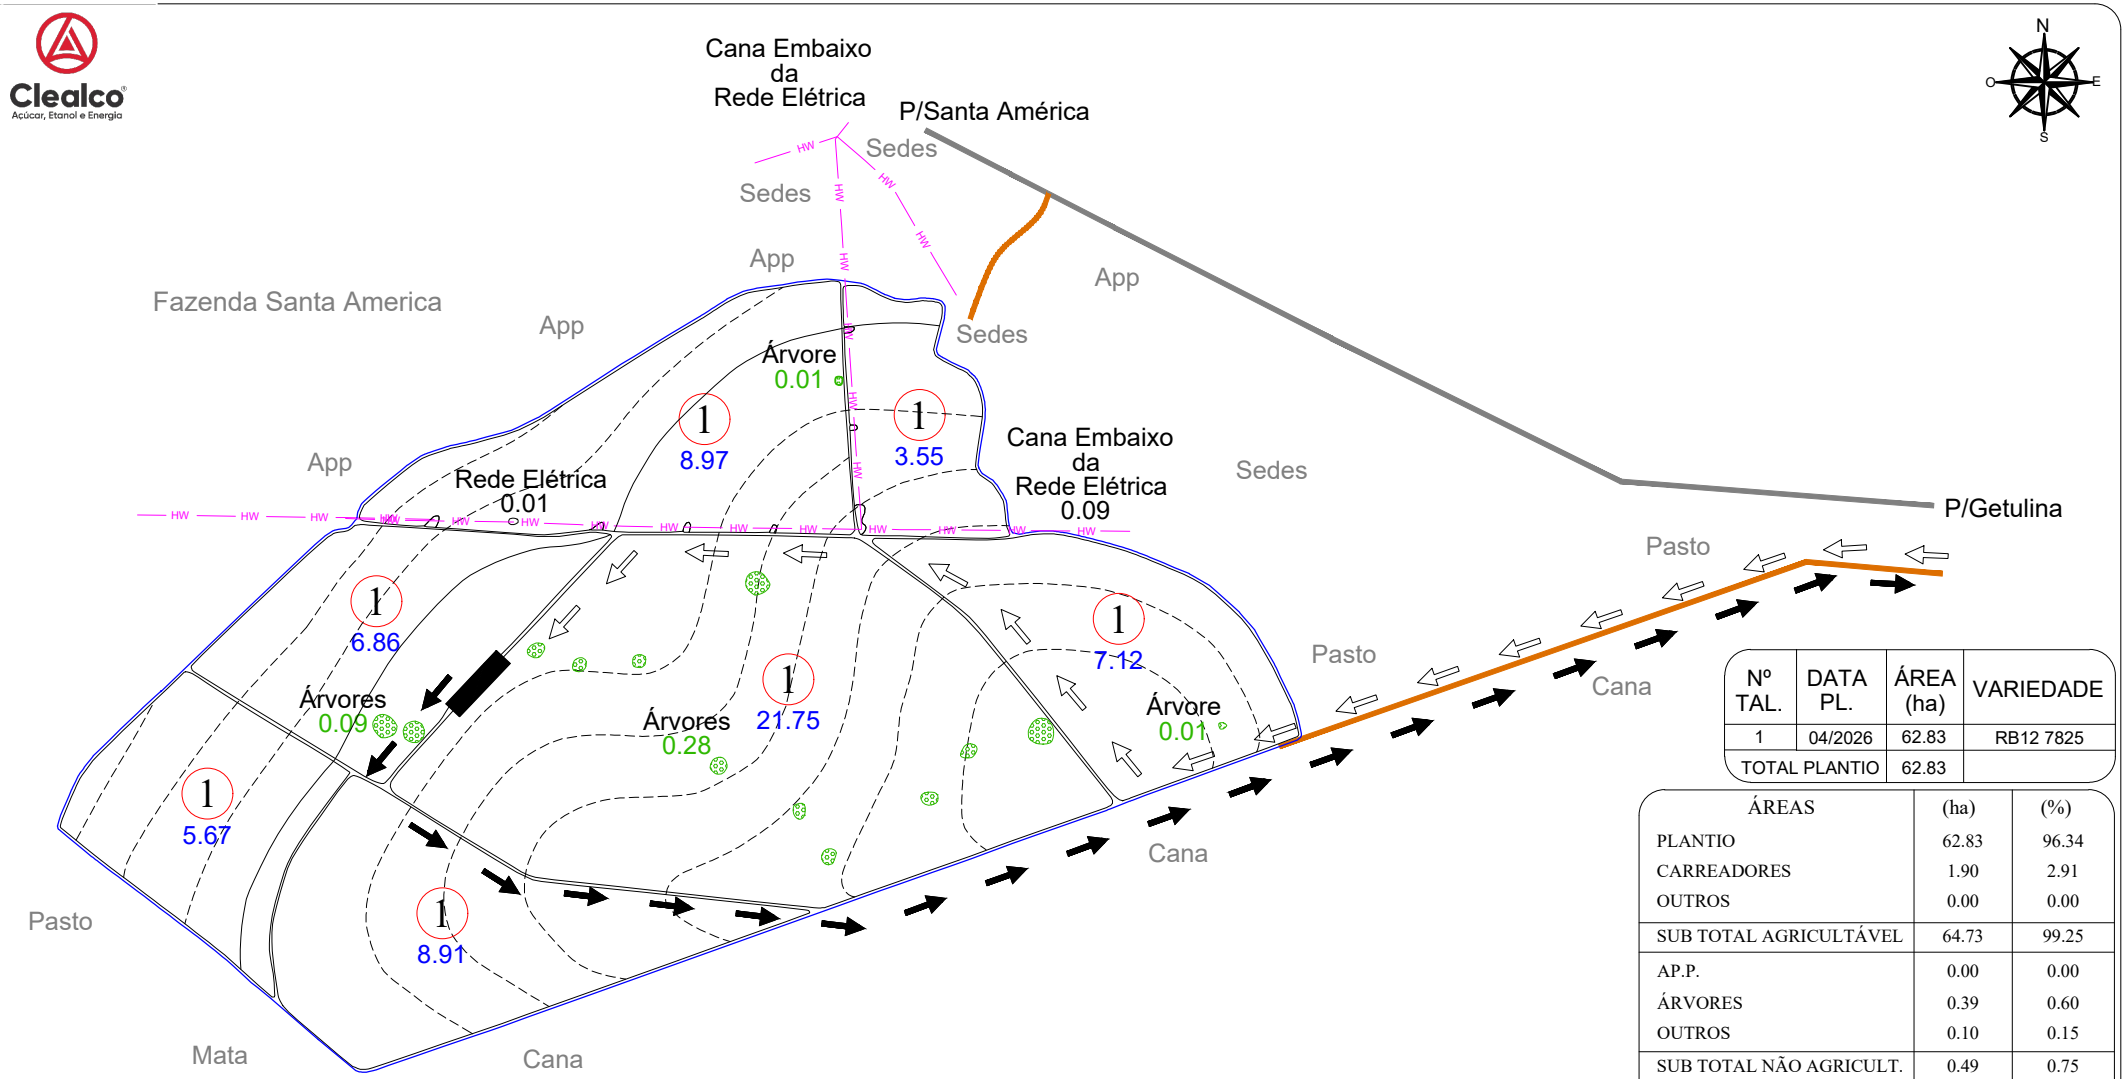


Nº TAL.	DATA PL.	ÁREA (ha)	VARIEDADE
1	04/2026	62.83	RB12 7825
TOTAL PLANTIO		62.83	

ÁREAS	(ha)	(%)
PLANTIO	62.83	96.34
CARREADORES	1.90	2.91
OUTROS	0.00	0.00
SUB TOTAL AGRICULTÁVEL	64.73	99.25
AP.P.	0.00	0.00
ÁRVORES	0.39	0.60
OUTROS	0.10	0.15
SUB TOTAL NÃO AGRICULT.	0.49	0.75
ÁREA TOTAL	65.22	100.00


C. NÍVEL: 1137.32 m/l 0.26 ha 0.40 %

ESCALA: 1: 9.500

LEGENDA
- FAZENDA
- TALHÃO
- REDE ELÉTRICA
- TERRAÇO BASE LARGA
- TERRAÇO EMBUTIDO
- VAZIO
- CARREGADO

ESPAÇAMENTO: 1.50 x 1.50
TIRO MÉDIO ESTIMADO: 264.42 m
D.V: 6.37 %

CROQUI DE ACESSO

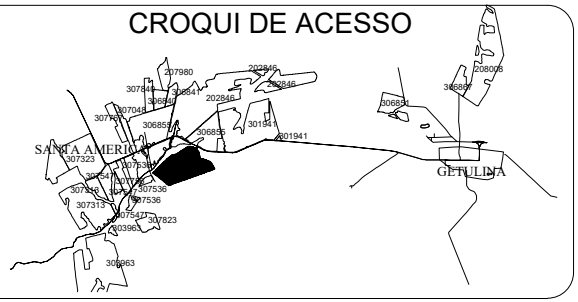

SÍTIO METODIO III

PROPRIETÁRIO: RAFAEL FRANCISCO V. A. CAPUTO
COMPRADOR: CLEALCO
MUNICÍPIO: GETULINA - SP

DISTÂNCIAS (km):
UNID. I - Asfalto: 80.00 Terra.: 0.00
UNID.I I - Asfalto: 27.30 Terra.: 0.00

COORDENADAS: E(X): 599175.06 N(Y): 7589144.32
LAT: -21°47'55.3579" LONG: -50°2'26.0744"
CLEALCO - AÇÚCAR E ALCOOL S/A - DEPARTAMENTO DE GEOTECNOLOGIA

LEVANTAMENTO VIA:
- SATÉLITE
- GPS / VANT
- GOOGLE

UNIDADE: II
PARTE: A/A
FUNDO AGRÍCOLA: 302459

M:\01-Mapa de safra\Mapas Atualizados\Terceiro\302459 - Sítio Metódio III (Rafael Francisco Vilatoro Aparicio Caputo)\302459 - Sítio Metódio III (Rafael Francisco Vilatoro Aparicio Caputo).dwg

Bruno Gamboa 27/08/26