| ZONA D.V. | Nº TAL. | DATA PL. | ÁREA (ha) | VAR. |
|---|---|---|---|---|
| 999 5.27 % | 1 | 06/2022 | 21.27 | RB975242 |
| | 2 | | 26.98 | |
| | 3 | | 28.02 | |
| TOTAL PLANTIO | | | 76.27 | -------- |


| ÁREAS | (ha) | (%) |
|---|---|---|
| PLANTIO | 76.27 | 96.58 |
| CARREADORES | 2.64 | 3.34 |
| OUTROS | 0.00 | 0.00 |
| SUB TOTAL AGRICULTÁVEL | 78.91 | 99.92 |
| AP.P. | 0.00 | 0.00 |
| ÁRVORES | 0.06 | 0.08 |
| OUTROS | 0.00 | 0.00 |
| SUB TOTAL NÃO AGRICULT. | 0.06 | 0.08 |
| ÁREA TOTAL | 78.97 | 100.00 |

C. NÍVEL: 0.00 m/l 0.00 ha 0.00 %

LEGENDA


- FAZENDA
- TALHÃO
- CURVA DE NÍVEL
- CARREADOR
- CONFRONTANTE
- REDE ELÉTRICA
- TRAJETO VAZIO
- TRAJETO CARREGADO

PLANTIO MANUAL - ESPAÇAMENTO: 1.50 X 1.50

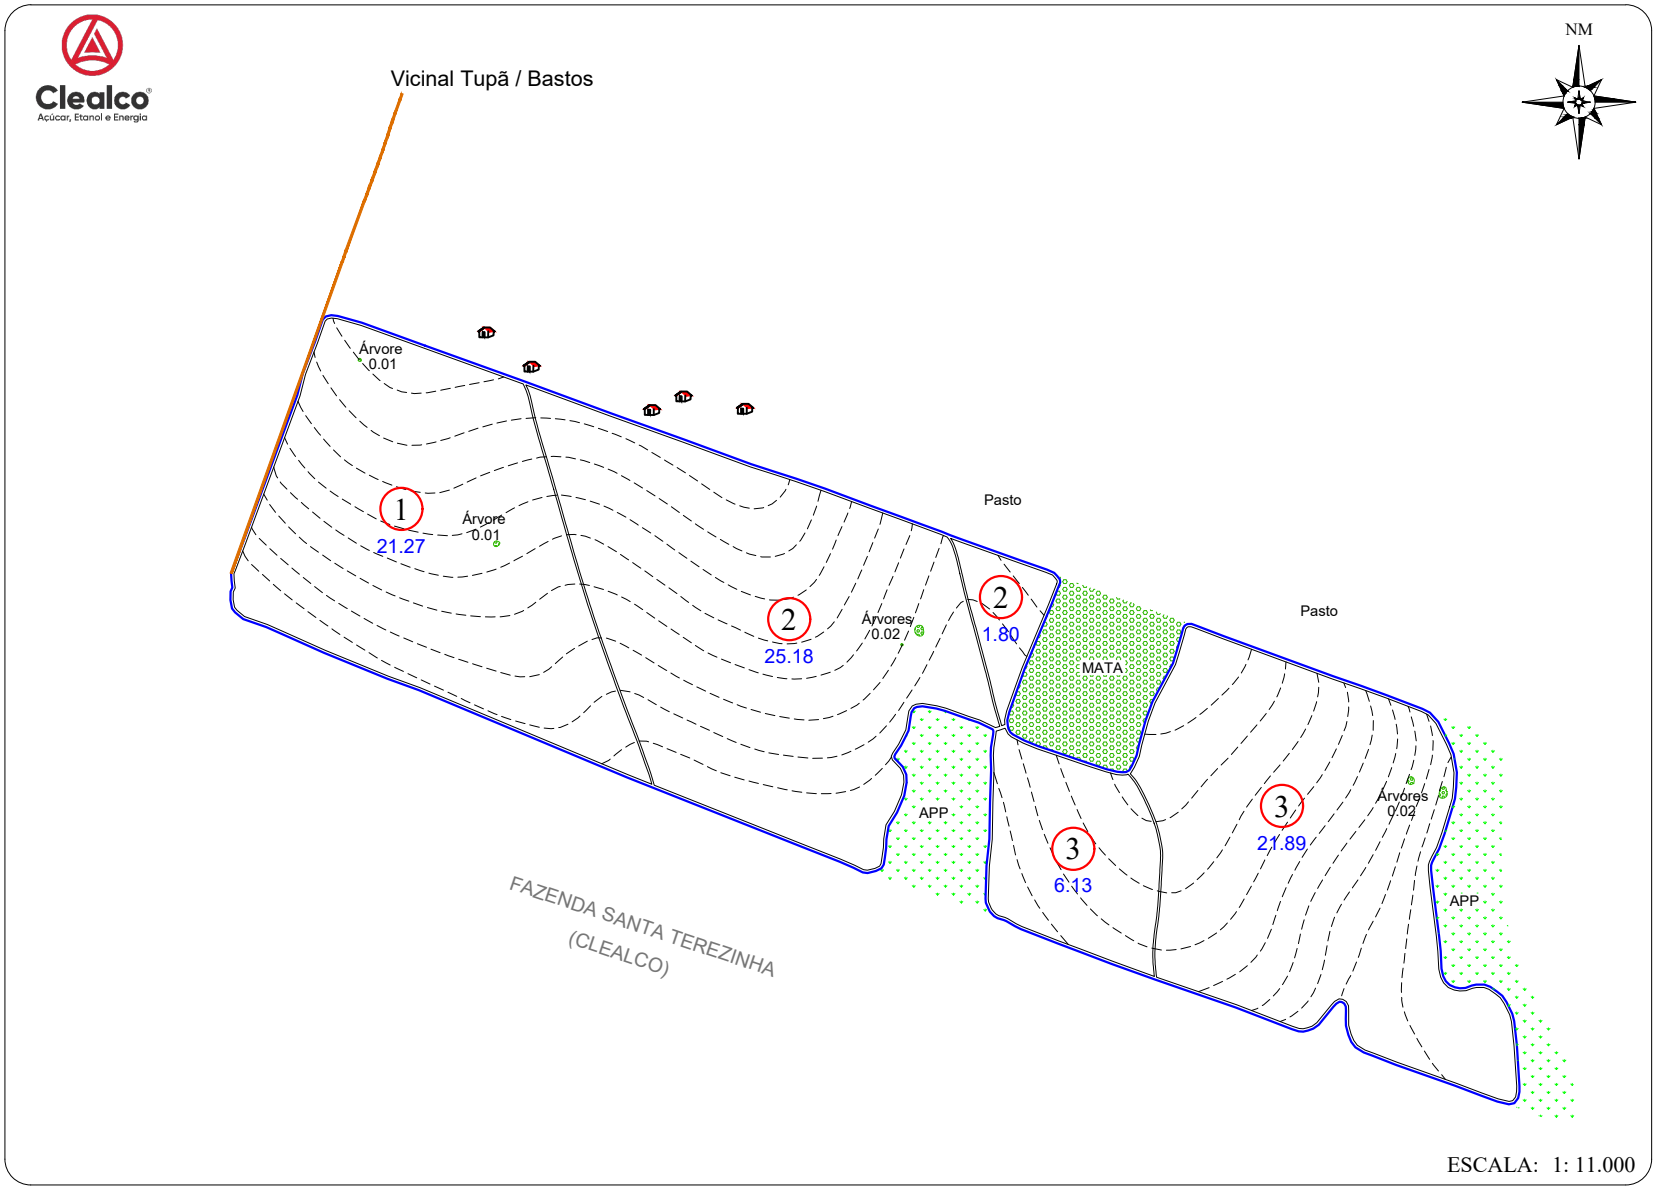


ESCALA: 1: 11.000

CROQUI DE ACESSO

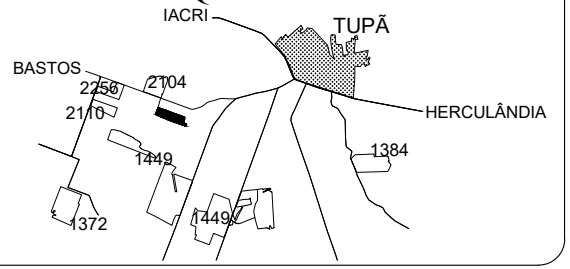


# ESTÂNCIA GLÓRIA

PROPRIETÁRIO: DIOGO APARECIDO DE AMORIM
COMPRADOR: CLEALCO S/A
MUNICÍPIO: TUPÃ

DISTÂNCIAS (km):
UNID. I - Asfalto: 66.50 Terra.: 0.50
UNID.I I - Asfalto: 58.00 Terra.: 0.50
UNID. III -Asfalto: 114.00 Terra.: 0.50

COORDENADAS: E(X): 541401.29 N(Y): 7571152.39
LAT: 21° 57' 48,53837" LONG: 50° 35' 56,44366"

CLEALCO - AÇÚCAR E ALCOOL S/A - DEPARTAMENTO DE TOPOGRAFIA

UNIDADE: I

PARTE: A/A

FUNDO AGRÍCOLA: 302964

M:\01-Mapa de safra\Mapas Atualizados\Terceiro\302964 - Estancia Gloria (Osmar Antonio Capiotto)\302964 - Estancia Gloria (Osmar Antonio Capiotto).dwg