

Clealco
Açúcar, Etanol e Energia

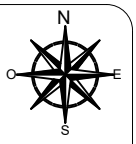

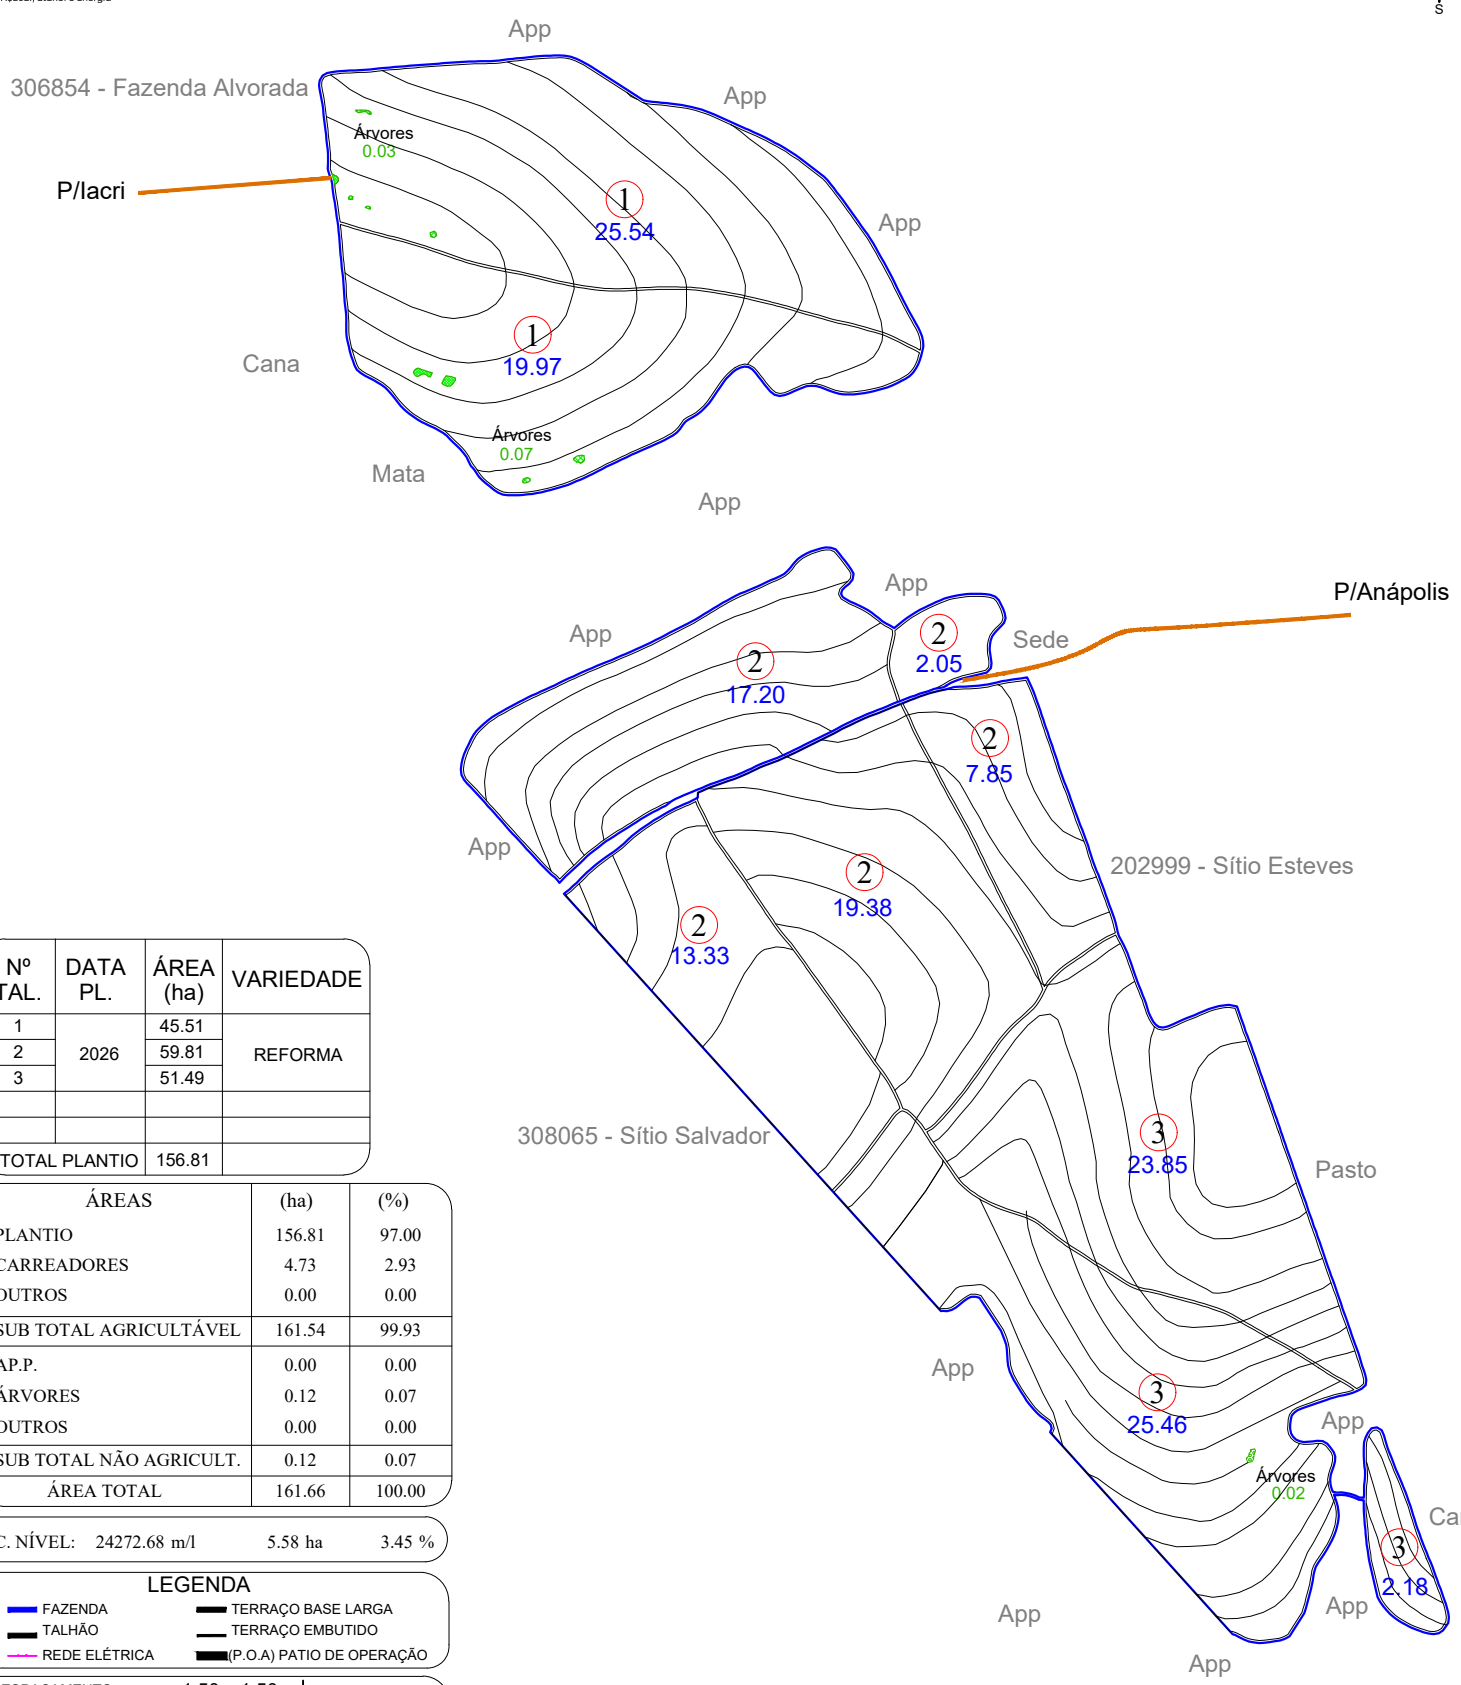

Nº TAL.	DATA PL.	ÁREA (ha)	VARIEDADE
1	2026	45.51	REFORMA
2		59.81	
3		51.49	
TOTAL PLANTIO		156.81	

ÁREAS	(ha)	(%)
PLANTIO	156.81	97.00
CARREADORES	4.73	2.93
OUTROS	0.00	0.00
SUB TOTAL AGRICULTÁVEL	161.54	99.93
AP.P.	0.00	0.00
ÁRVORES	0.12	0.07
OUTROS	0.00	0.00
SUB TOTAL NÃO AGRICULT.	0.12	0.07
ÁREA TOTAL	161.66	100.00

C. NÍVEL: 24272.68 m/l 5.58 ha 3.45 %


LEGENDA

- FAZENDA
- TALHÃO
- REDE ELÉTRICA
- TERRAÇO BASE LARGA
- TERRAÇO EMBUTIDO
- (P.O.A) PATIO DE OPERAÇÃO

ESPAÇAMENTO: 1.50 x 1.50
TIRO MÉDIO ESTIMADO: 000.00 m
D.V: 4.94 %

ESCALA: 1: 12.500

CROQUI DE ACESSO

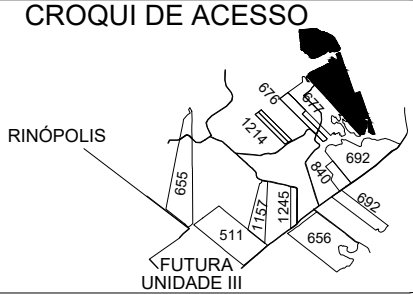

FAZENDA PORTAL DO SOL

PROPRIETÁRIO: ROBERLEI BUENO DE OLIVEIRA
COMPRADOR: CLEALCO
MUNICÍPIO: IACRI - SP

DISTÂNCIAS (km):
UNID. I - Asfalto: 36.70 Terra.: 15.00
UNID.I I - Asfalto: 50.20 Terra.: 15.00

COORDENADAS: E(X): 546138.37 N(Y): 7592396.73
LAT: -21°46'17.4345" LONG: -50°33'13.4197"

CLEALCO - AÇÚCAR E ALCOOL S/A - DEPARTAMENTO DE GEOTECNOLOGIA

LEVANTAMENTO VIA:
- SATÉLITE
- GPS / VANT
- GOOGLE

UNIDADE: I
PARTE: A/A
FUNDO AGRÍCOLA: 302996

M:\01-Mapa de safra\Mapas Atualizados\Terceiro\302996 - Fazenda Portal do Sol (Roberlei Bueno De Oliveira)\302996 - Fazenda Portal do Sol (Roberlei Bueno De Oliveira).dwg

Bruno Gamboa 19/01/26